
Client : SAUDI GLOBAL PORTS

Project : DAMMAM LOGISTICS ZONE

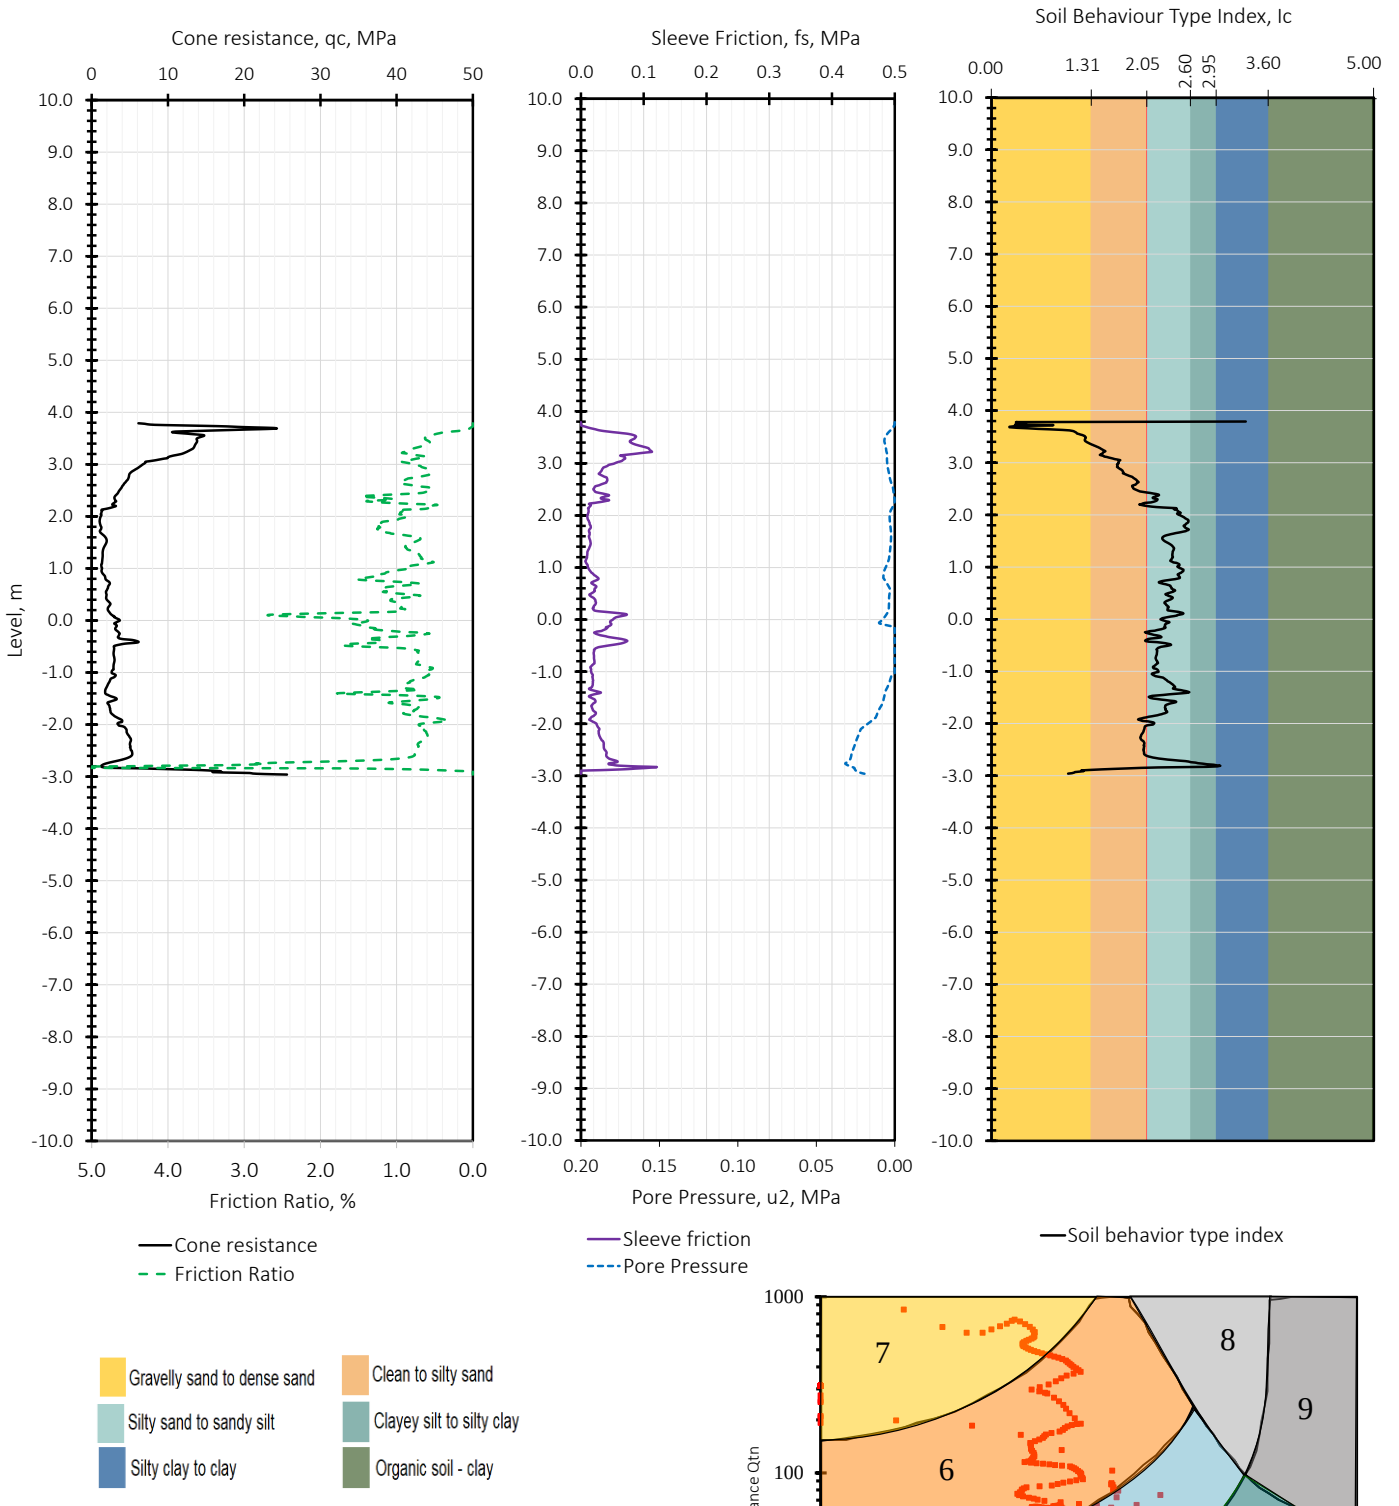

Main Contractor:	CTS GULF	
Test Location:	CPT-A1-294-100	
Ground Elevation:	3.79	
	Easting	**Northing**
Coordinates:	421106.843	2928384.109
Cone ID:	DP15-CFPTxy.71431	
Test Date	24-Sep-2026	