
Client : SAUDI GLOBAL PORTS

Project : DAMMAM LOGISTICS ZONE

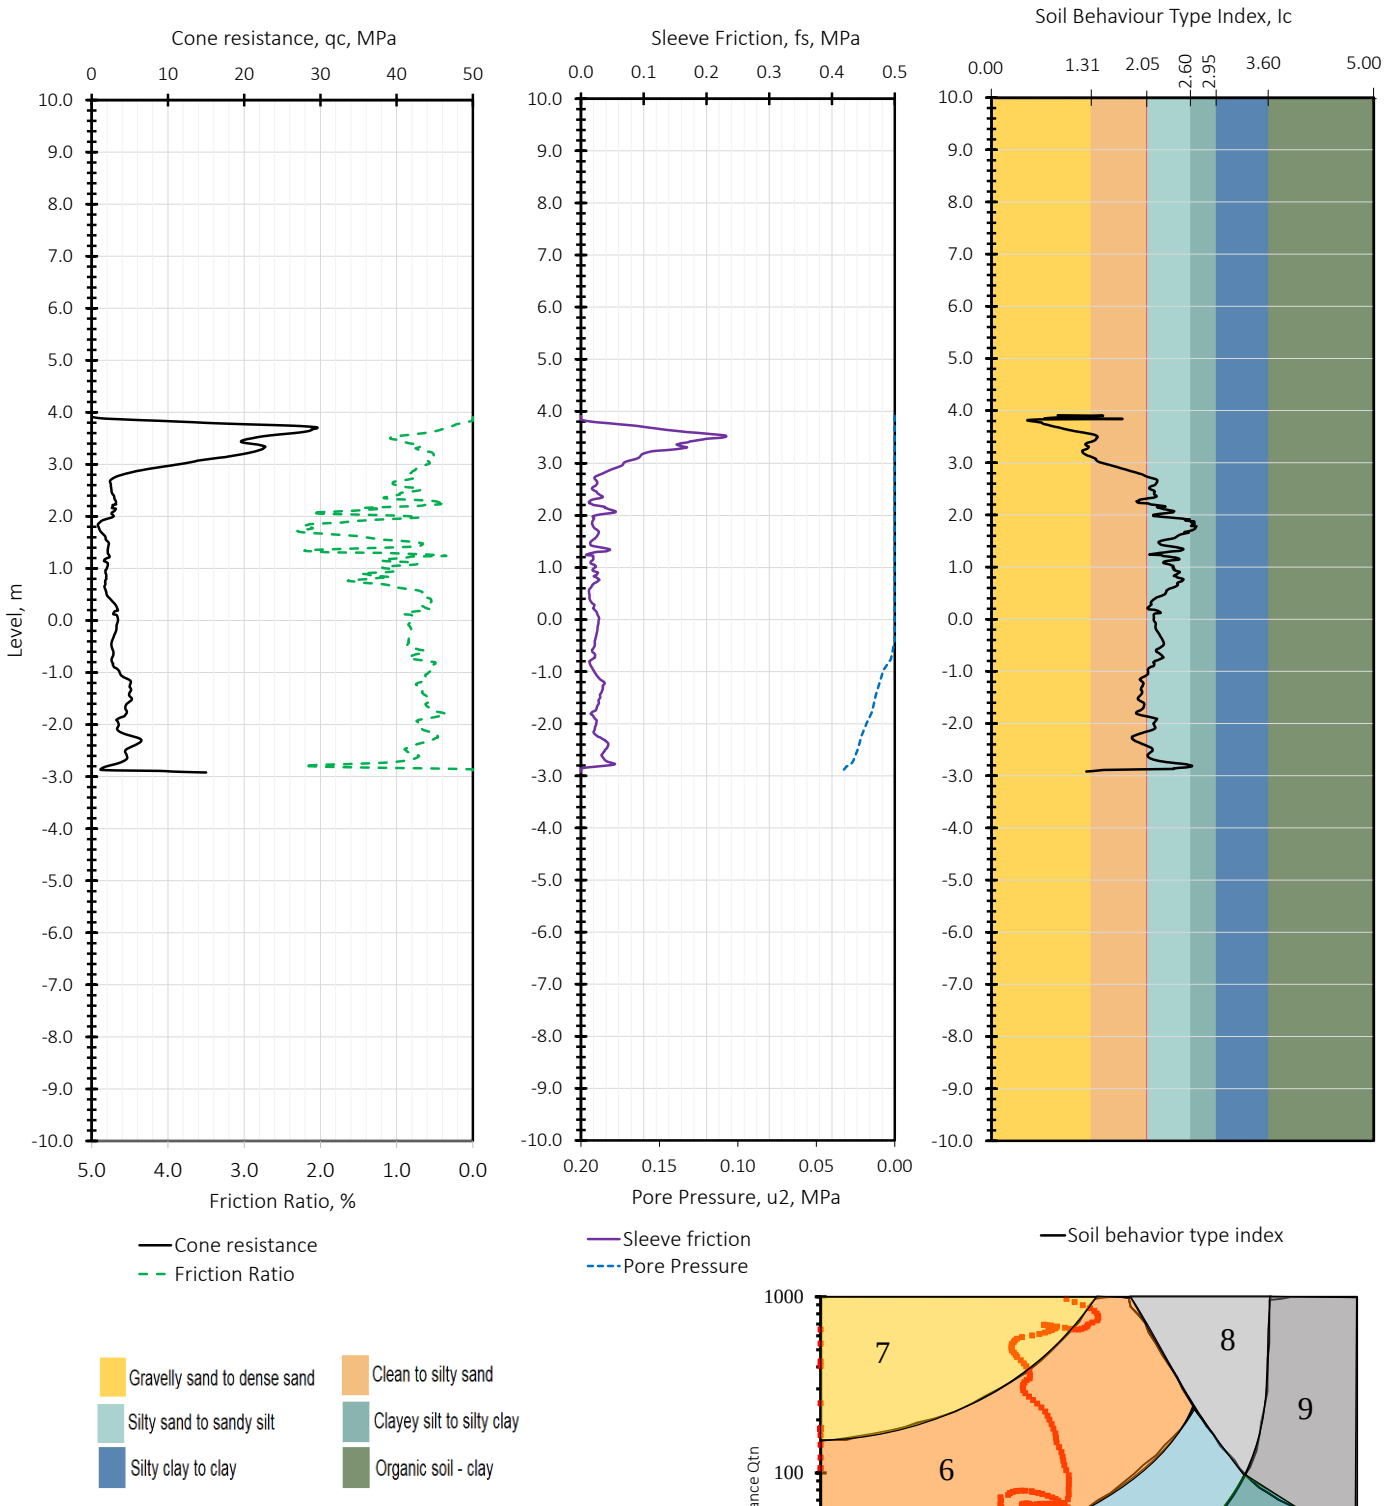

Main Contractor:	CTS GULF	
Test Location:	CPT-A1-295-100	
Ground Elevation:	3.91	
	Easting	**Northing**
Coordinates:	421106.235	2928411.755
Cone ID:	DP15-CFPTxy.71431	
Test Date	24-Sep-2026	