
Client : SAUDI GLOBAL PORTS

Project : DAMMAM LOGISTICS ZONE

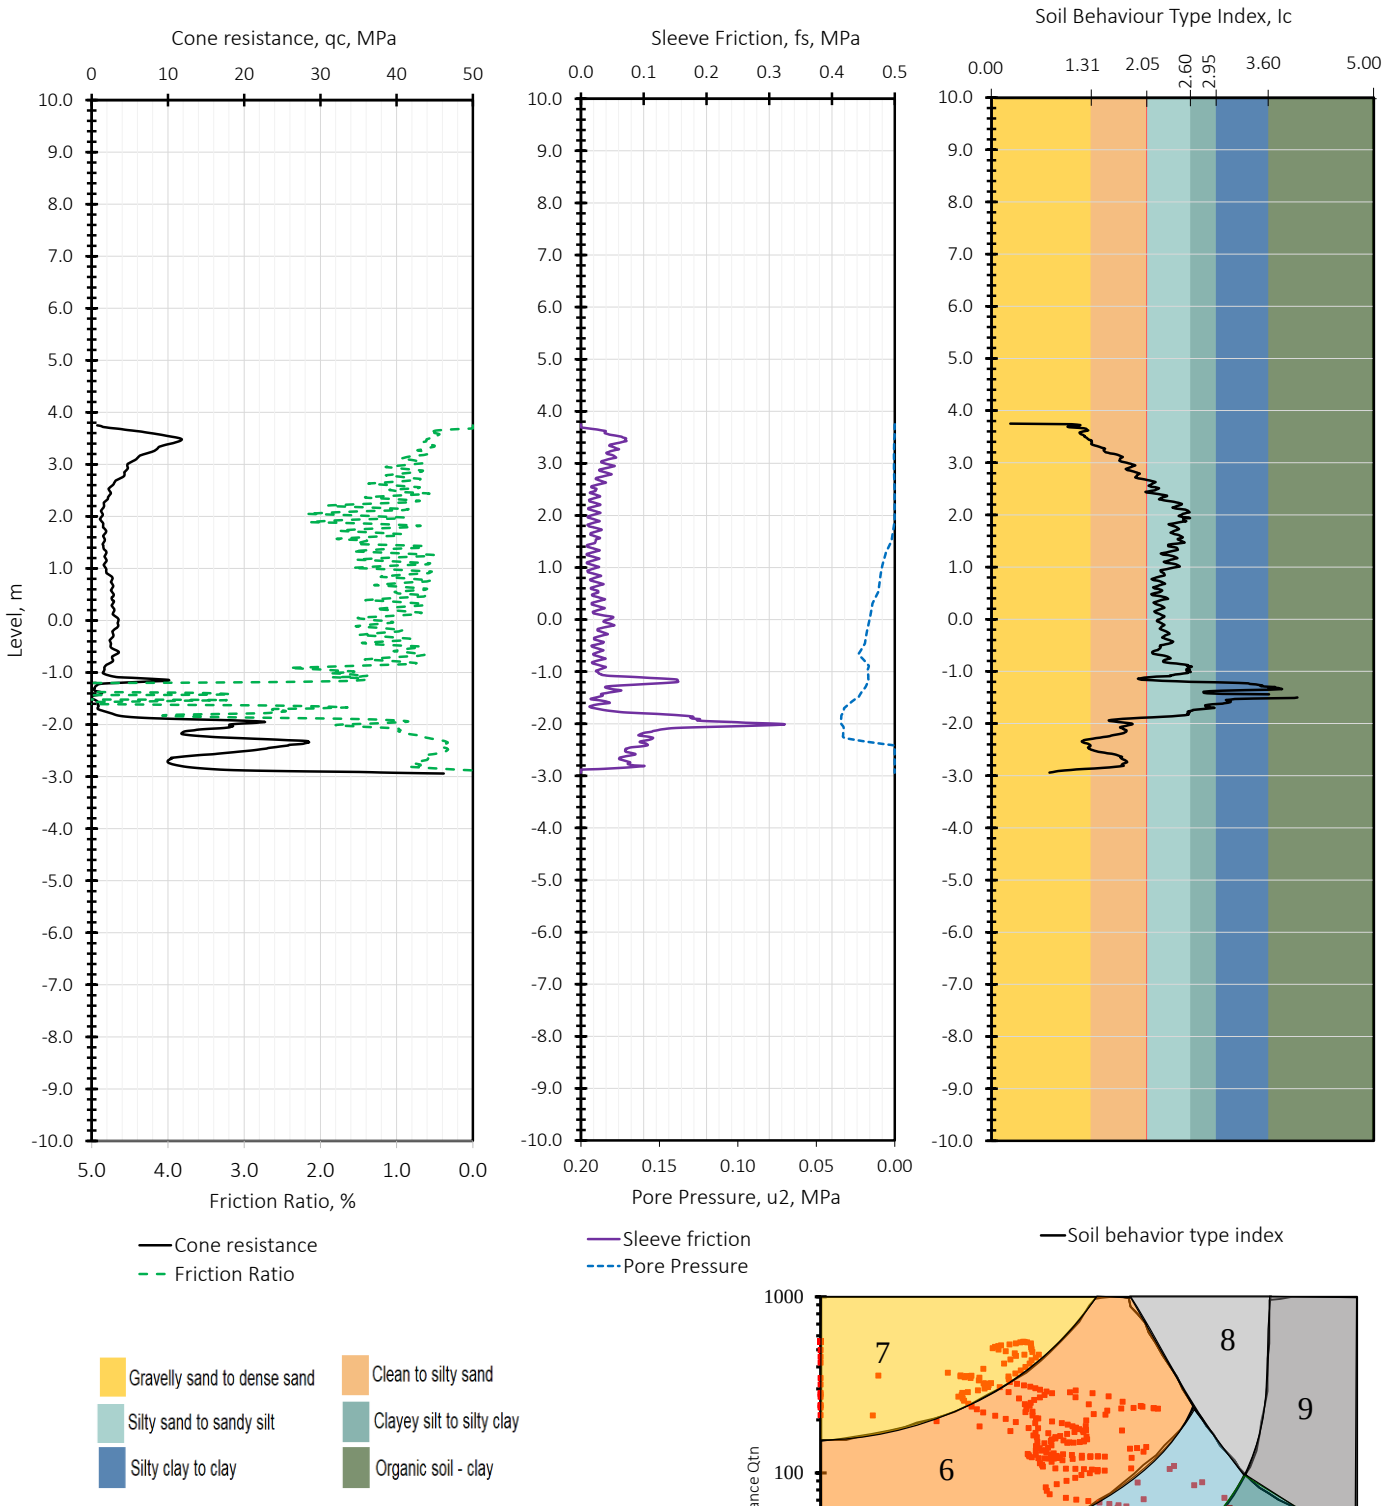

Main Contractor:	CTS GULF	
Test Location:	CPT-A1-B100-100	
Ground Elevation:	3.75	
	Easting	**Northing**
Coordinates:	420652.661	2927659.562
Cone ID:	DP15-CFPTxy.71431	
Test Date	12-Oct-2026	