
Client : SAUDI GLOBAL PORTS

Project : DAMMAM LOGISTICS ZONE

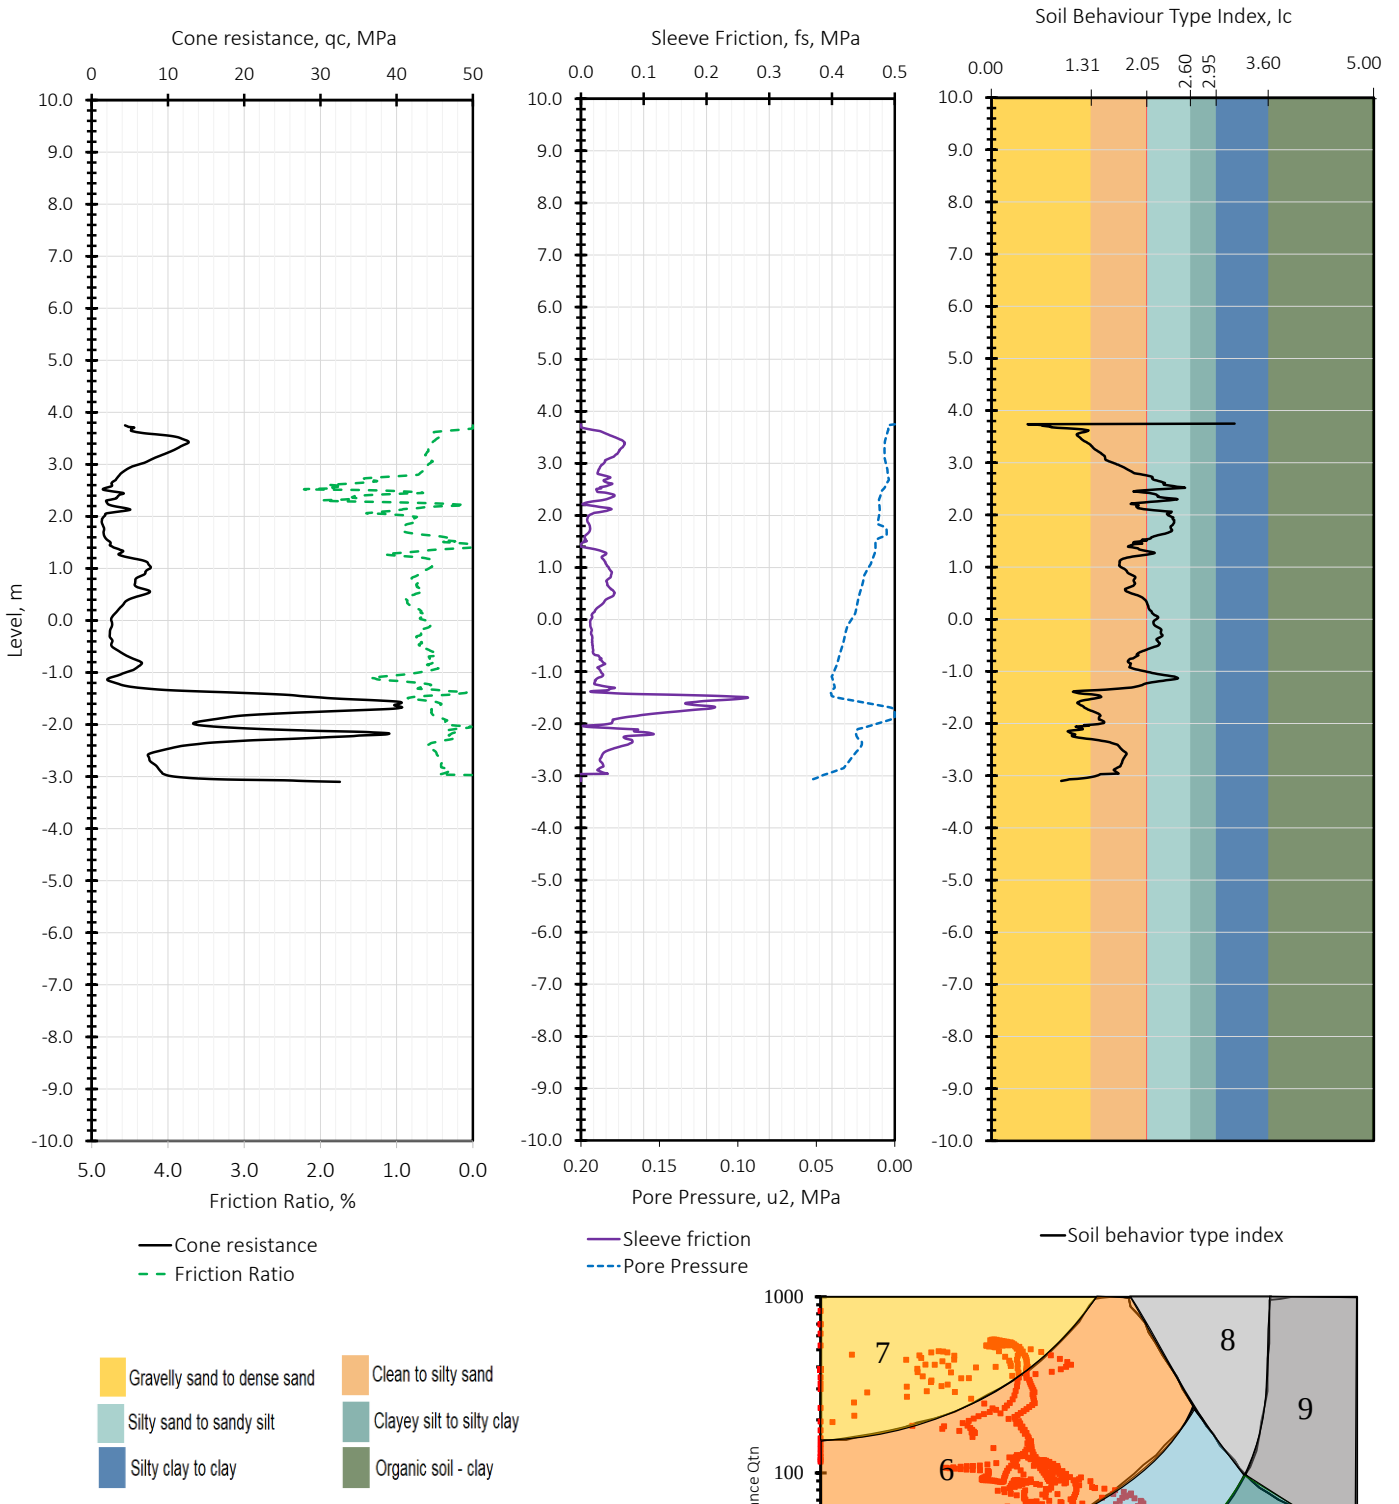

Main Contractor:	CTS GULF	
Test Location:	CPT-A1-B113-100	
Ground Elevation:	3.75	
	Easting	**Northing**
Coordinates:	420683.827	2927676.255
Cone ID:	DP15-CFPTxy.71424	
Test Date	11-Oct-2026	