

Client : SAUDI GLOBAL PORTS

Project : DAMMAM LOGISTICS ZONE

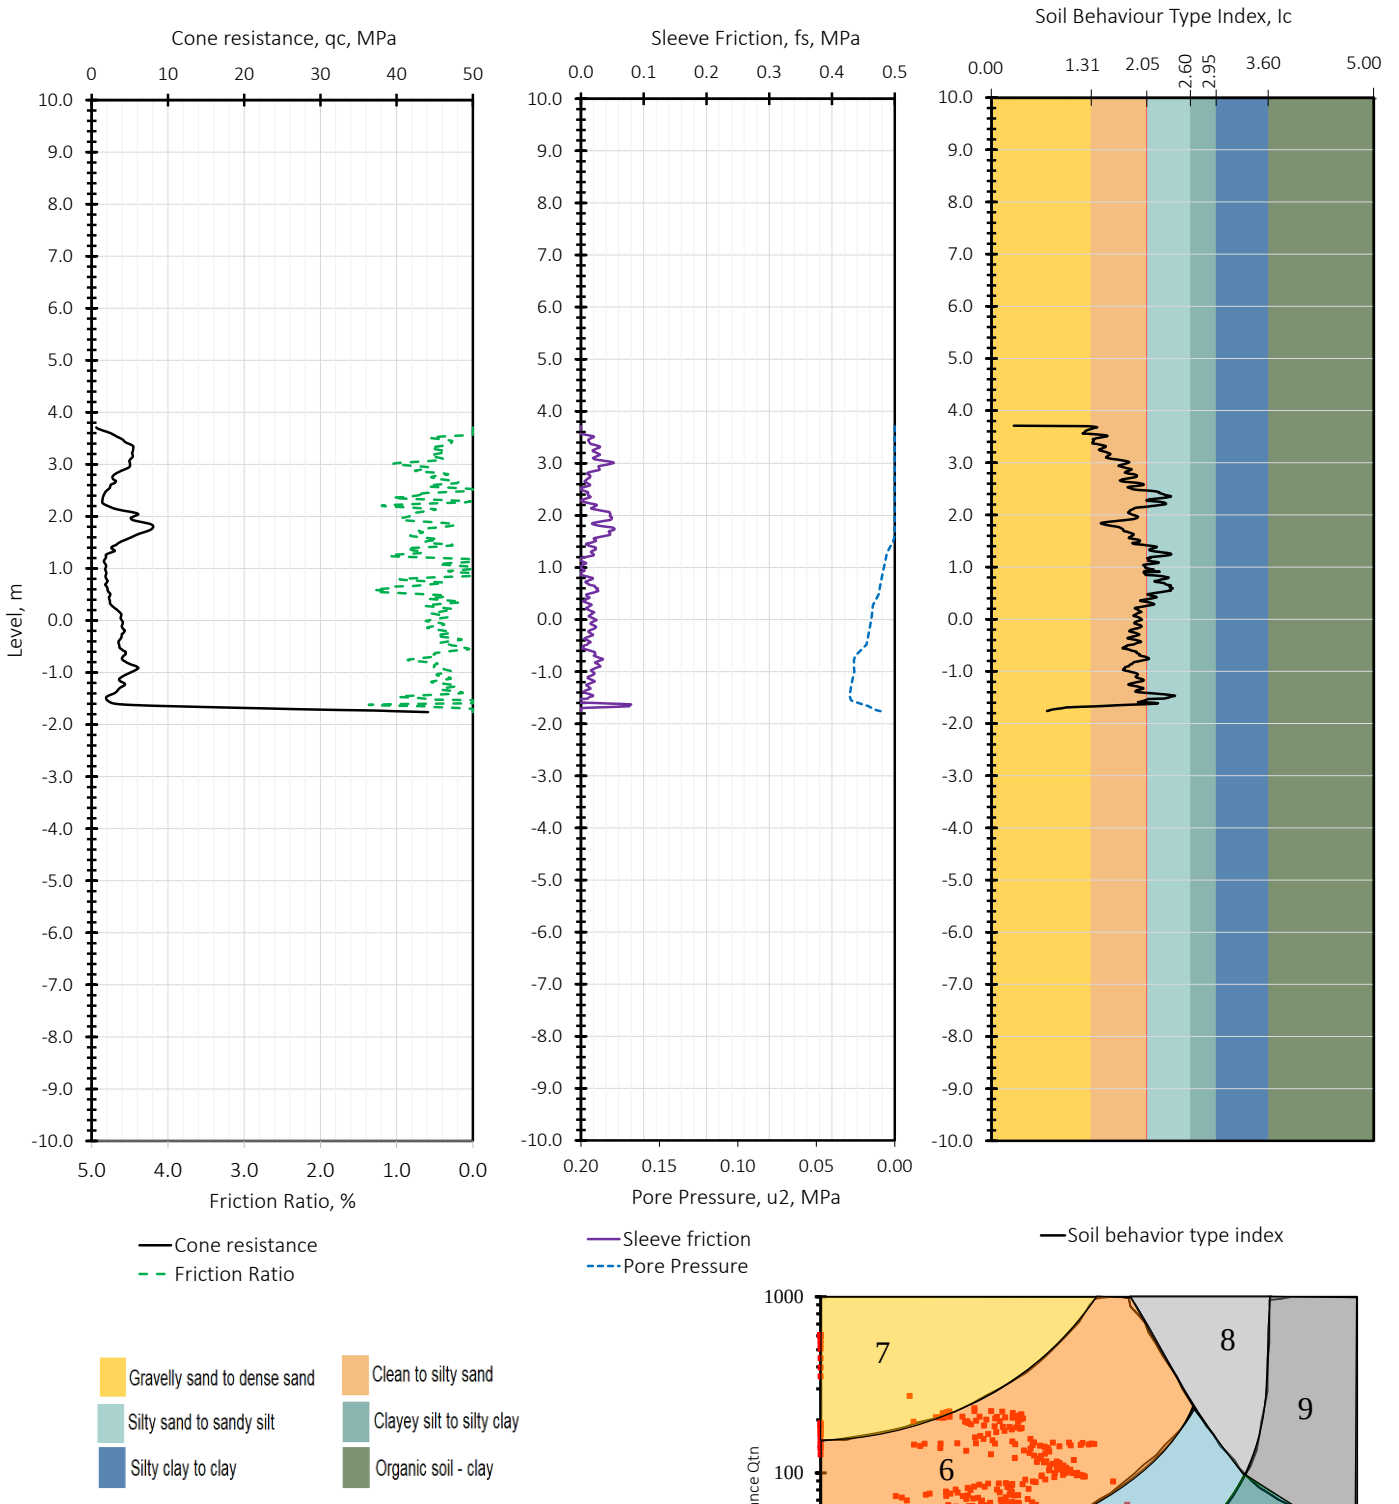

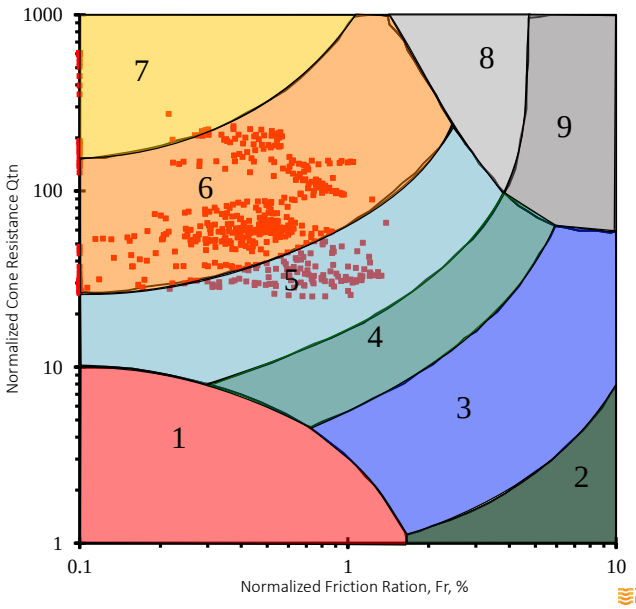

Main Contractor:	CTS GULF	
Test Location:	CPT-A1-B115-100	
Ground Elevation:	3.71	
	Easting	**Northing**
Coordinates:	421038.074	2927465.803
Cone ID:	DP15-CFPTxy.71431	
Test Date	10-Oct-2026	