

Client : SAUDI GLOBAL PORTS

Project : DAMMAM LOGISTICS ZONE

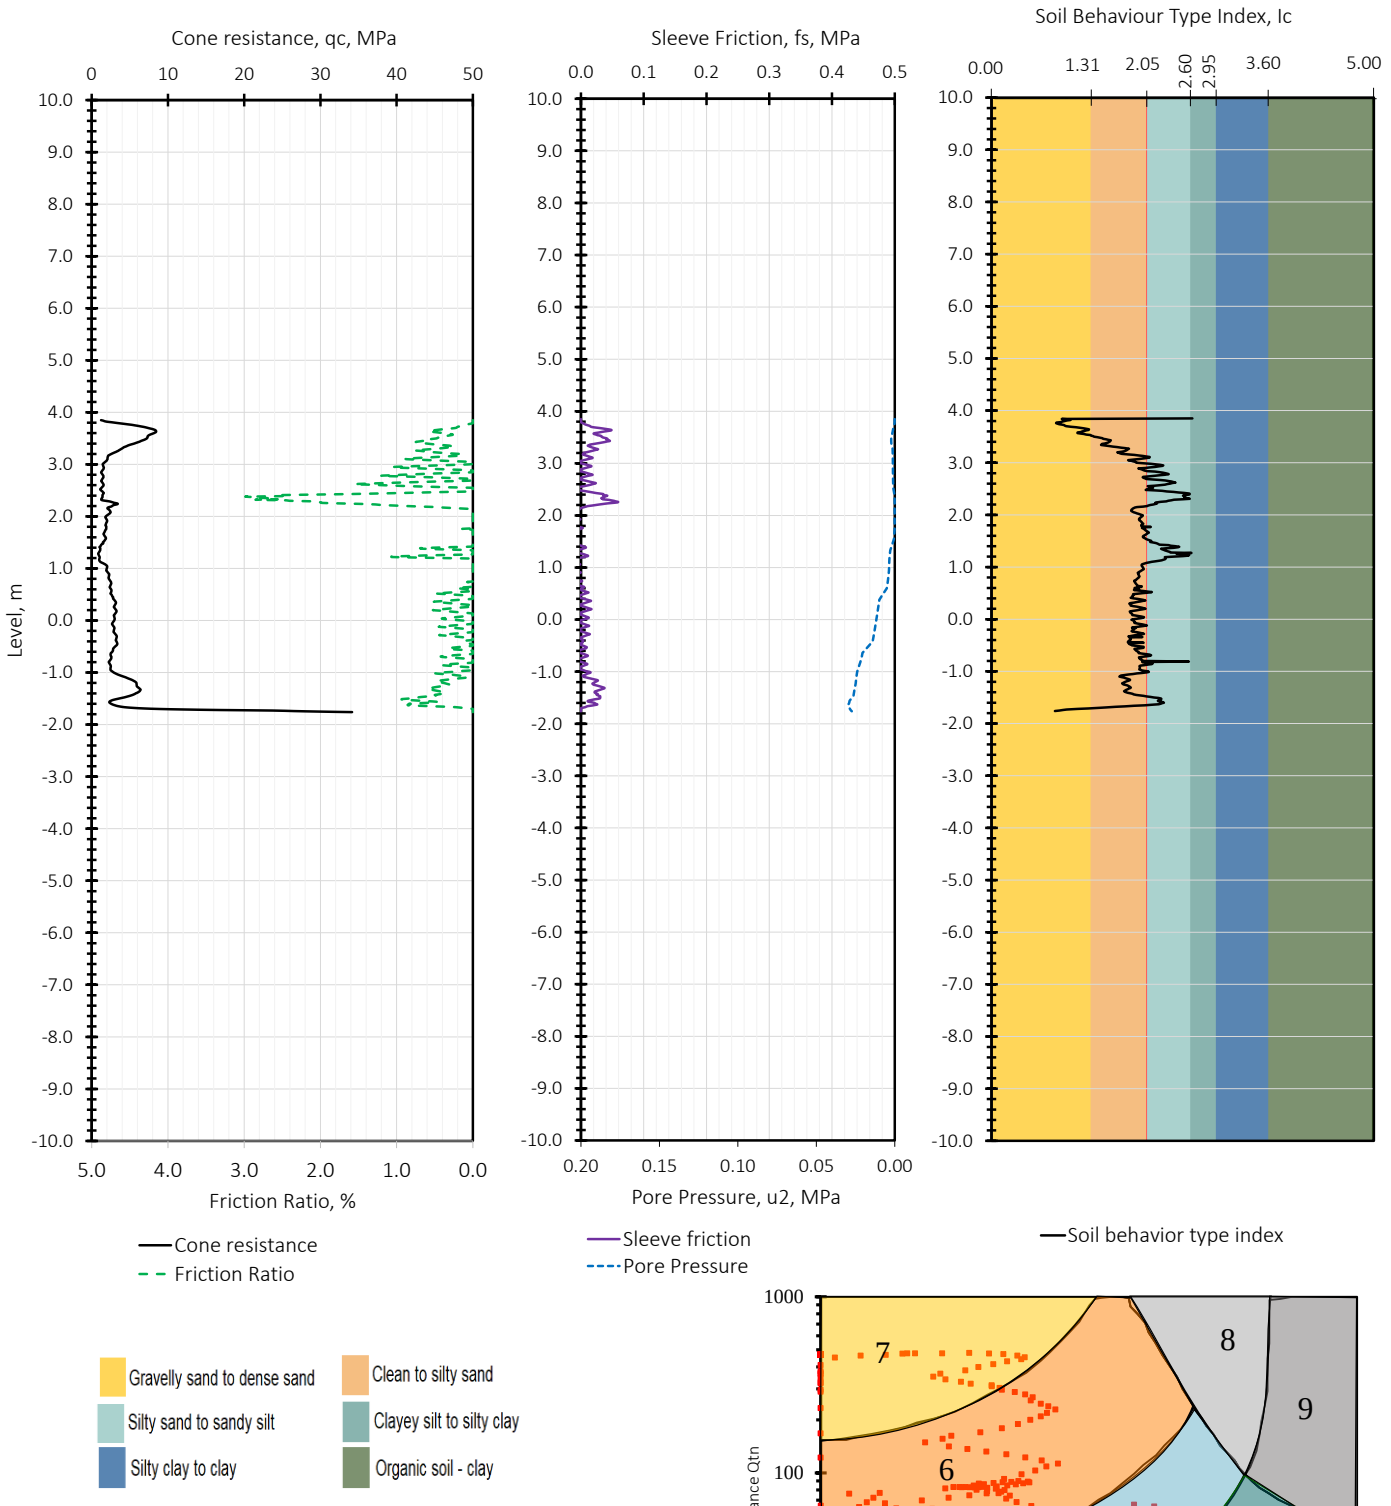

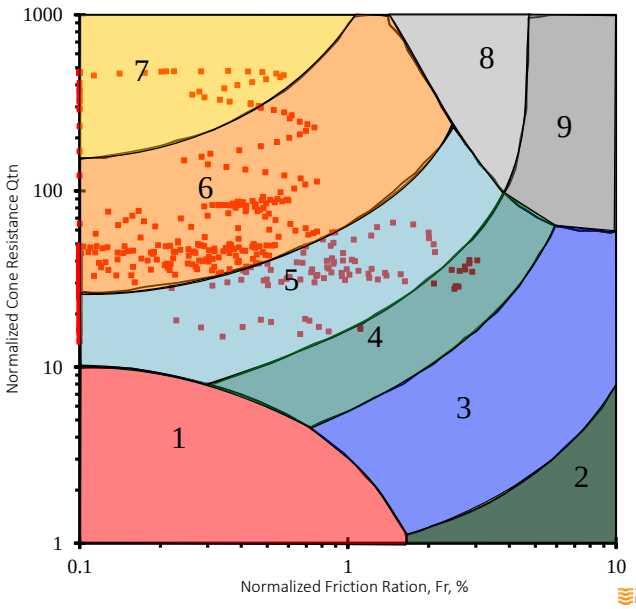

Main Contractor:	CTS GULF	
Test Location:	CPT-A1-B116-100	
Ground Elevation:	3.85	
	Easting	**Northing**
Coordinates:	421044.991	2927488.677
Cone ID:	DP15-CFPTxy.71431	
Test Date	10-Oct-2026	