
**Client : SAUDI GLOBAL PORTS**

**Project : DAMMAM LOGISTICS ZONE**

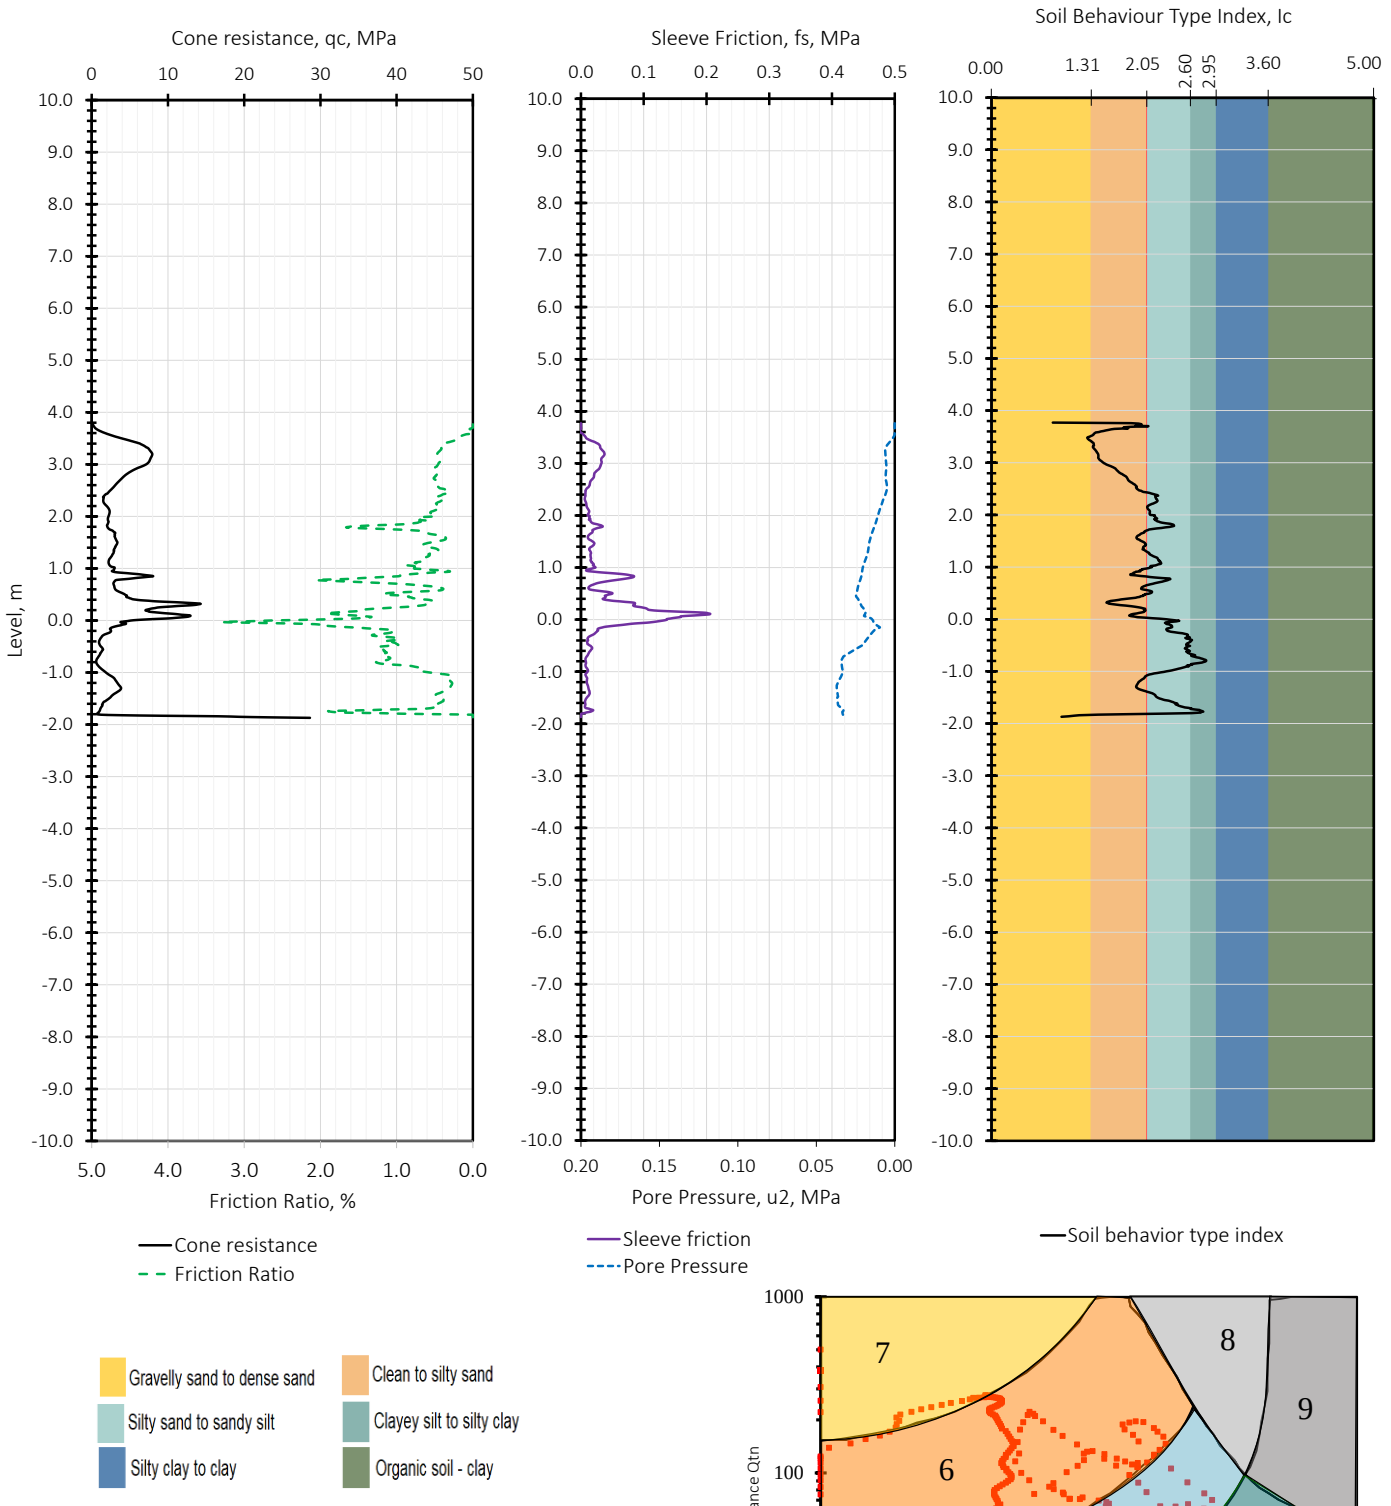


| | | |
|---|---|---|
| **Main Contractor:** | CTS GULF | |
| **Test Location:** | CPT-A1-B119-100 | |
| **Ground Elevation:** | 3.77 | |
| | **Easting** | **Northing** |
| **Coordinates:** | 420727.248 | 2927819.833 |
| **Cone ID:** | DP15-CFPTxy.71431 | |
| **Test Date** | 6-Oct-2026 | |