
Client : SAUDI GLOBAL PORTS

Project : DAMMAM LOGISTICS ZONE

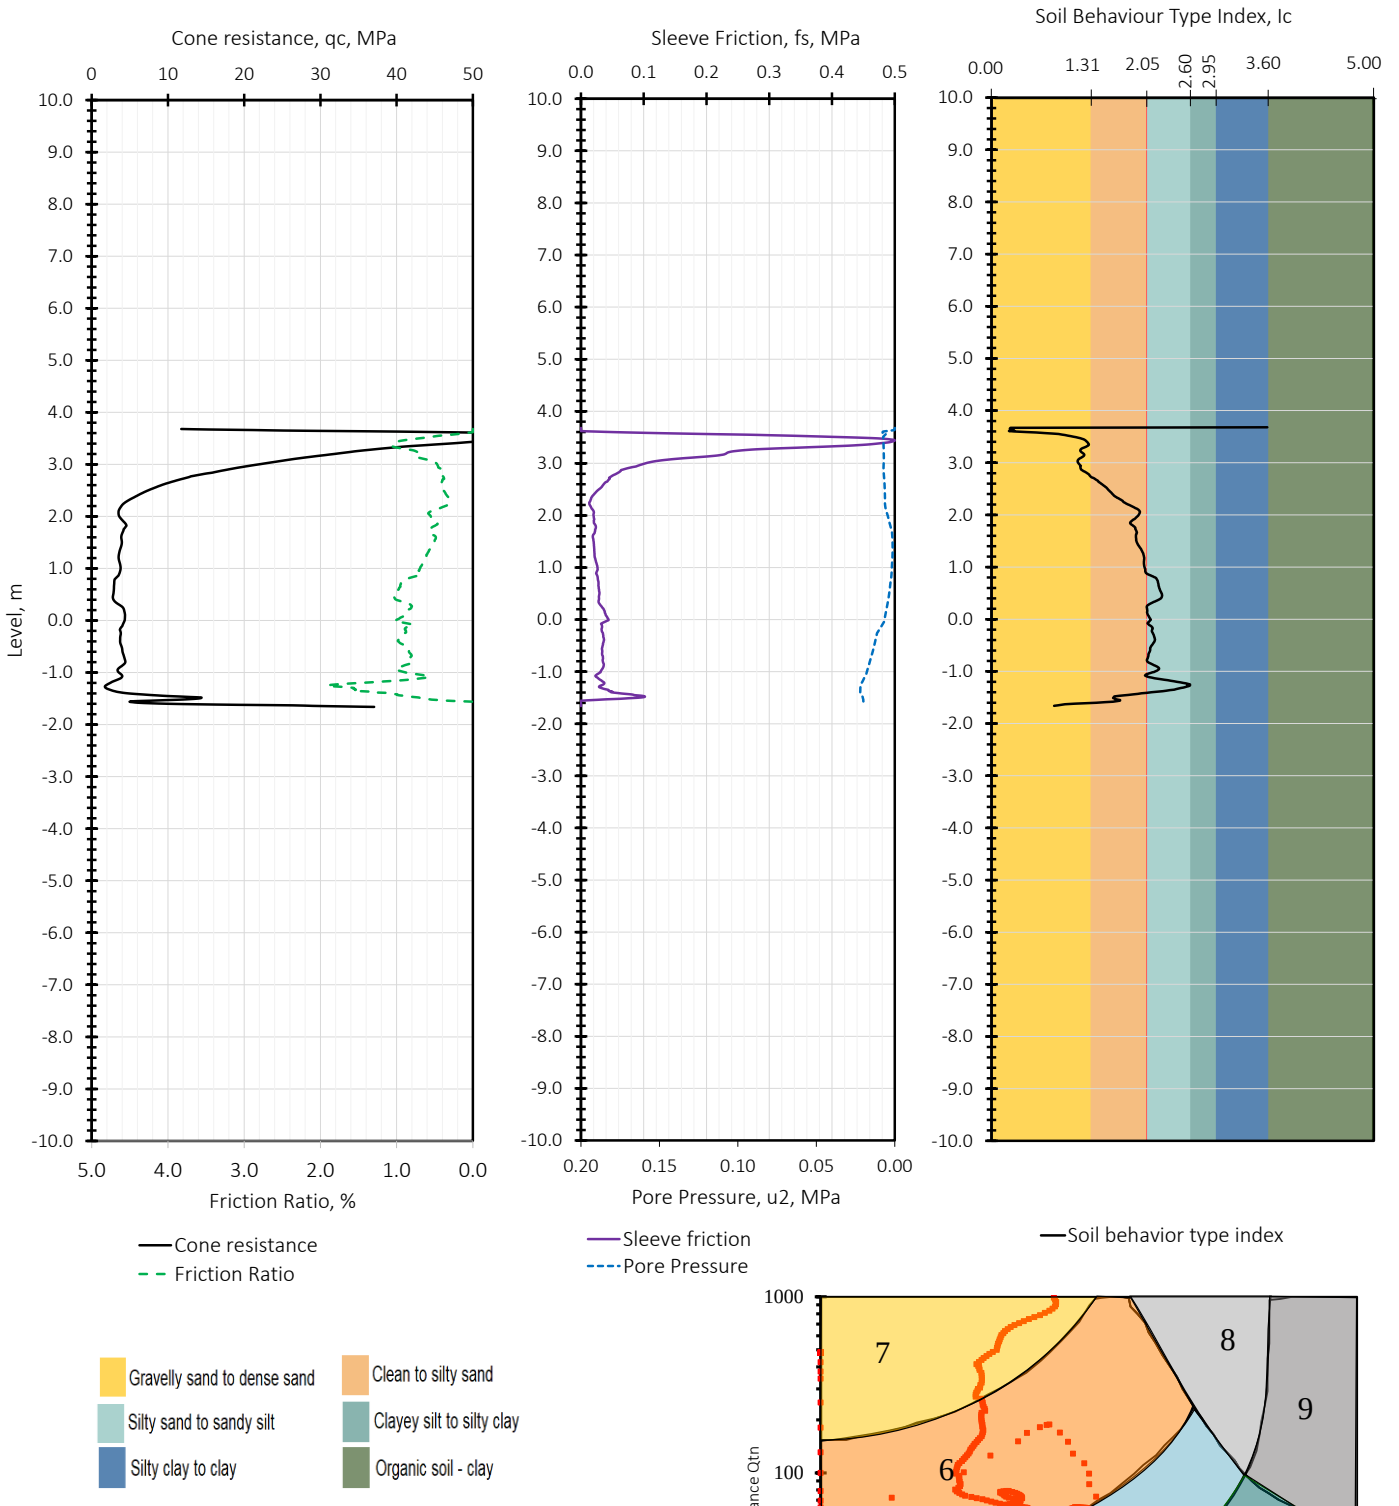

Main Contractor:	CTS GULF	
Test Location:	CPT-A1-B125-100	
Ground Elevation:	3.68	
	Easting	**Northing**
Coordinates:	420700.52	2927645.089
Cone ID:	DP15-CFPTxy.71424	
Test Date	11-Oct-2026	