

Client : SAUDI GLOBAL PORTS

Project : DAMMAM LOGISTICS ZONE

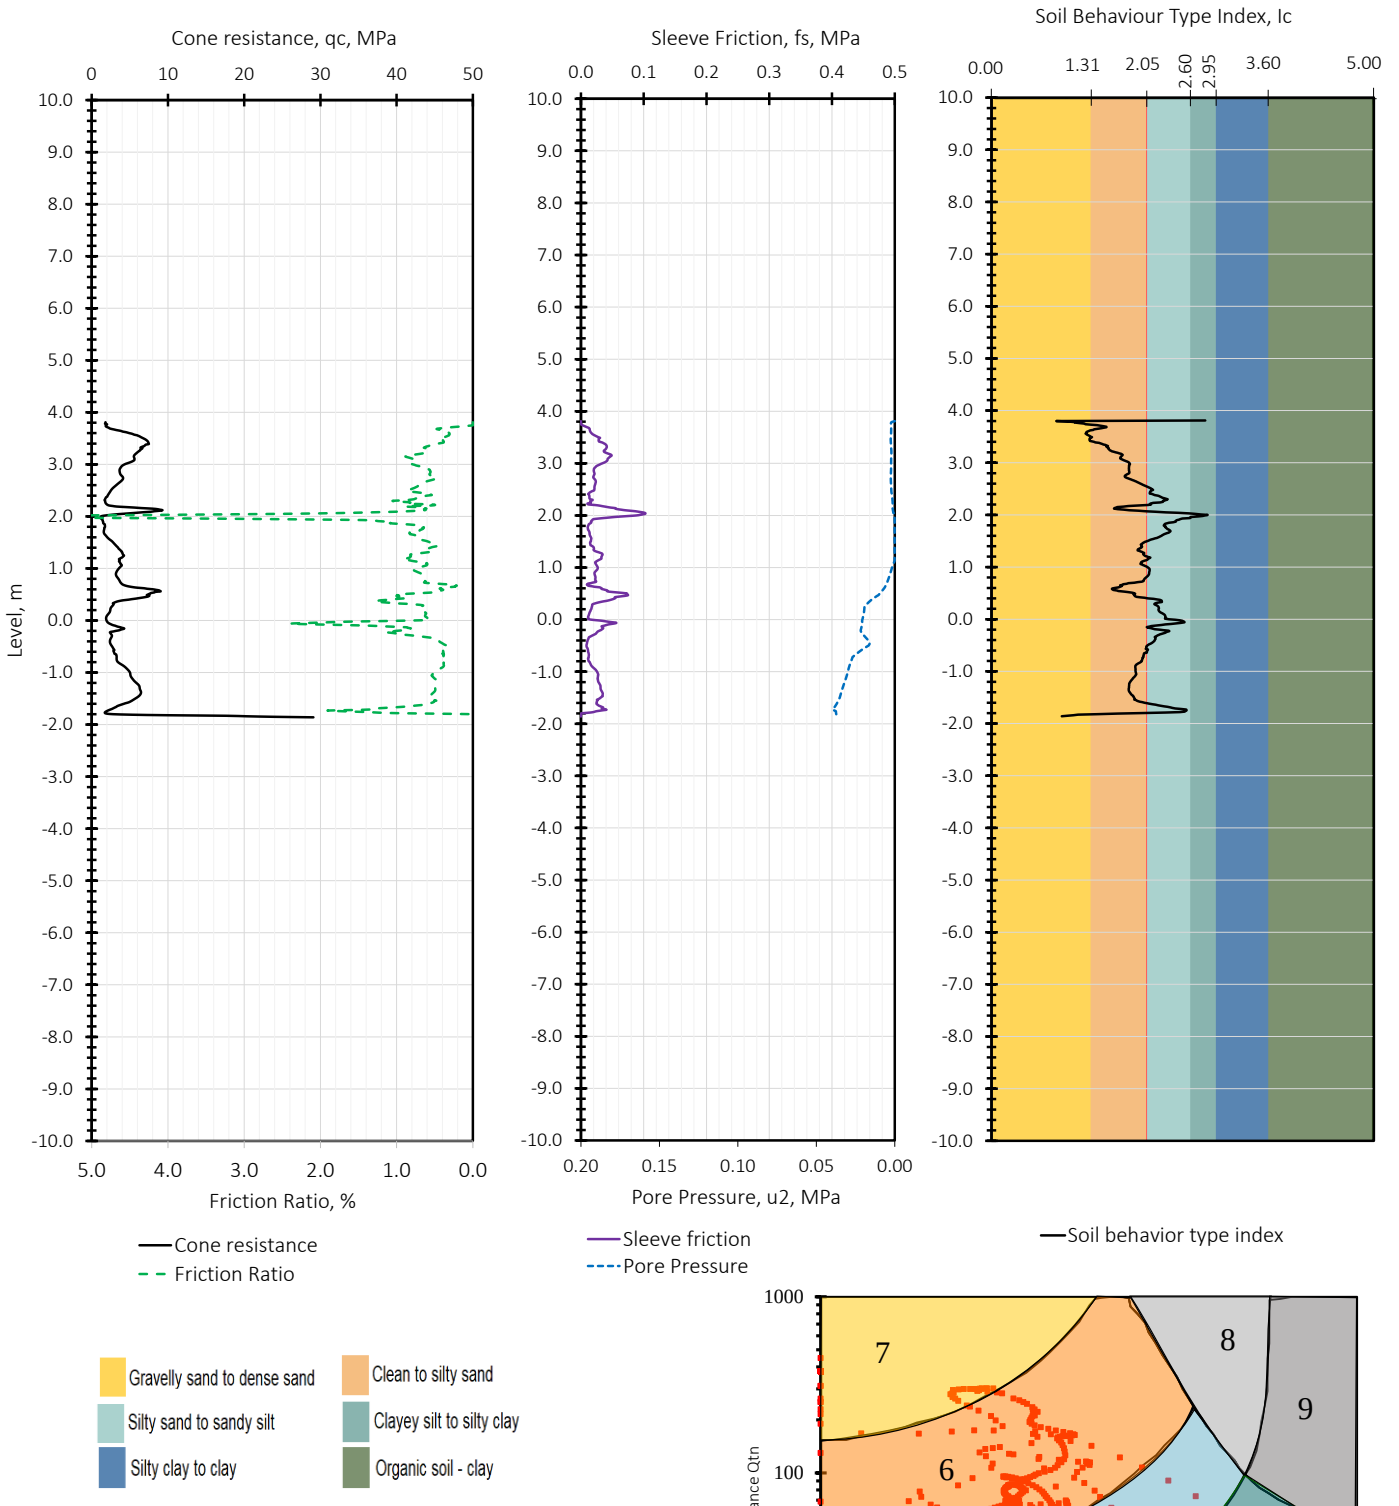

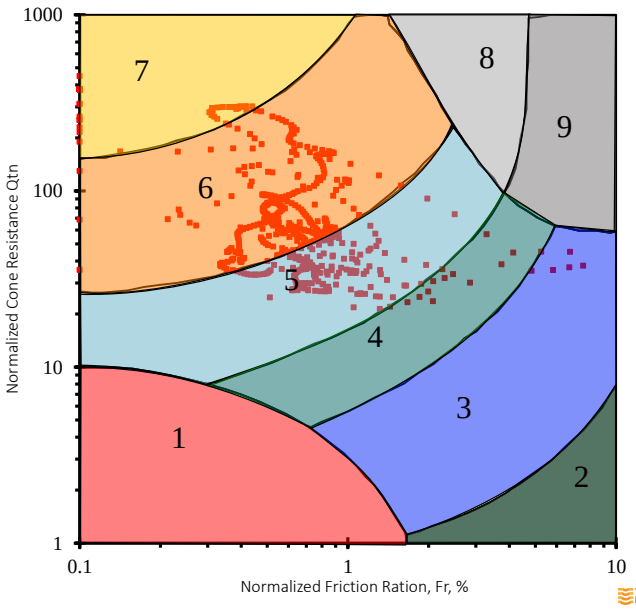

Main Contractor:	CTS GULF	
Test Location:	CPT-A1-B130-100	
Ground Elevation:	3.81	
	Easting	**Northing**
Coordinates:	420736.704	2927764.737
Cone ID:	DP15-CFPTxy.71431	
Test Date	3-Oct-2026	