
**Client : SAUDI GLOBAL PORTS**

**Project : DAMMAM LOGISTICS ZONE**

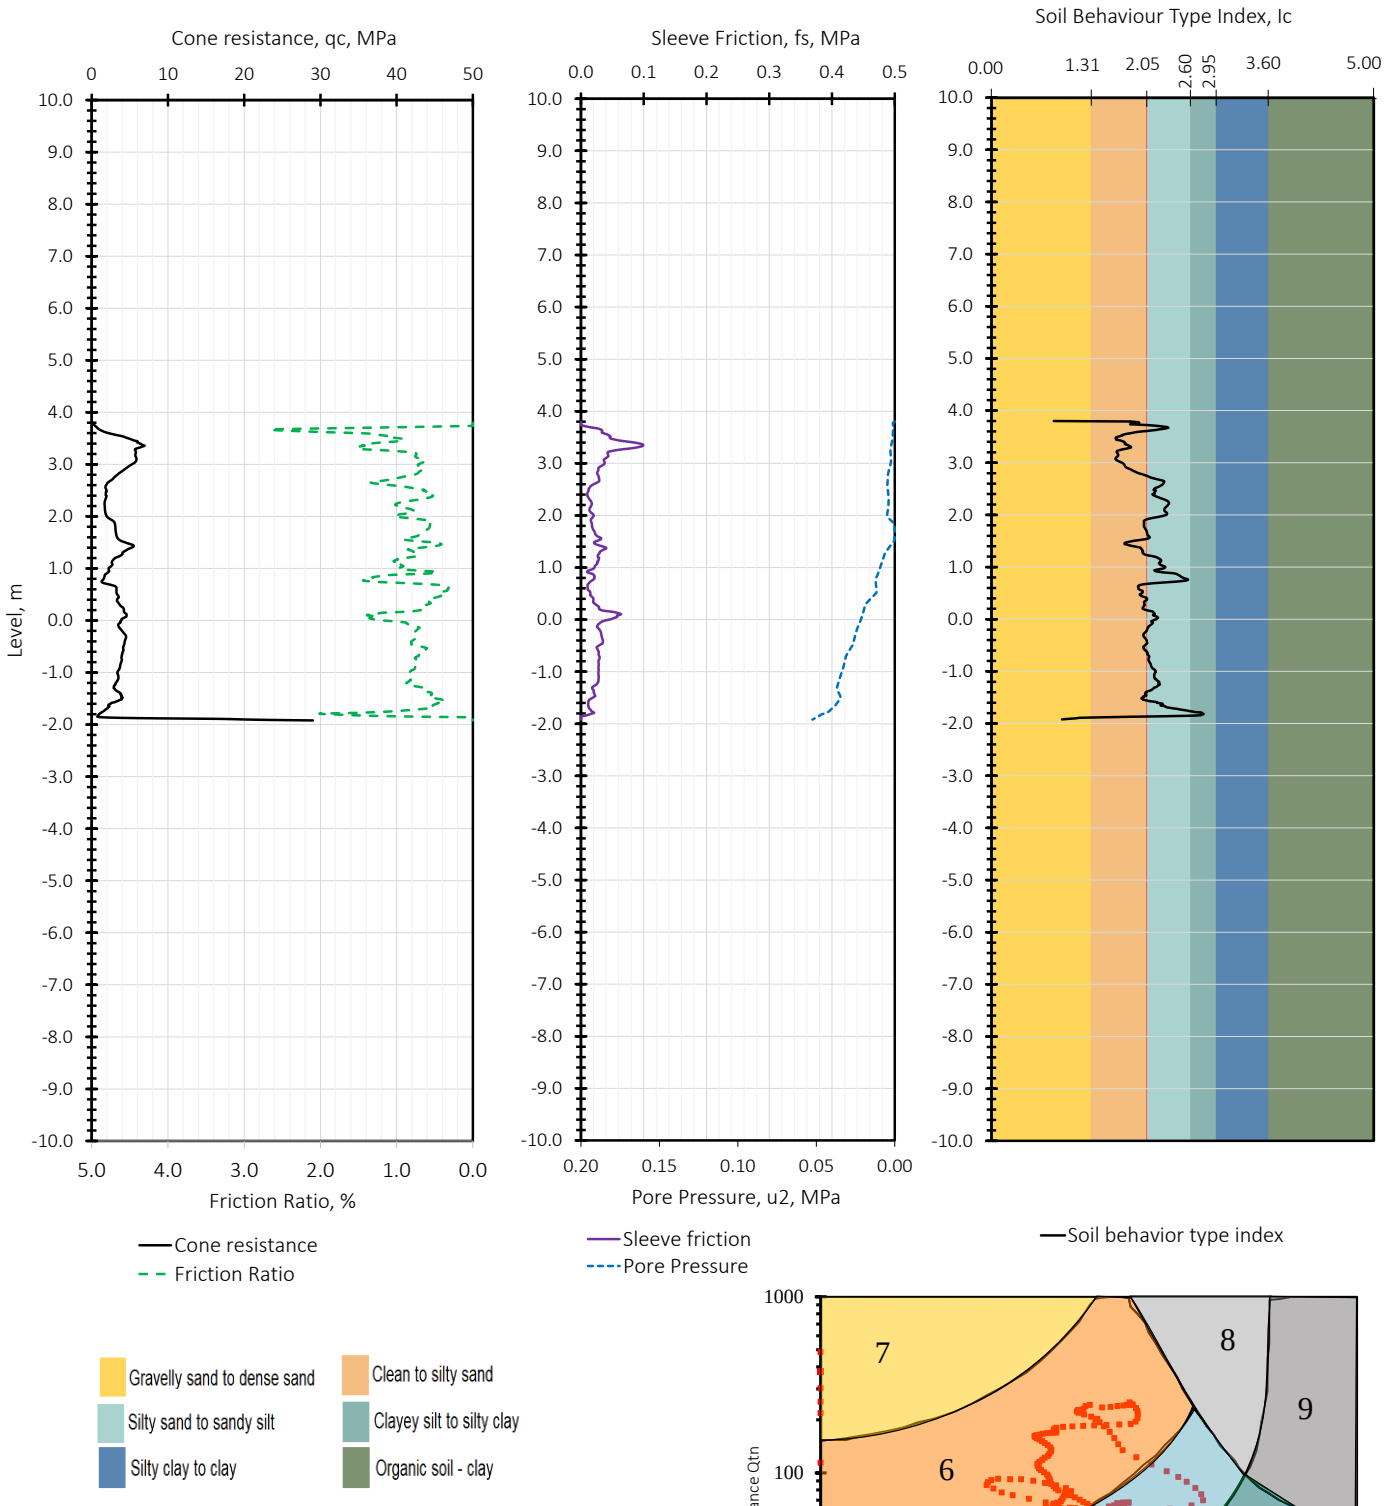


| | | |
|---|---|---|
| **Main Contractor:** | CTS GULF | |
| **Test Location:** | CPT-A1-B134-100 | |
| **Ground Elevation:** | 3.8 | |
| | **Easting** | **Northing** |
| **Coordinates:** | 420765.652 | 2927860.456 |
| **Cone ID:** | DP15-CFPTxy.71431 | |
| **Test Date** | 3-Oct-2026 | |