

Client : SAUDI GLOBAL PORTS

Project : DAMMAM LOGISTICS ZONE

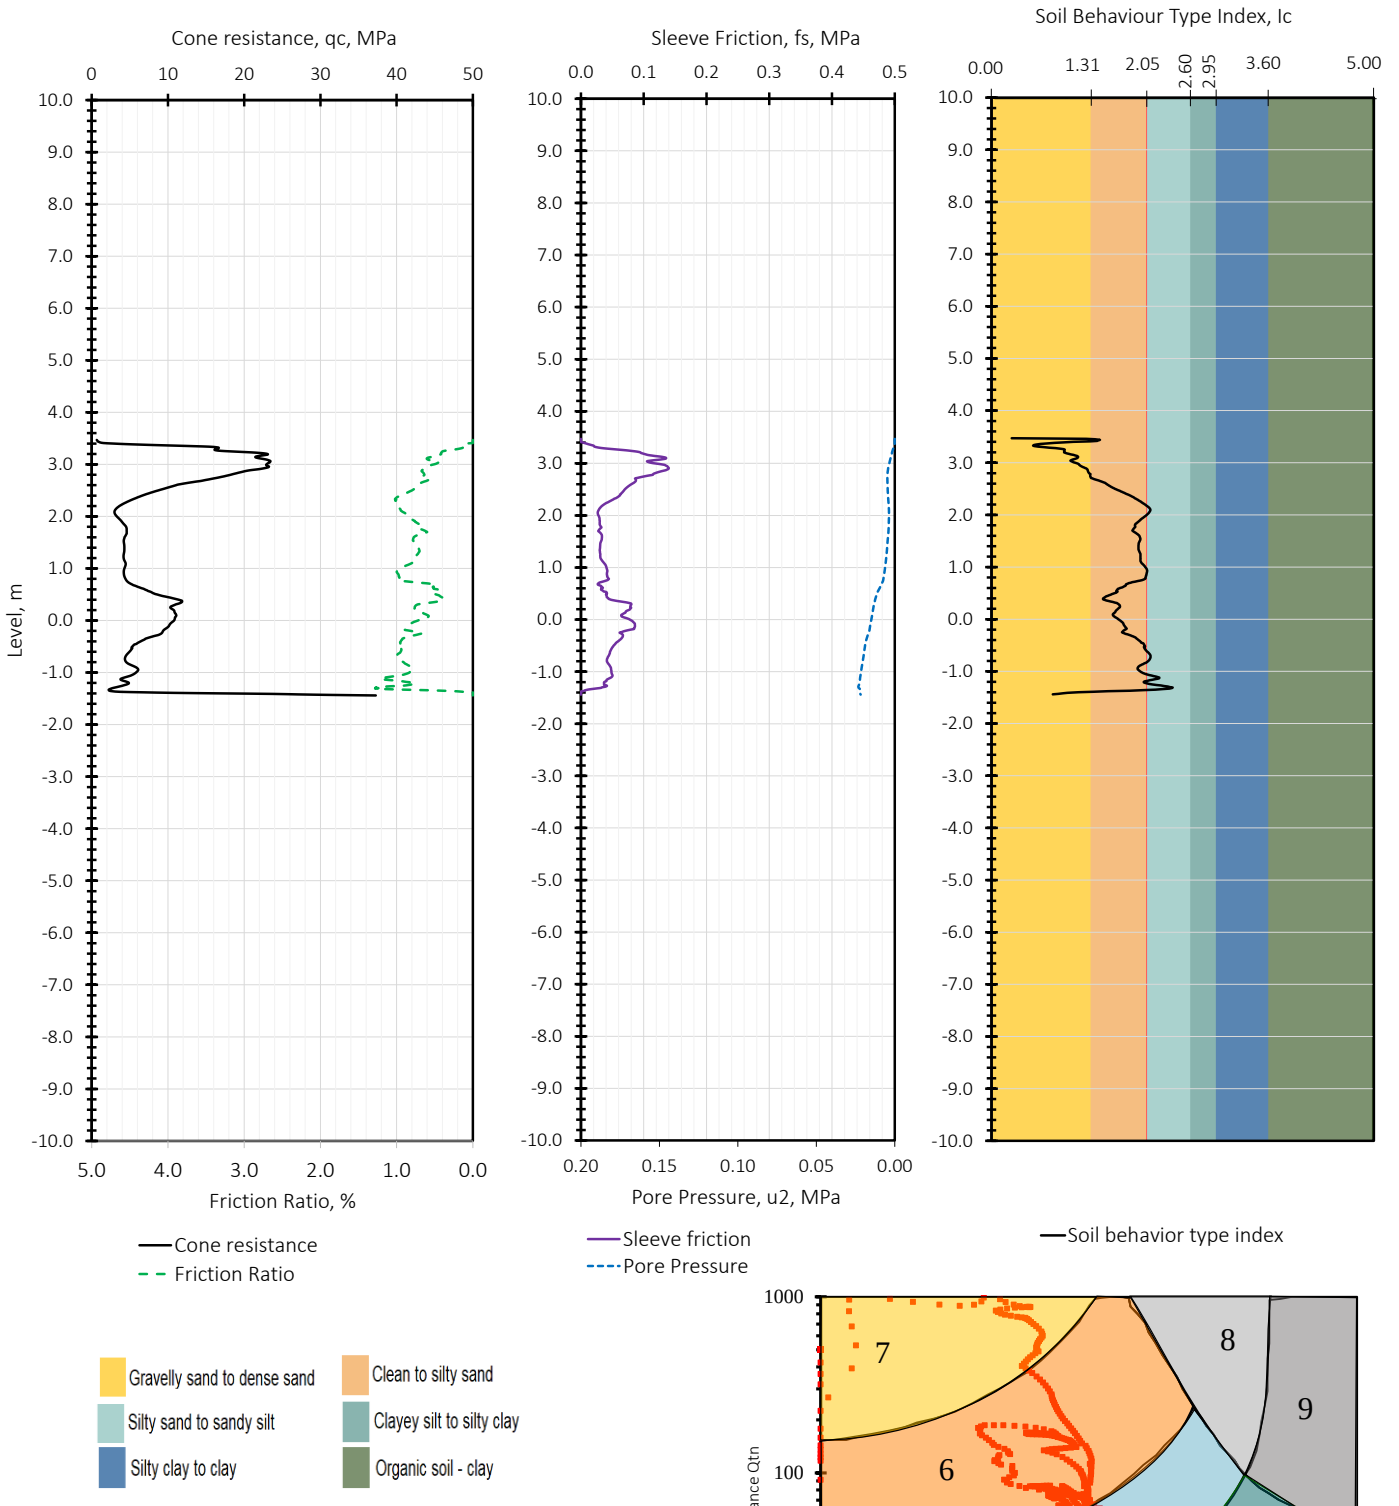

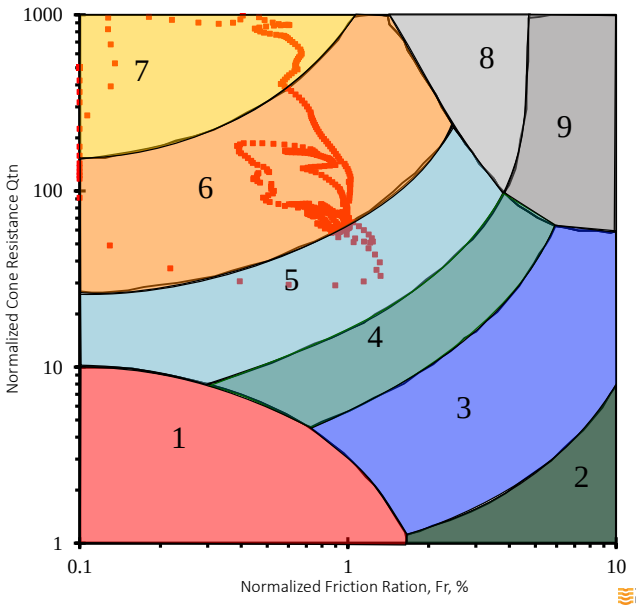

Main Contractor:	CTS GULF	
Test Location:	CPT-A1-B137-100	
Ground Elevation:	3.47	
	Easting	**Northing**
Coordinates:	420724.45	2927637.852
Cone ID:	DP15-CFPTxy.71424	
Test Date	11-Oct-2026	