
Client : SAUDI GLOBAL PORTS

Project : DAMMAM LOGISTICS ZONE

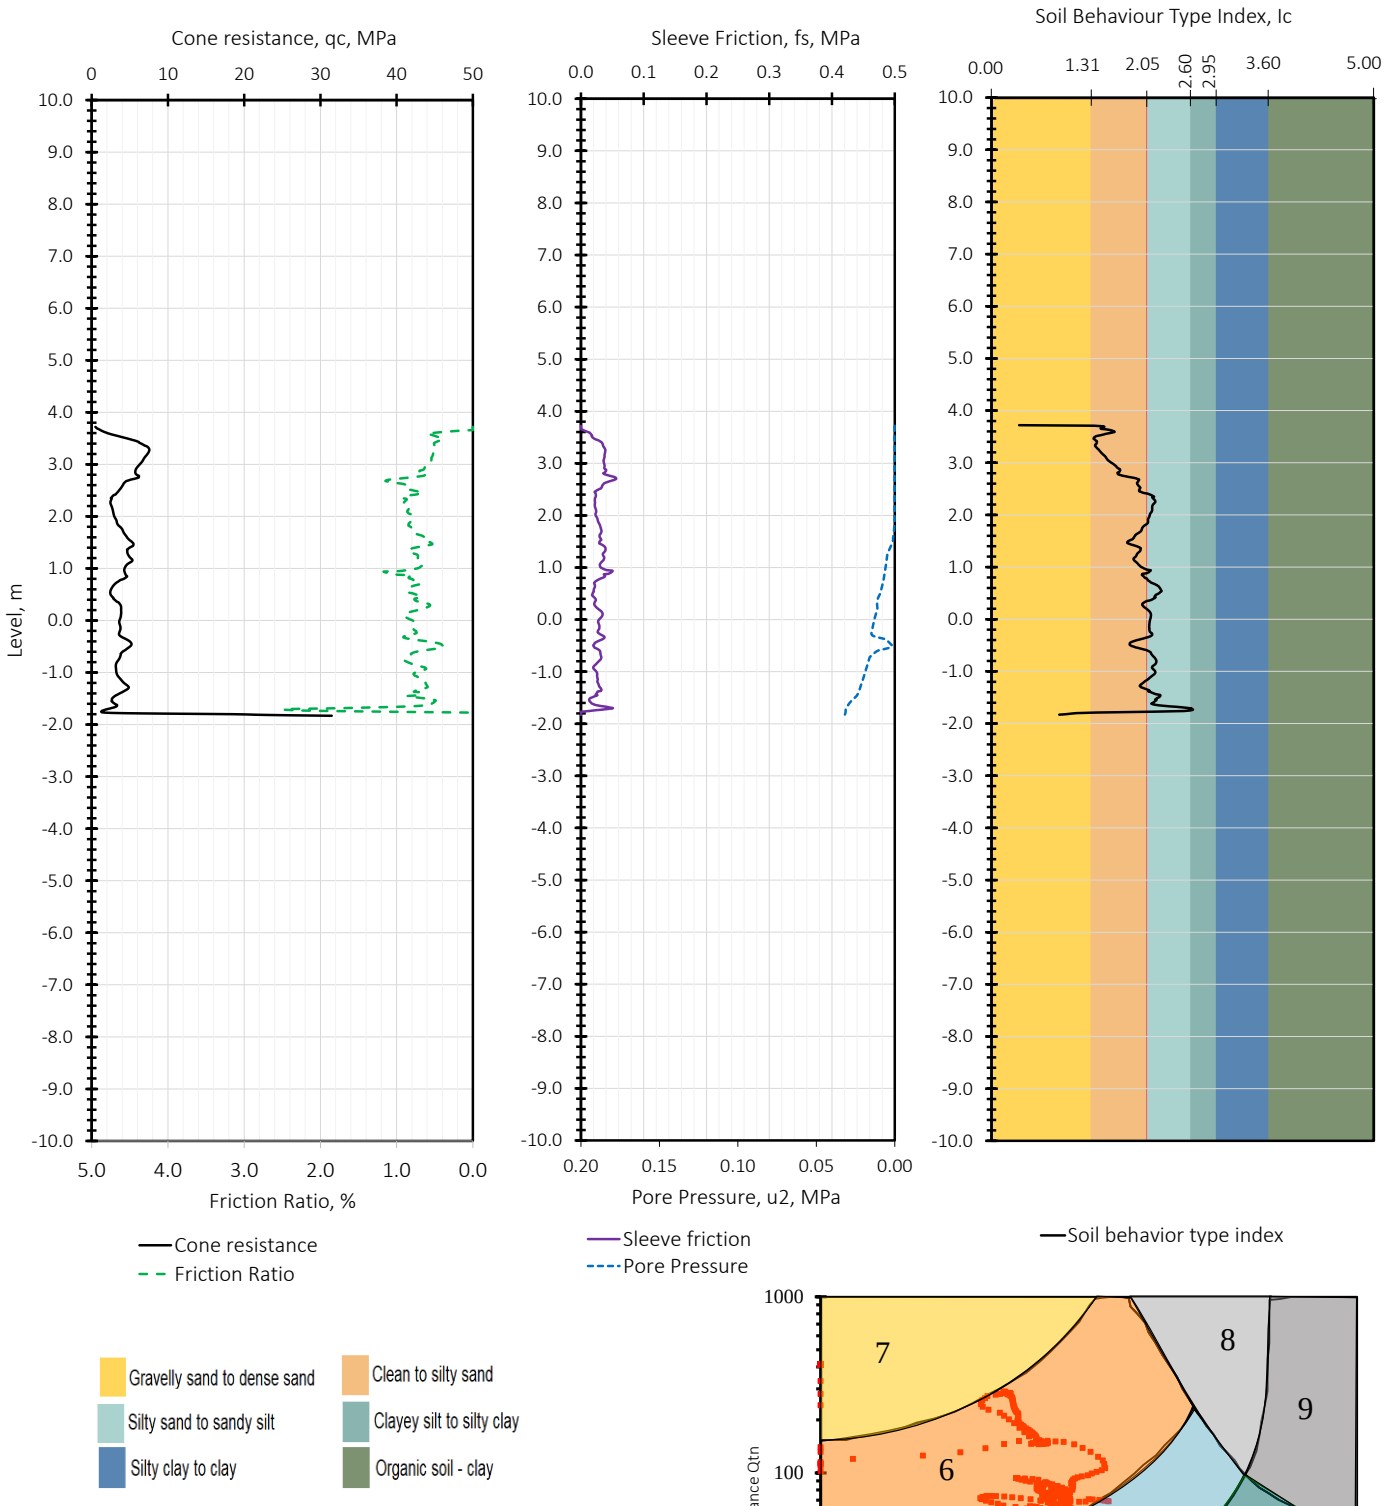

Main Contractor:	CTS GULF	
Test Location:	CPT-A1-B144-100	
Ground Elevation:	3.72	
	Easting	**Northing**
Coordinates:	420775.108	2927805.359
Cone ID:	DP15-CFPTxy.71431	
Test Date	3-Oct-2026	