
Client : SAUDI GLOBAL PORTS

Project : DAMMAM LOGISTICS ZONE

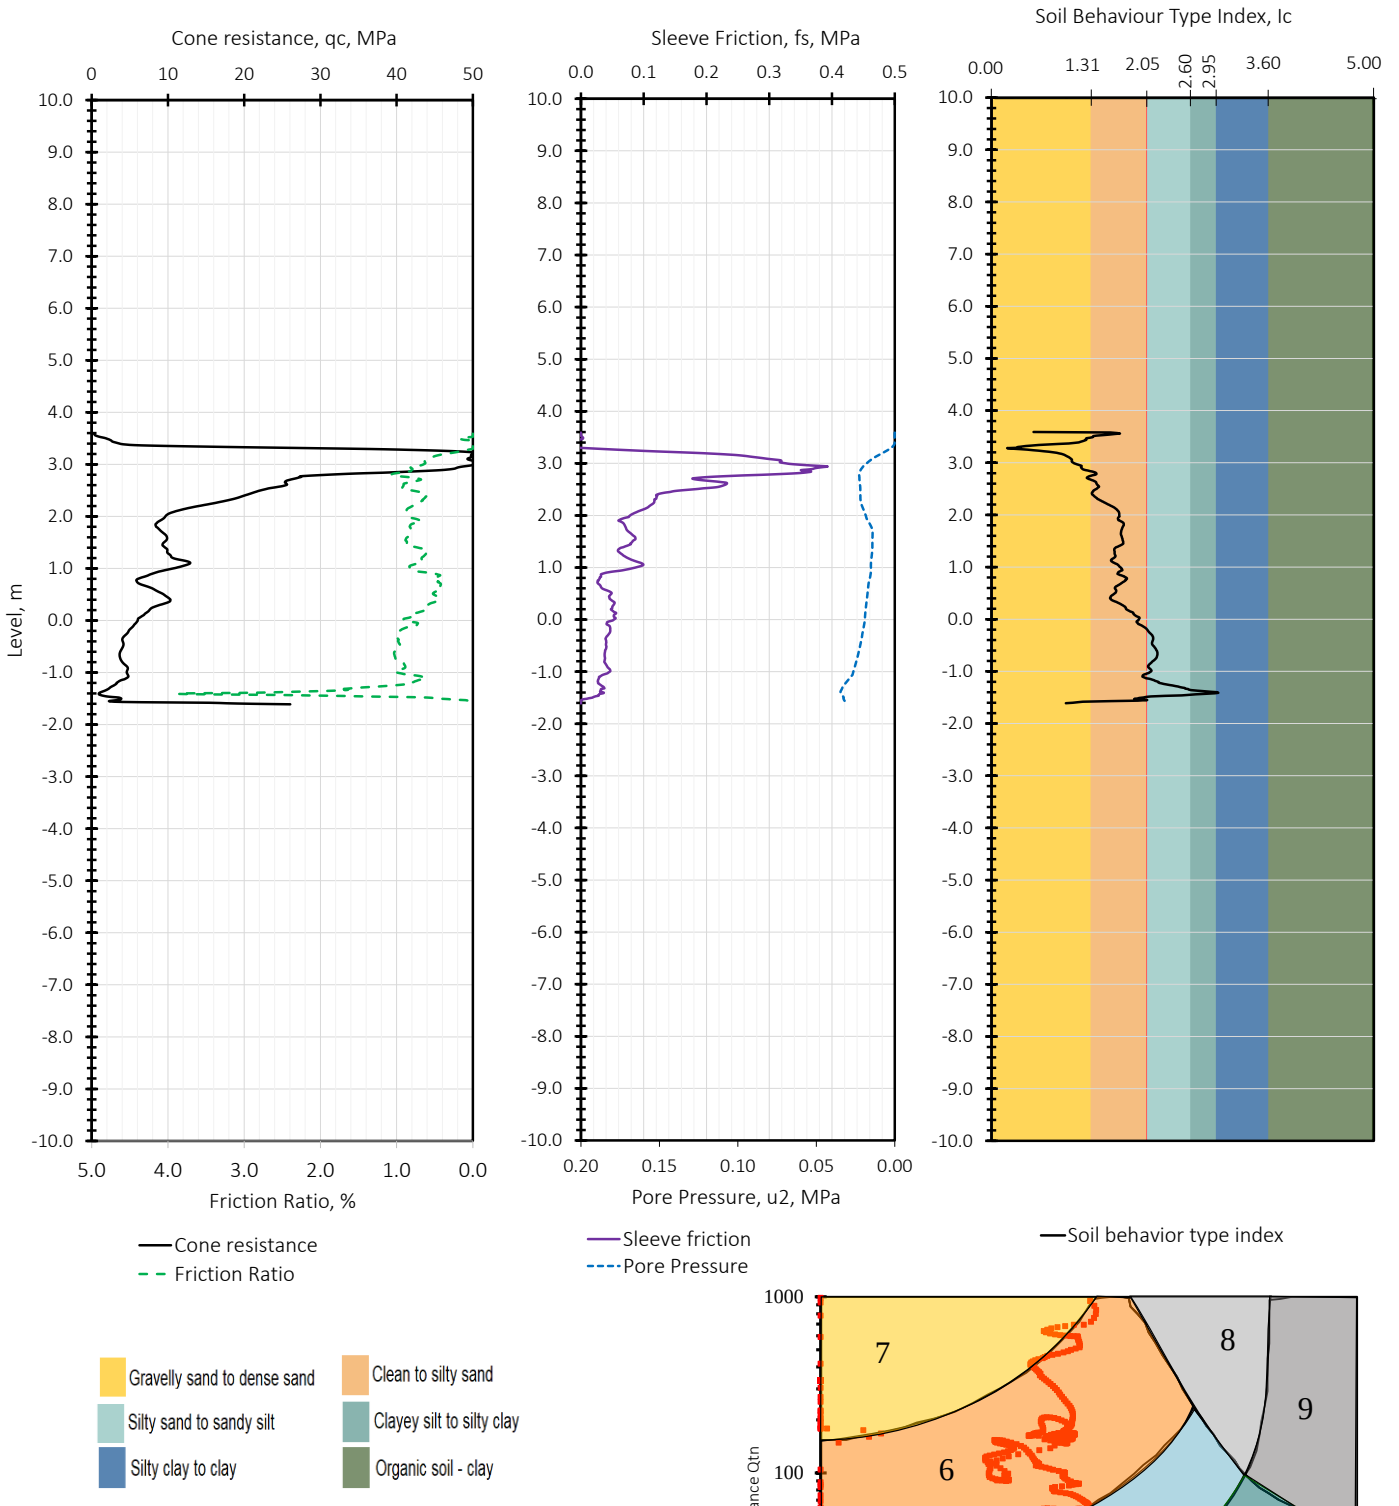

Main Contractor:	CTS GULF	
Test Location:	CPT-A1-B149-100	
Ground Elevation:	3.59	
	Easting	**Northing**
Coordinates:	420741.143	2927606.685
Cone ID:	DP15-CFPTxy.71424	
Test Date	11-Oct-2026	