
Client : SAUDI GLOBAL PORTS

Project : DAMMAM LOGISTICS ZONE

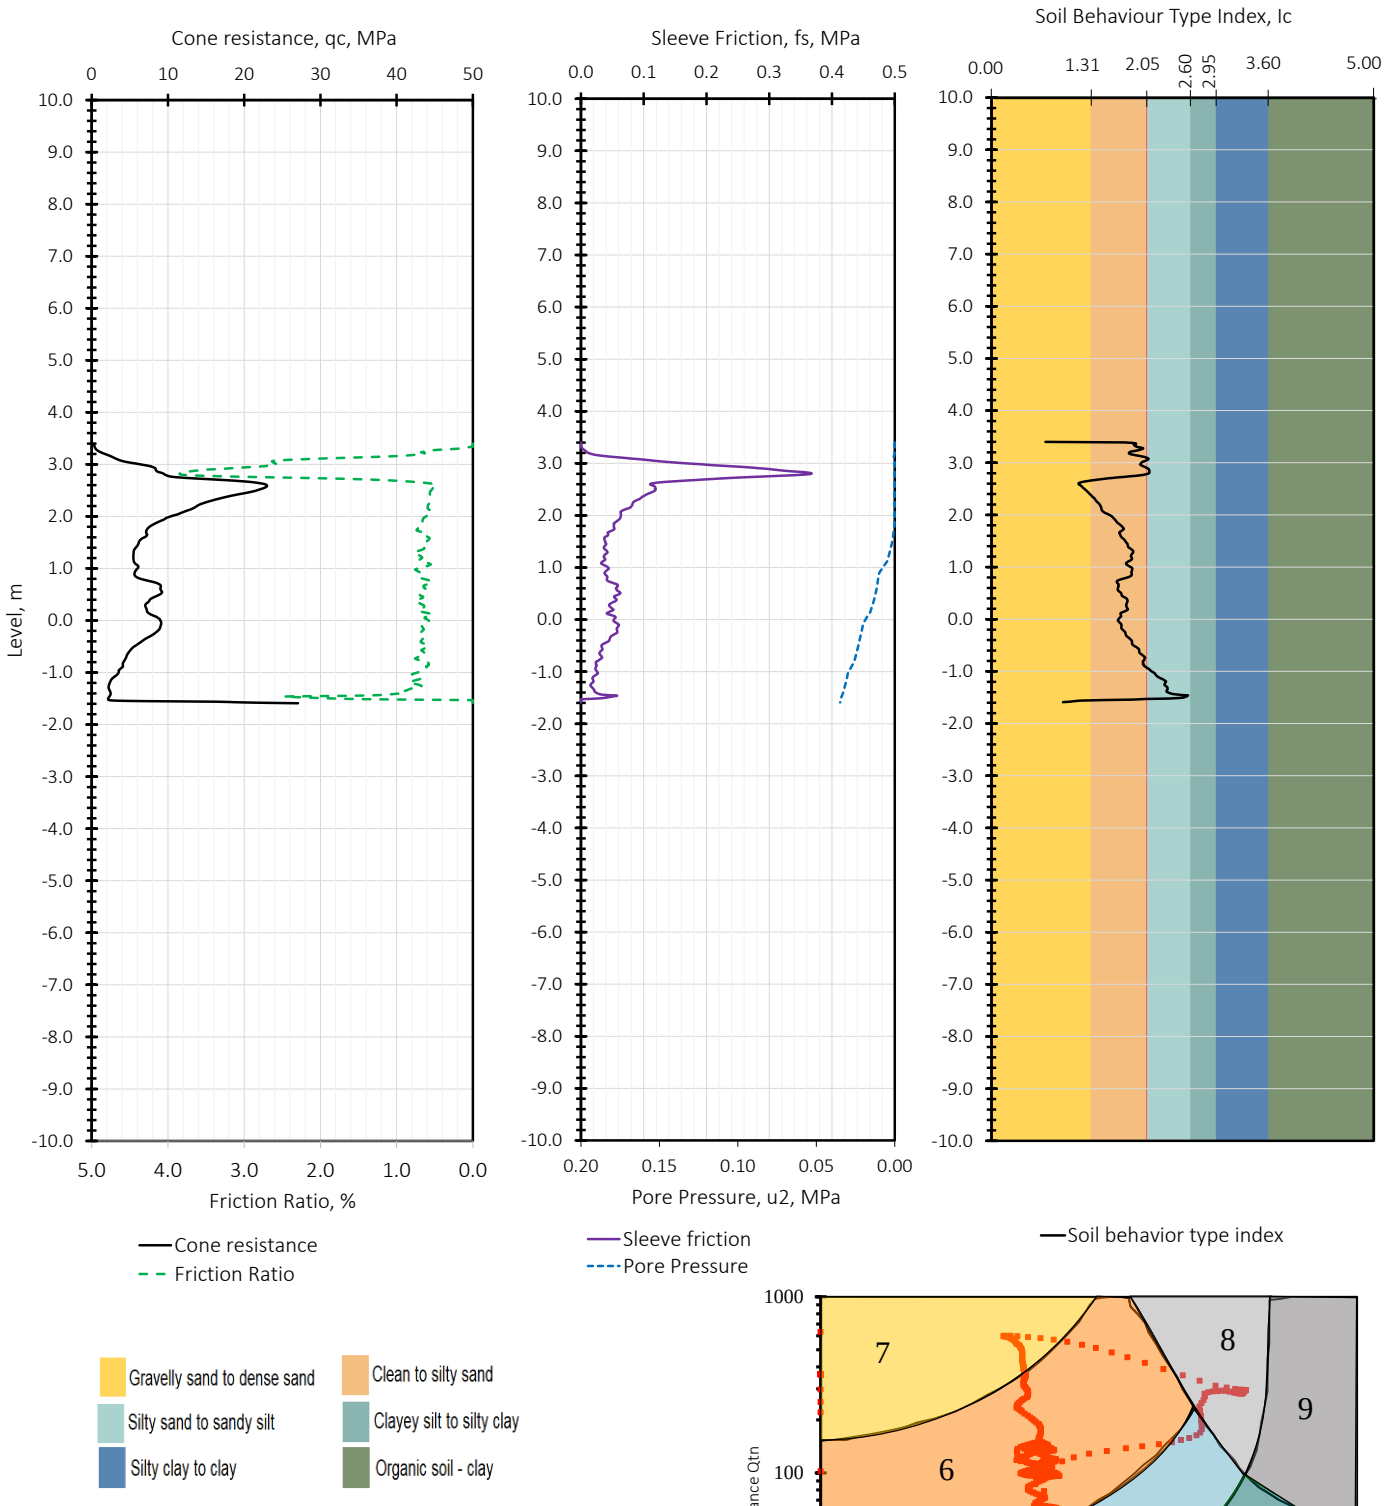

Main Contractor:	CTS GULF	
Test Location:	CPT-A1-B163-100	
Ground Elevation:	3.4	
	Easting	**Northing**
Coordinates:	420779.546	2927647.308
Cone ID:	DP15-CFPTxy.71431	
Test Date	11-Oct-2026	