
Client : SAUDI GLOBAL PORTS

Project : DAMMAM LOGISTICS ZONE

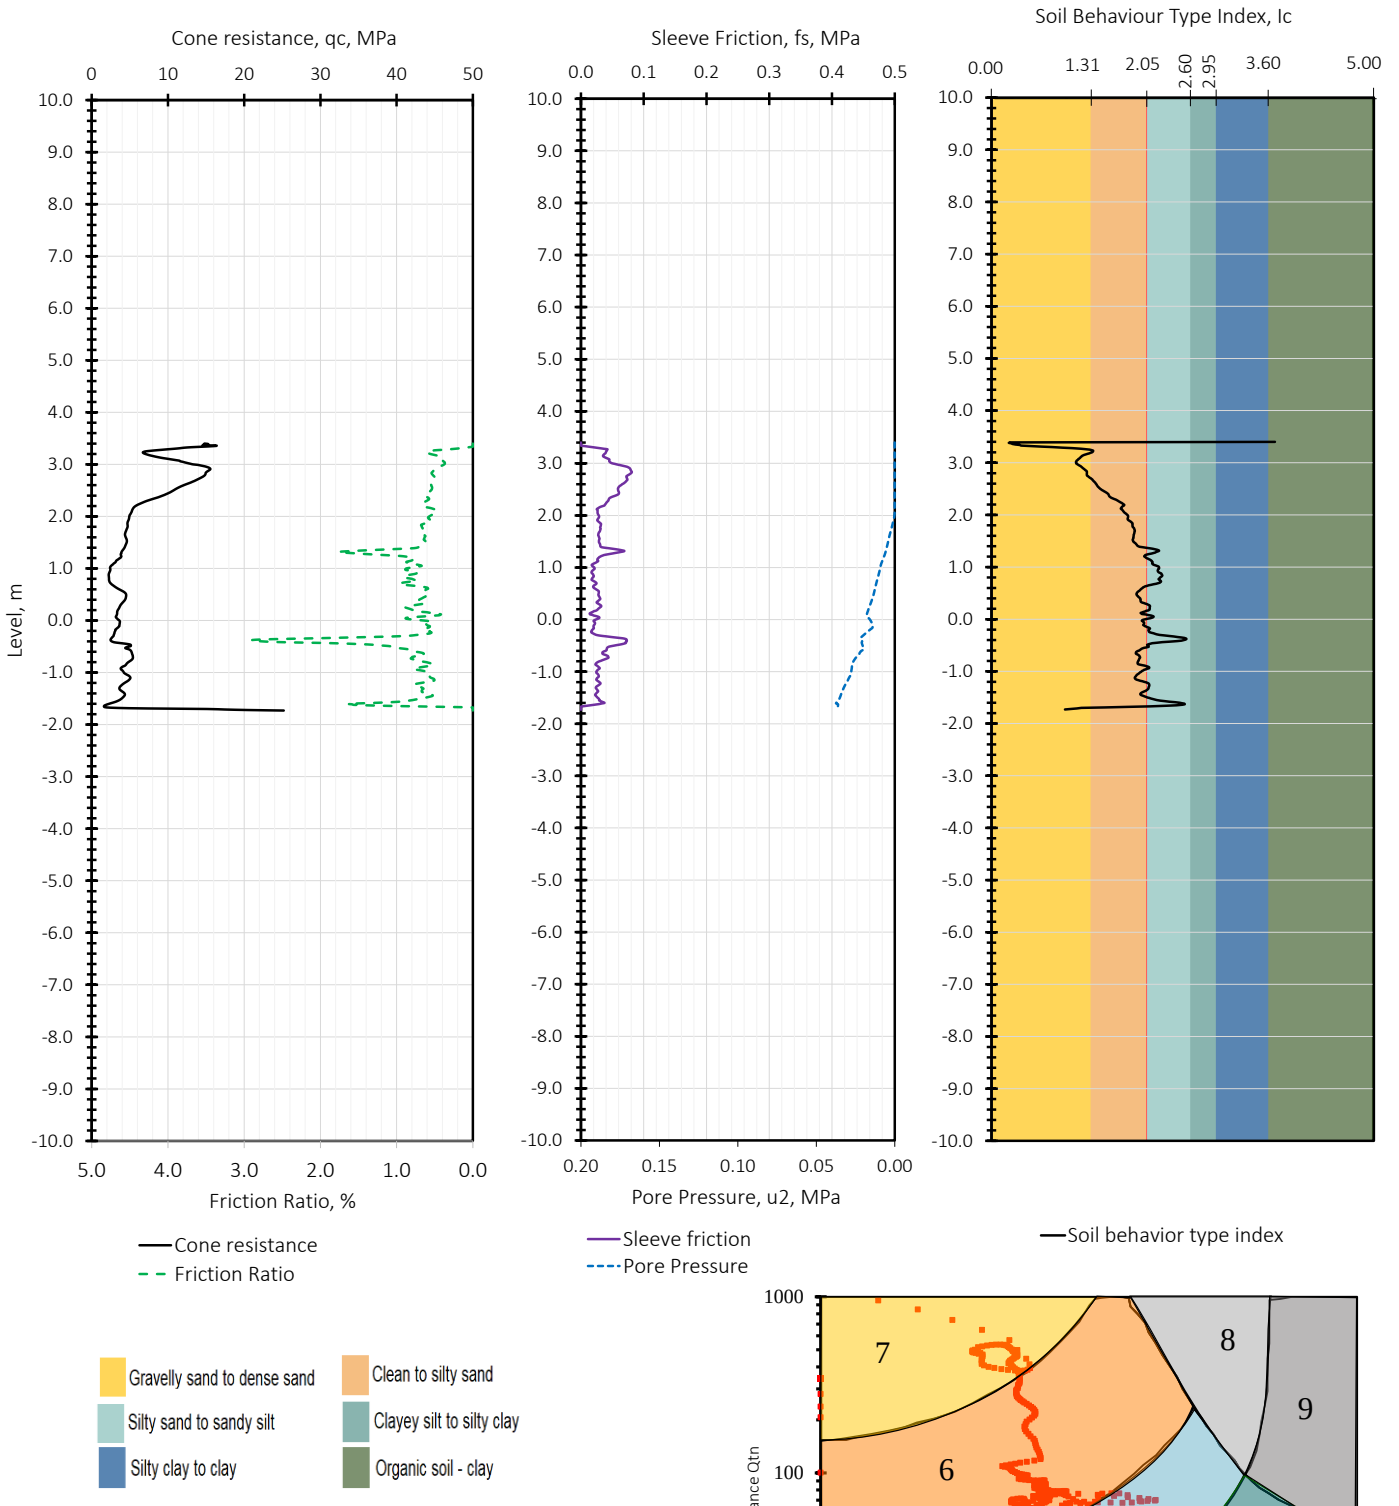

Main Contractor:	CTS GULF	
Test Location:	CPT-A1-B165-100	
Ground Elevation:	3.4	
	Easting	**Northing**
Coordinates:	420794.02	2927695.167
Cone ID:	DP15-CFPTxy.71431	
Test Date	11-Oct-2026	