
Client : SAUDI GLOBAL PORTS

Project : DAMMAM LOGISTICS ZONE

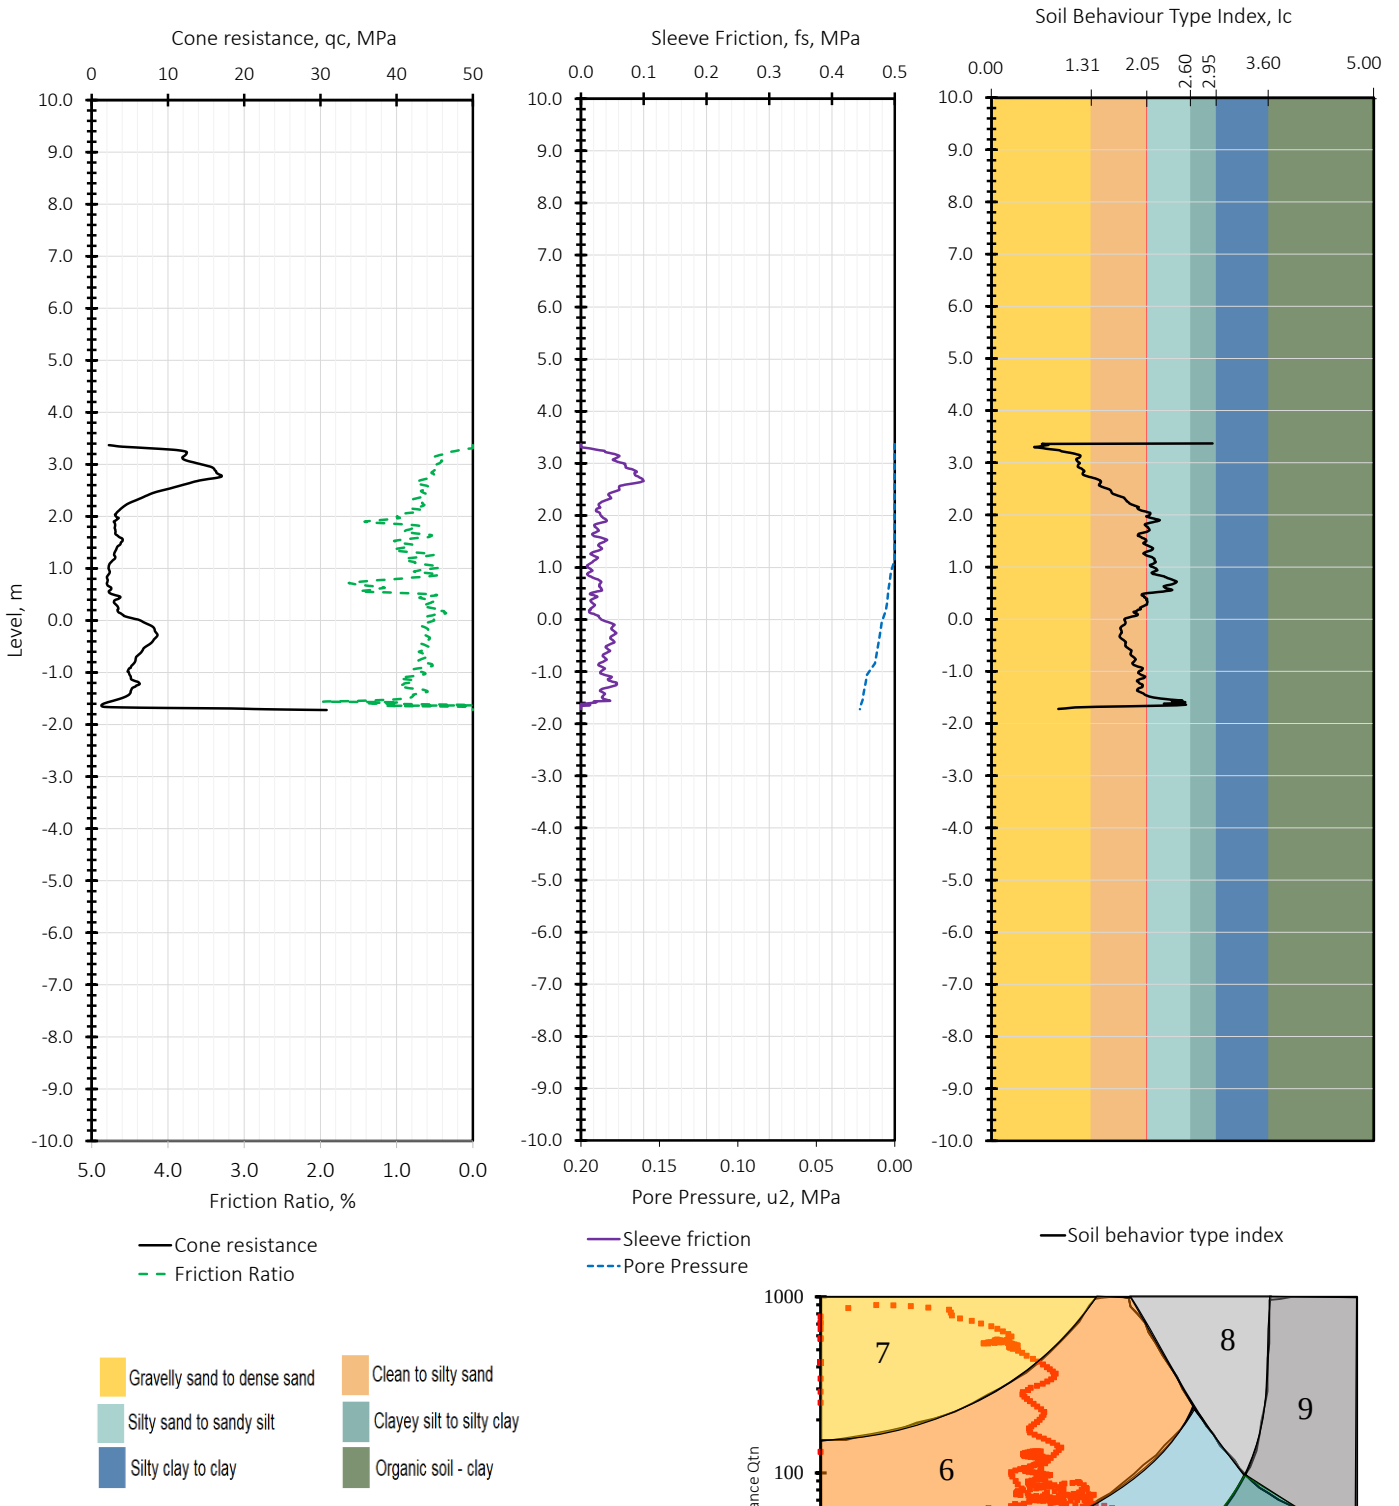

Main Contractor:	CTS GULF	
Test Location:	CPT-A1-B166-100	
Ground Elevation:	3.37	
	Easting	**Northing**
Coordinates:	421174.675	2927658.404
Cone ID:	DP15-CFPTxy.71431	
Test Date	10-Oct-2026	