
Client : SAUDI GLOBAL PORTS

Project : DAMMAM LOGISTICS ZONE

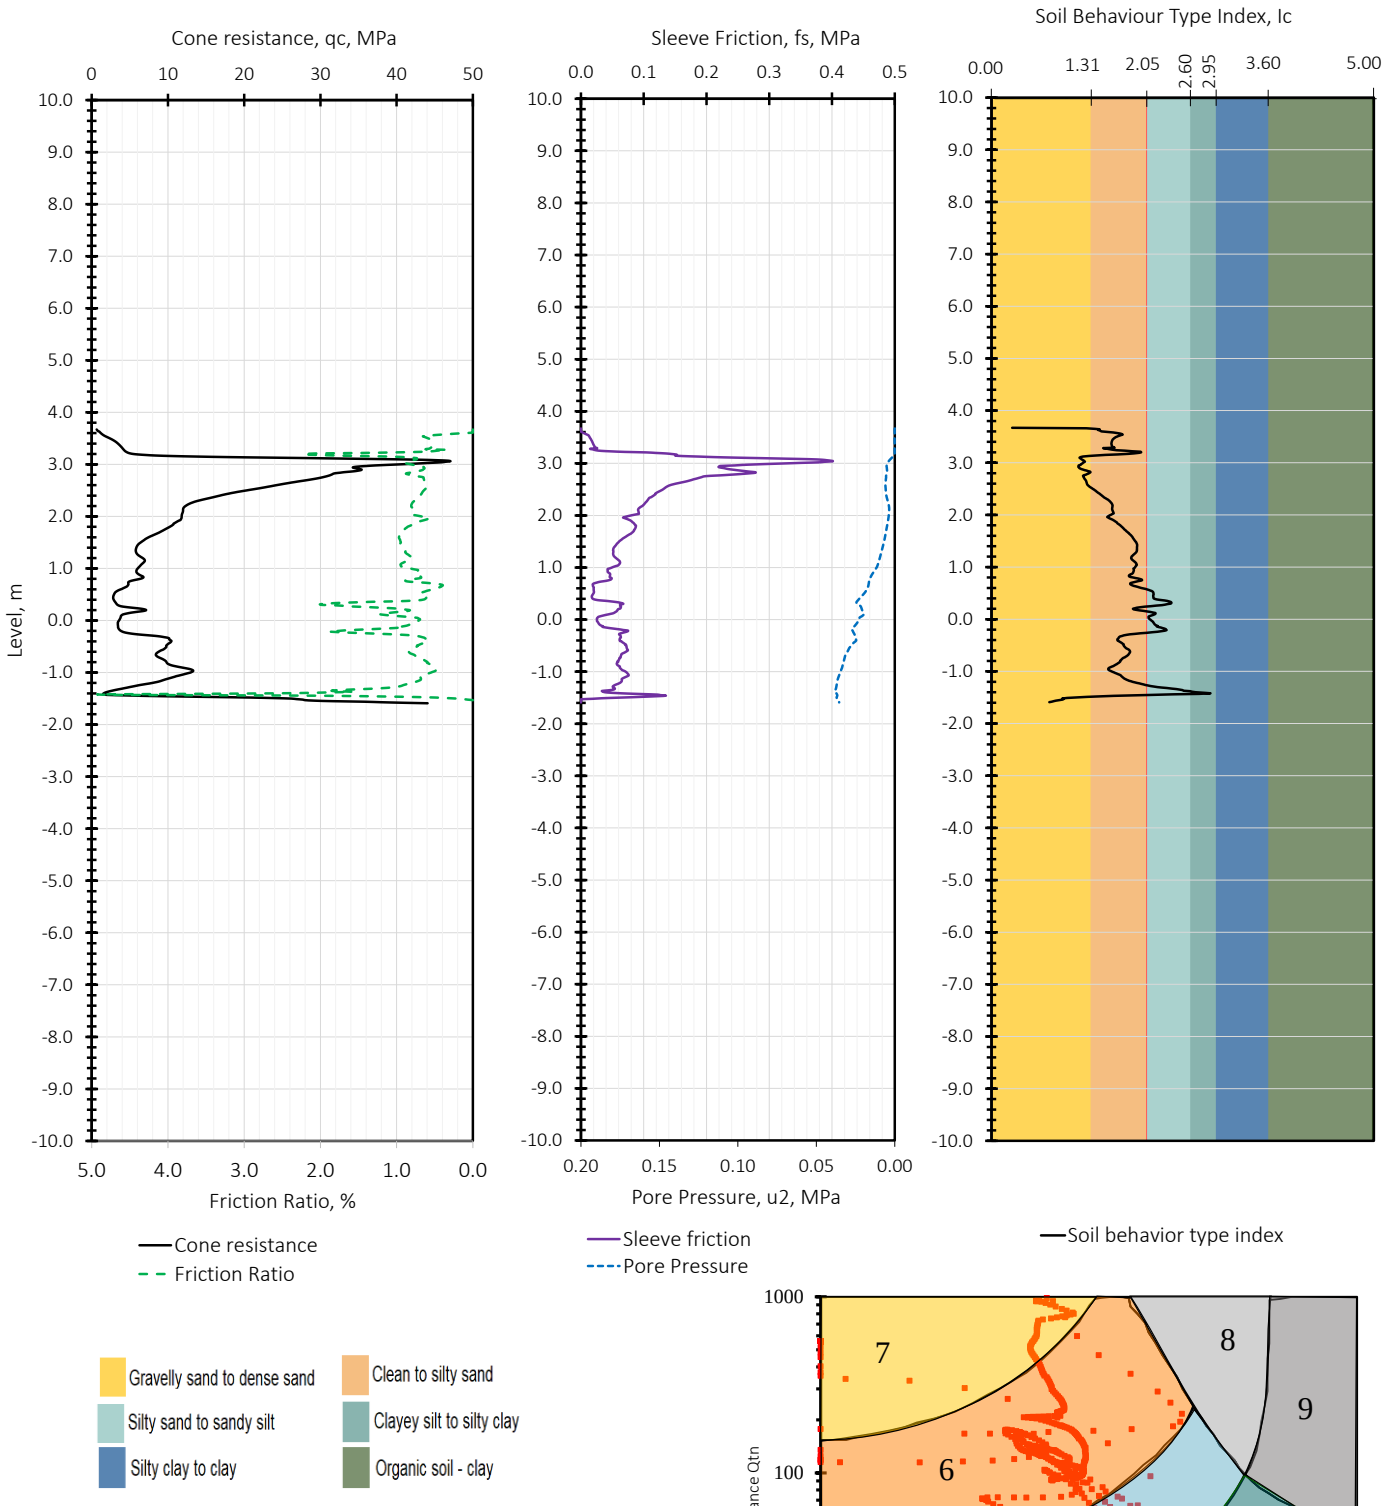

Main Contractor:	CTS GULF	
Test Location:	CPT-A1-B173-100	
Ground Elevation:	3.67	
	Easting	**Northing**
Coordinates:	420781.678	2927567.993
Cone ID:	DP15-CFPTxy.71424	
Test Date	12-Oct-2026	