
Client : SAUDI GLOBAL PORTS

Project : DAMMAM LOGISTICS ZONE

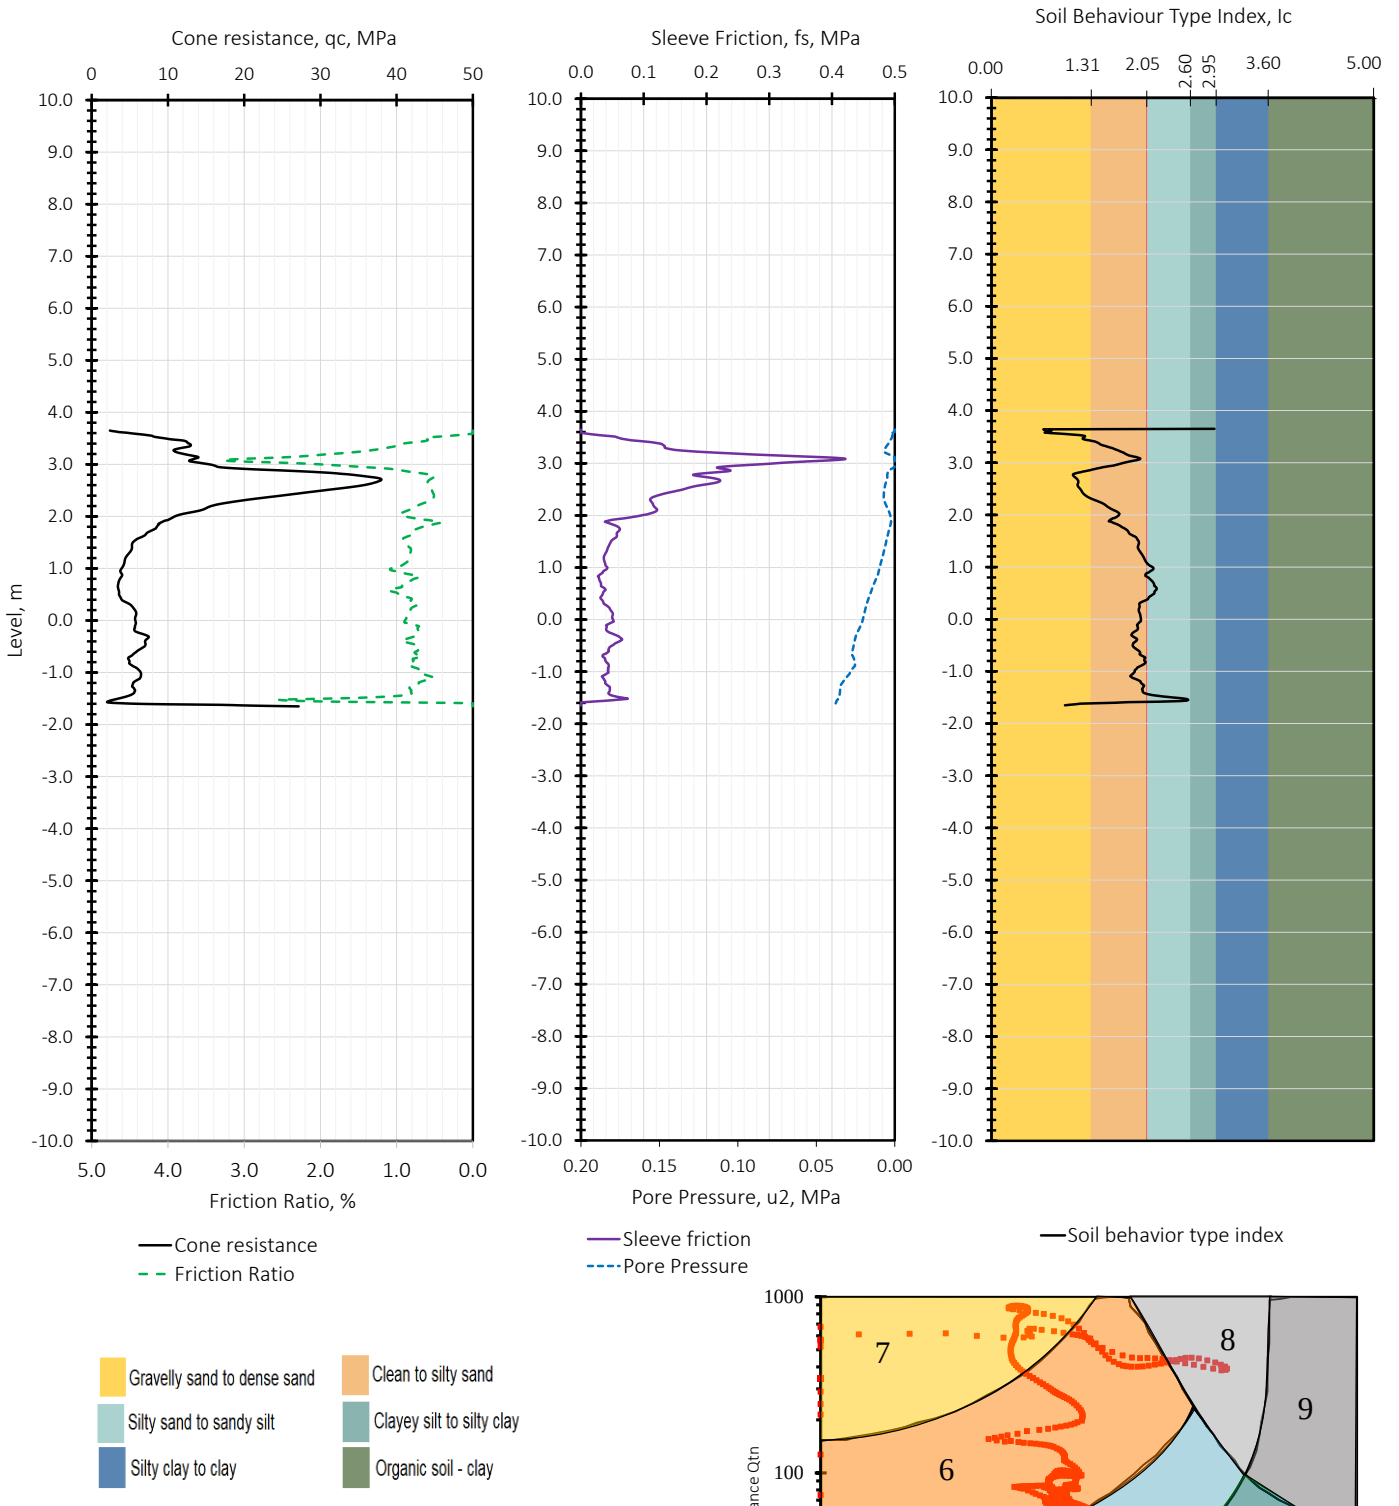

Main Contractor:	CTS GULF	
Test Location:	CPT-A1-B174-100	
Ground Elevation:	3.65	
	Easting	**Northing**
Coordinates:	420789.002	2927592.212
Cone ID:	DP15-CFPTxy.71424	
Test Date	12-Oct-2026	