
Client : SAUDI GLOBAL PORTS

Project : DAMMAM LOGISTICS ZONE

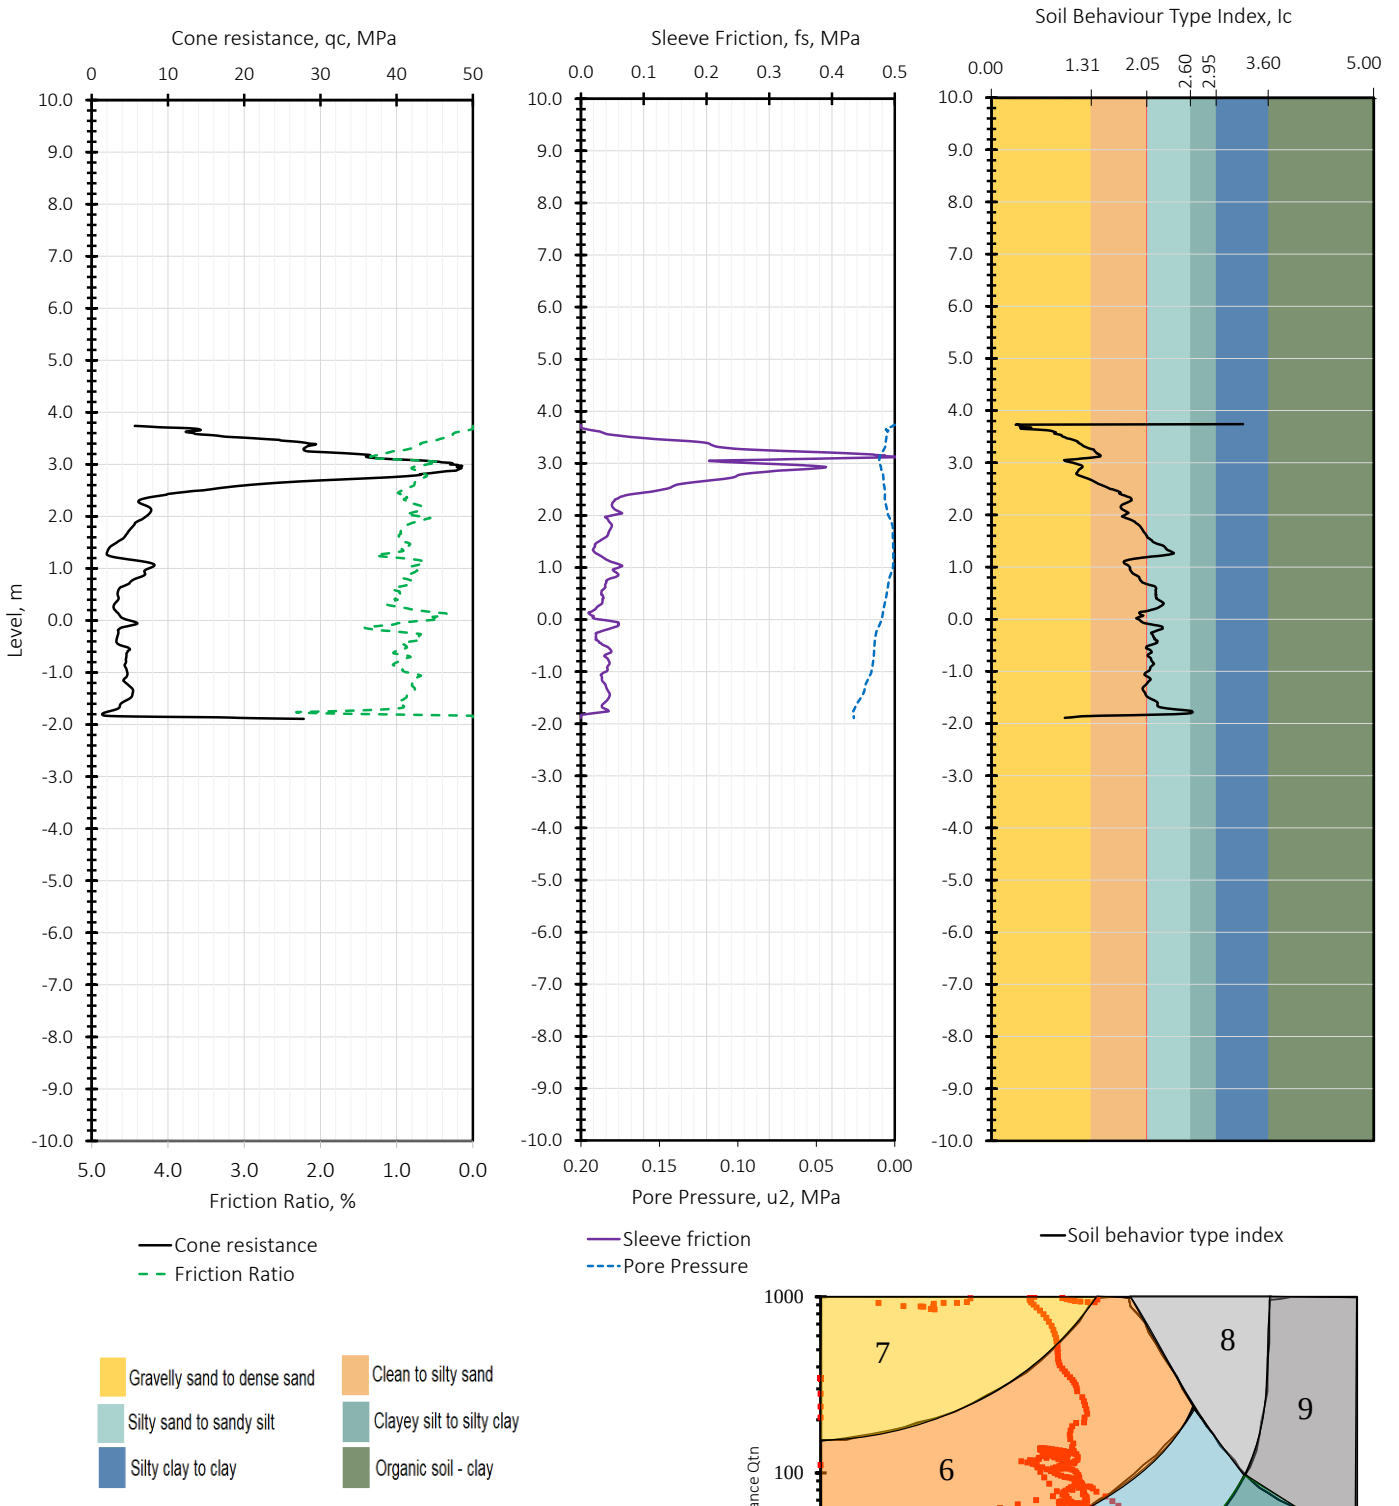

Main Contractor:	CTS GULF	
Test Location:	CPT-A1-B183-100	
Ground Elevation:	3.74	
	Easting	**Northing**
Coordinates:	420854.133	2927807.579
Cone ID:	DP15-CFPTxy.71424	
Test Date	12-Oct-2026	