
Client : SAUDI GLOBAL PORTS

Project : DAMMAM LOGISTICS ZONE

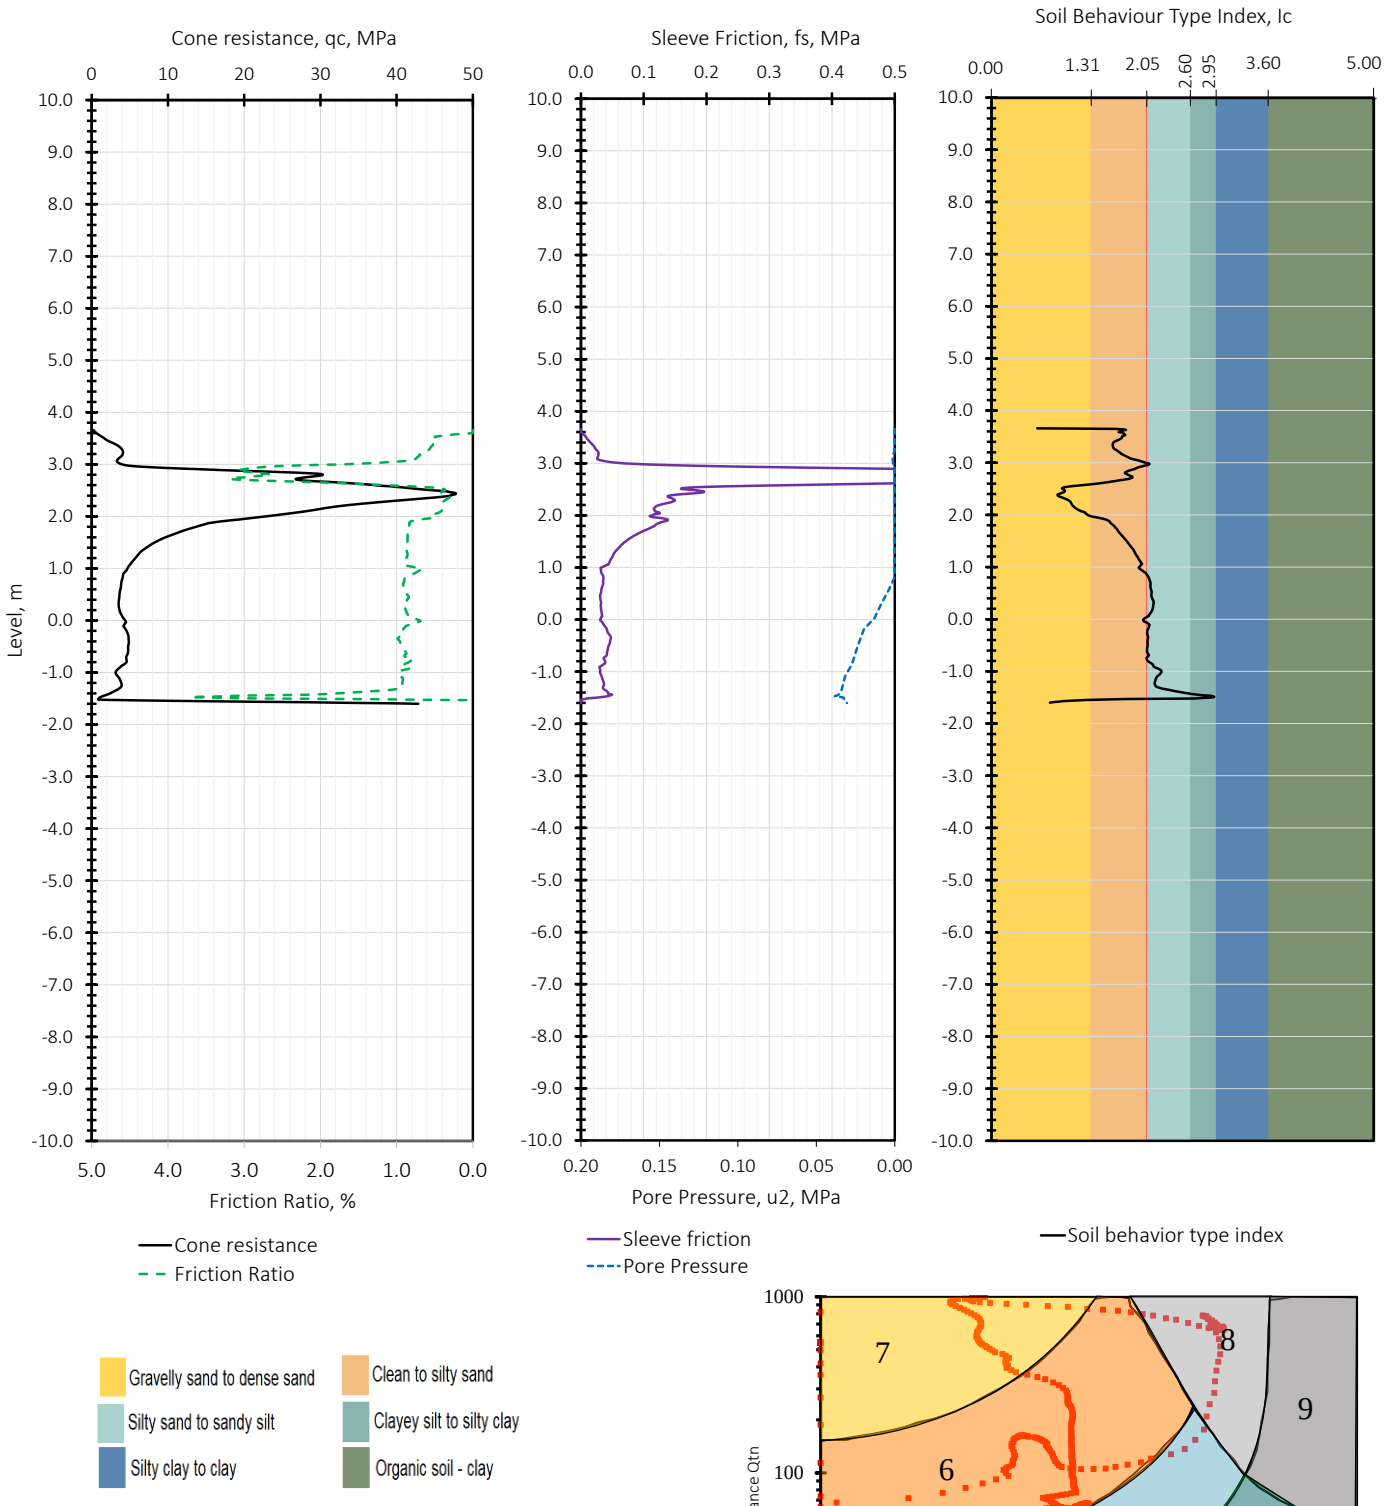

Main Contractor:	CTS GULF	
Test Location:	CPT-A1-B211-100	
Ground Elevation:	3.66	
	Easting	**Northing**
Coordinates:	420812.932	2927584.975
Cone ID:	DP15-CFPTxy.71424	
Test Date	12-Oct-2026	