
Client : SAUDI GLOBAL PORTS

Project : DAMMAM LOGISTICS ZONE

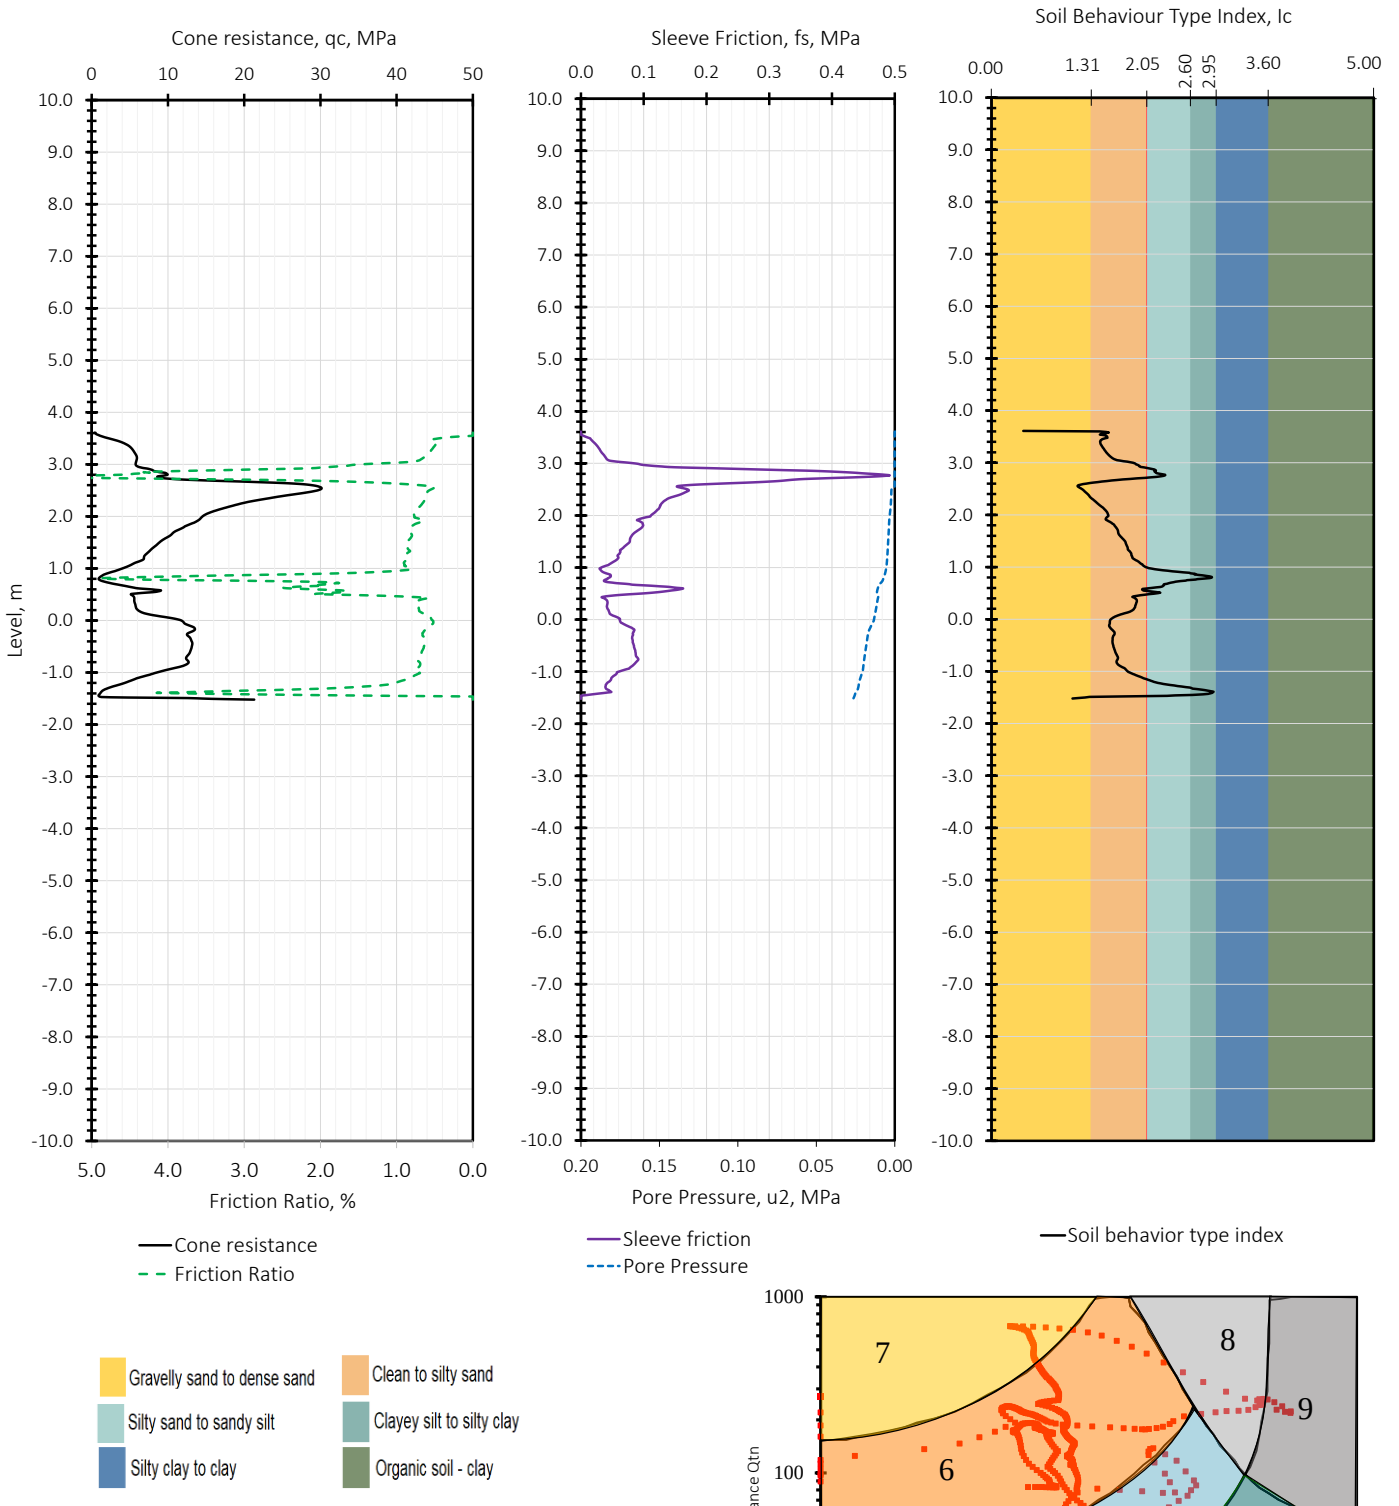

Main Contractor:	CTS GULF	
Test Location:	CPT-A1-B213-100	
Ground Elevation:	3.61	
	Easting	**Northing**
Coordinates:	420827.405	2927632.834
Cone ID:	DP15-CFPTxy.71424	
Test Date	12-Oct-2026	