
Client : SAUDI GLOBAL PORTS

Project : DAMMAM LOGISTICS ZONE

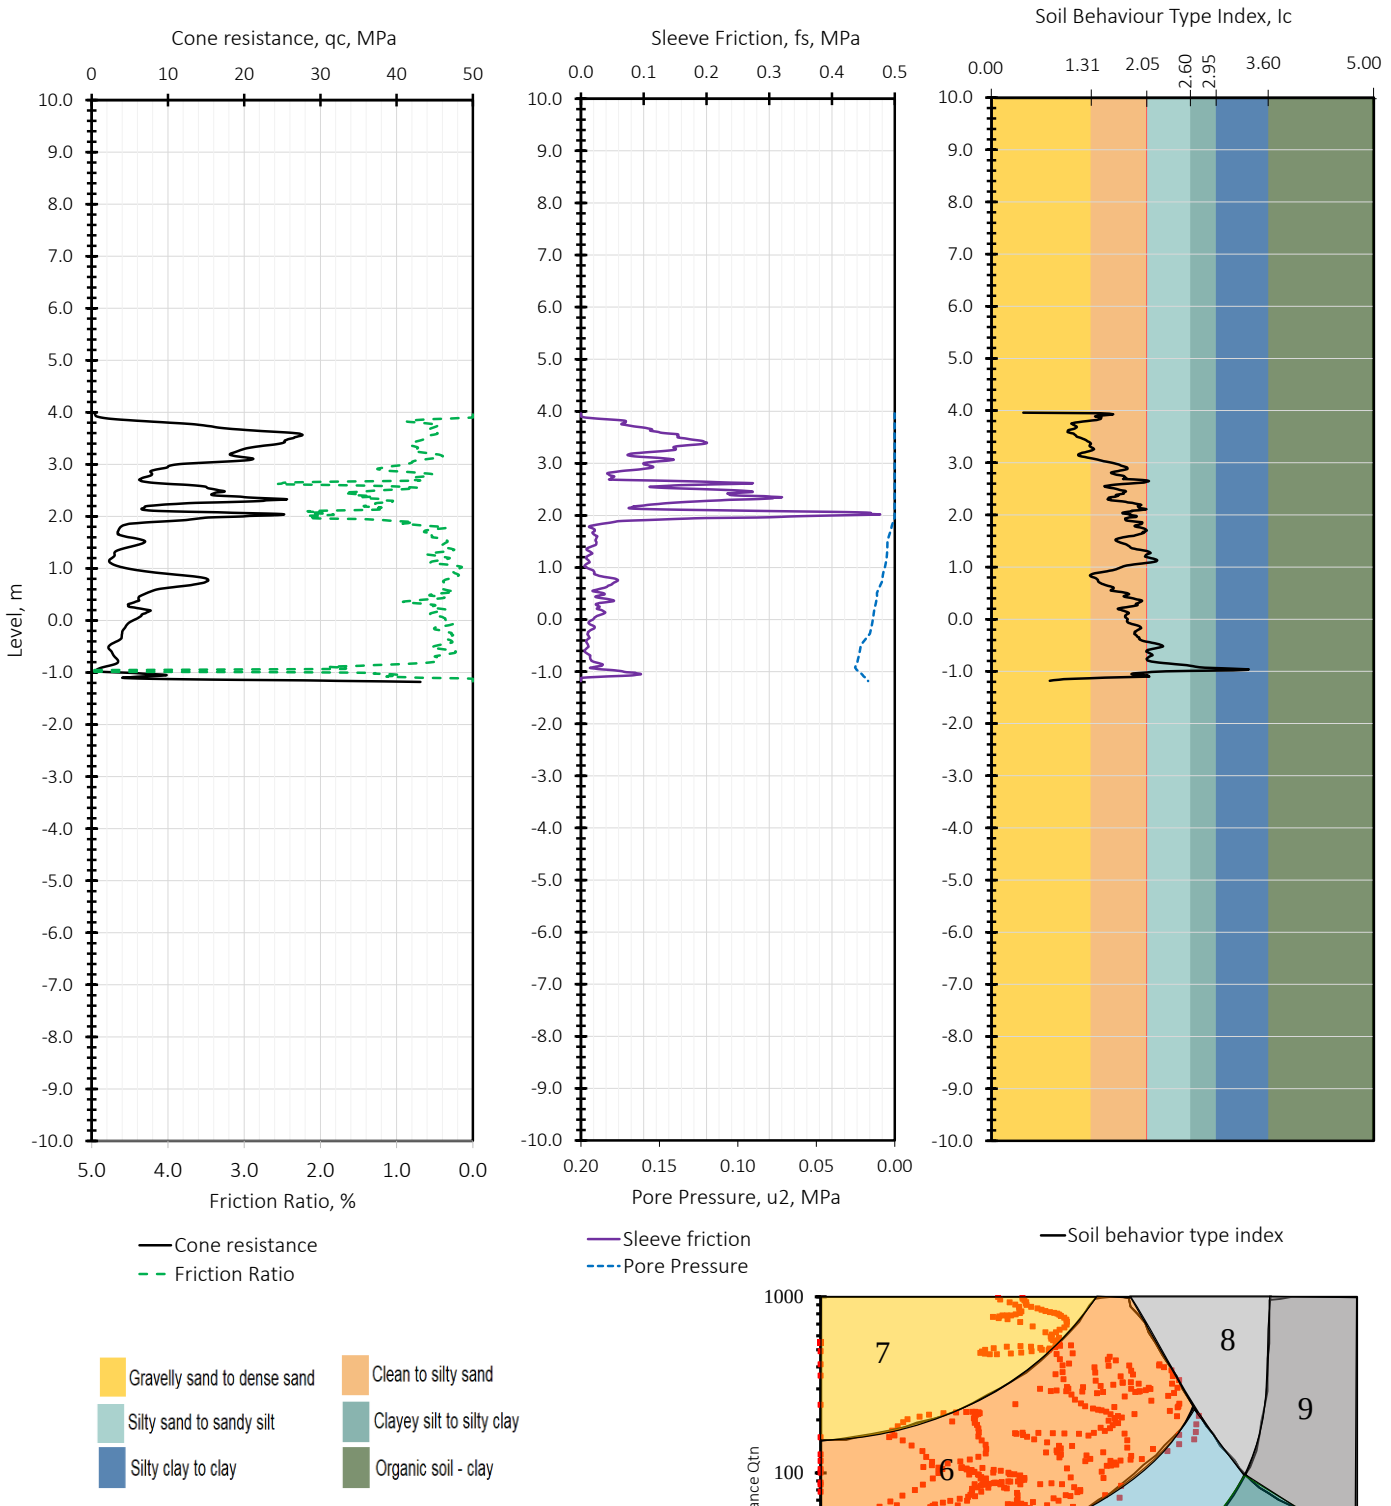

Main Contractor:	CTS GULF	
Test Location:	CPT-A1-B22-100	
Ground Elevation:	3.96	
	Easting	**Northing**
Coordinates:	420539.92	2927888.135
Cone ID:	DP15-CFPTxy.71431	
Test Date	10-Oct-2026	