

Client : SAUDI GLOBAL PORTS

Project : DAMMAM LOGISTICS ZONE

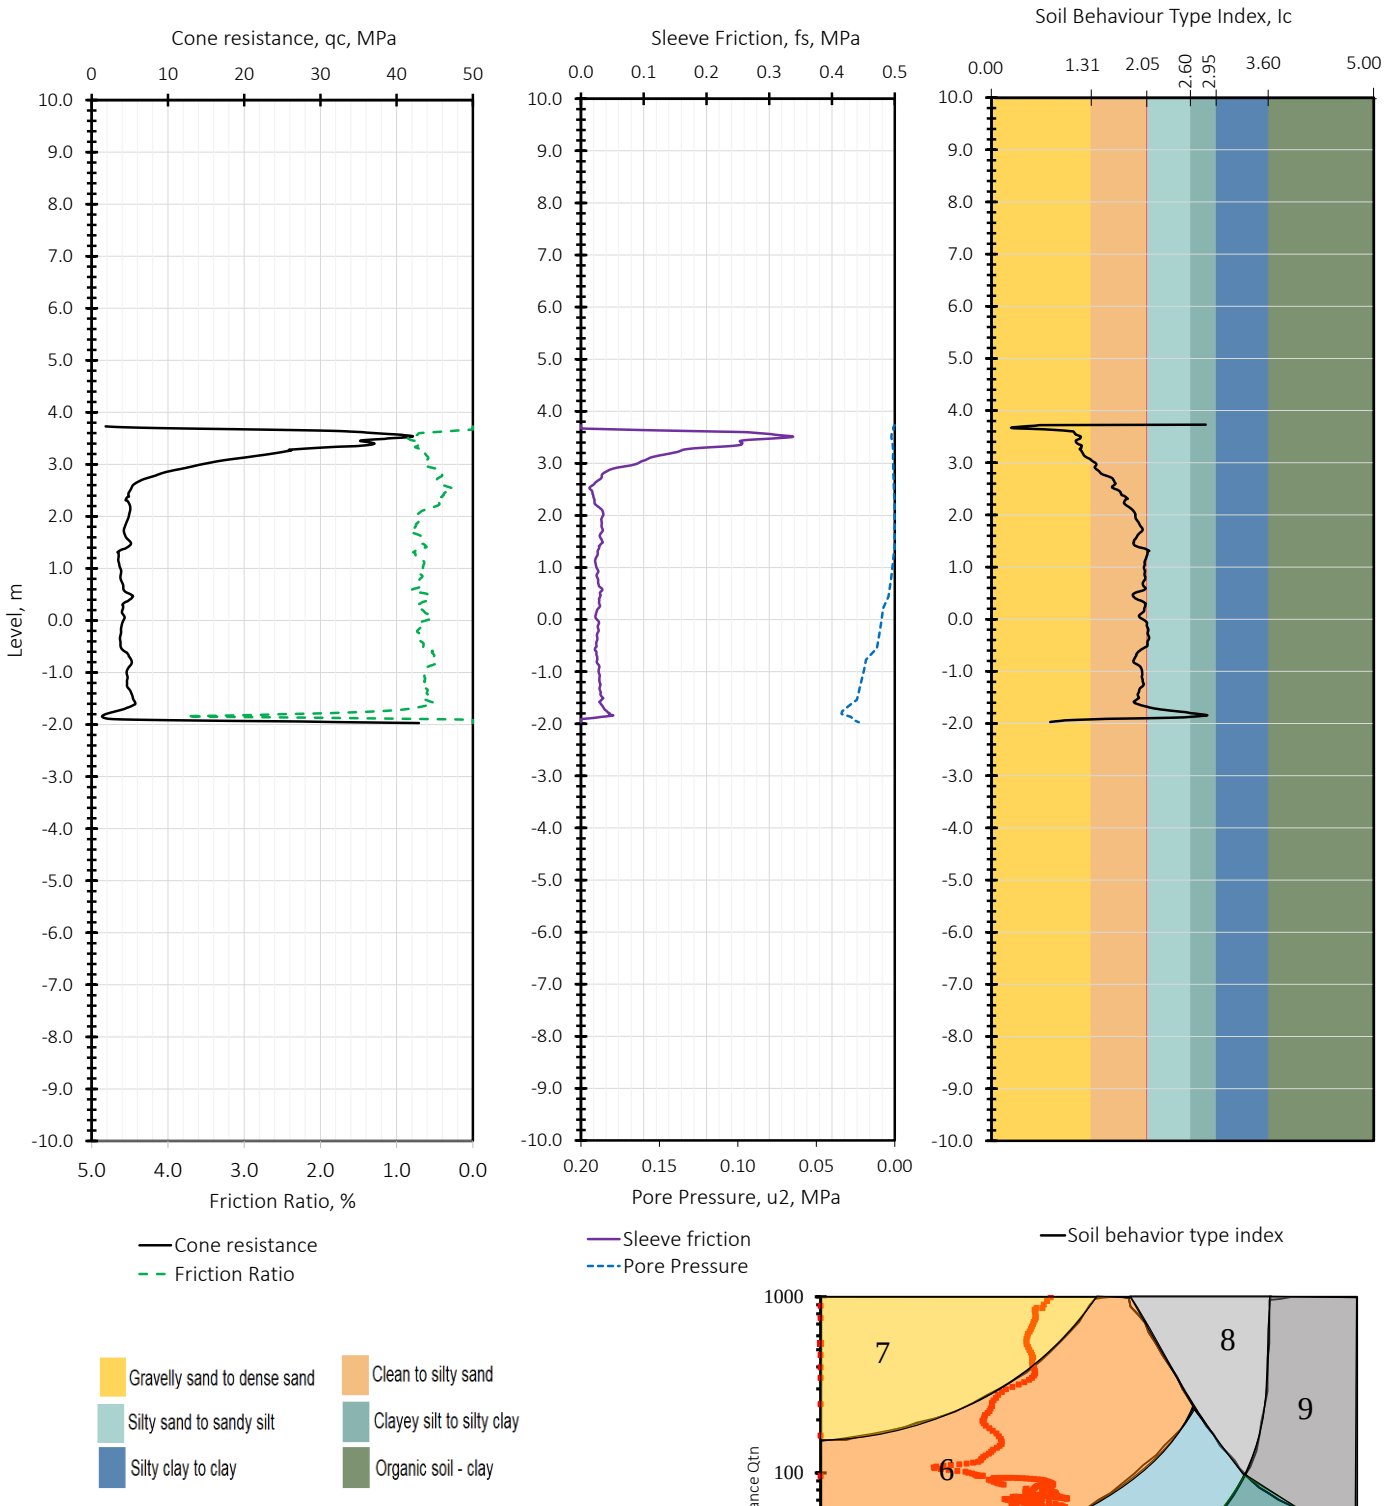

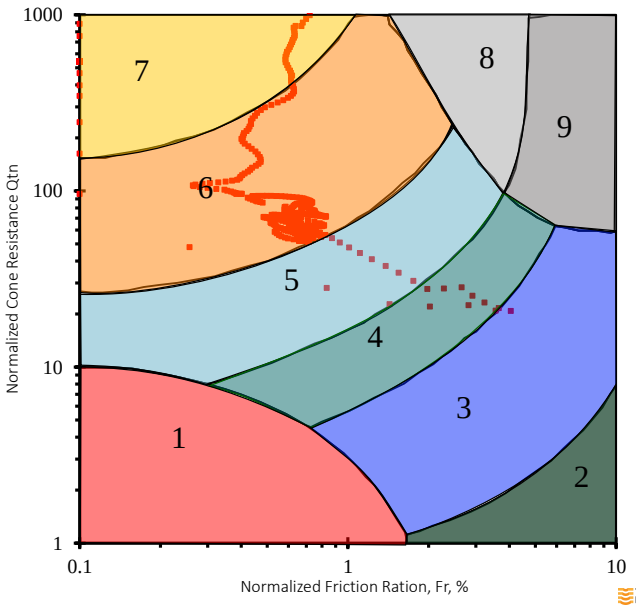

Main Contractor:	CTS GULF	
Test Location:	CPT-A1-B223-100	
Ground Elevation:	3.73	
	Easting	**Northing**
Coordinates:	420899.774	2927872.131
Cone ID:	DP15-CFPTxy.71431	
Test Date	5-Oct-2026	