
Client : SAUDI GLOBAL PORTS

Project : DAMMAM LOGISTICS ZONE

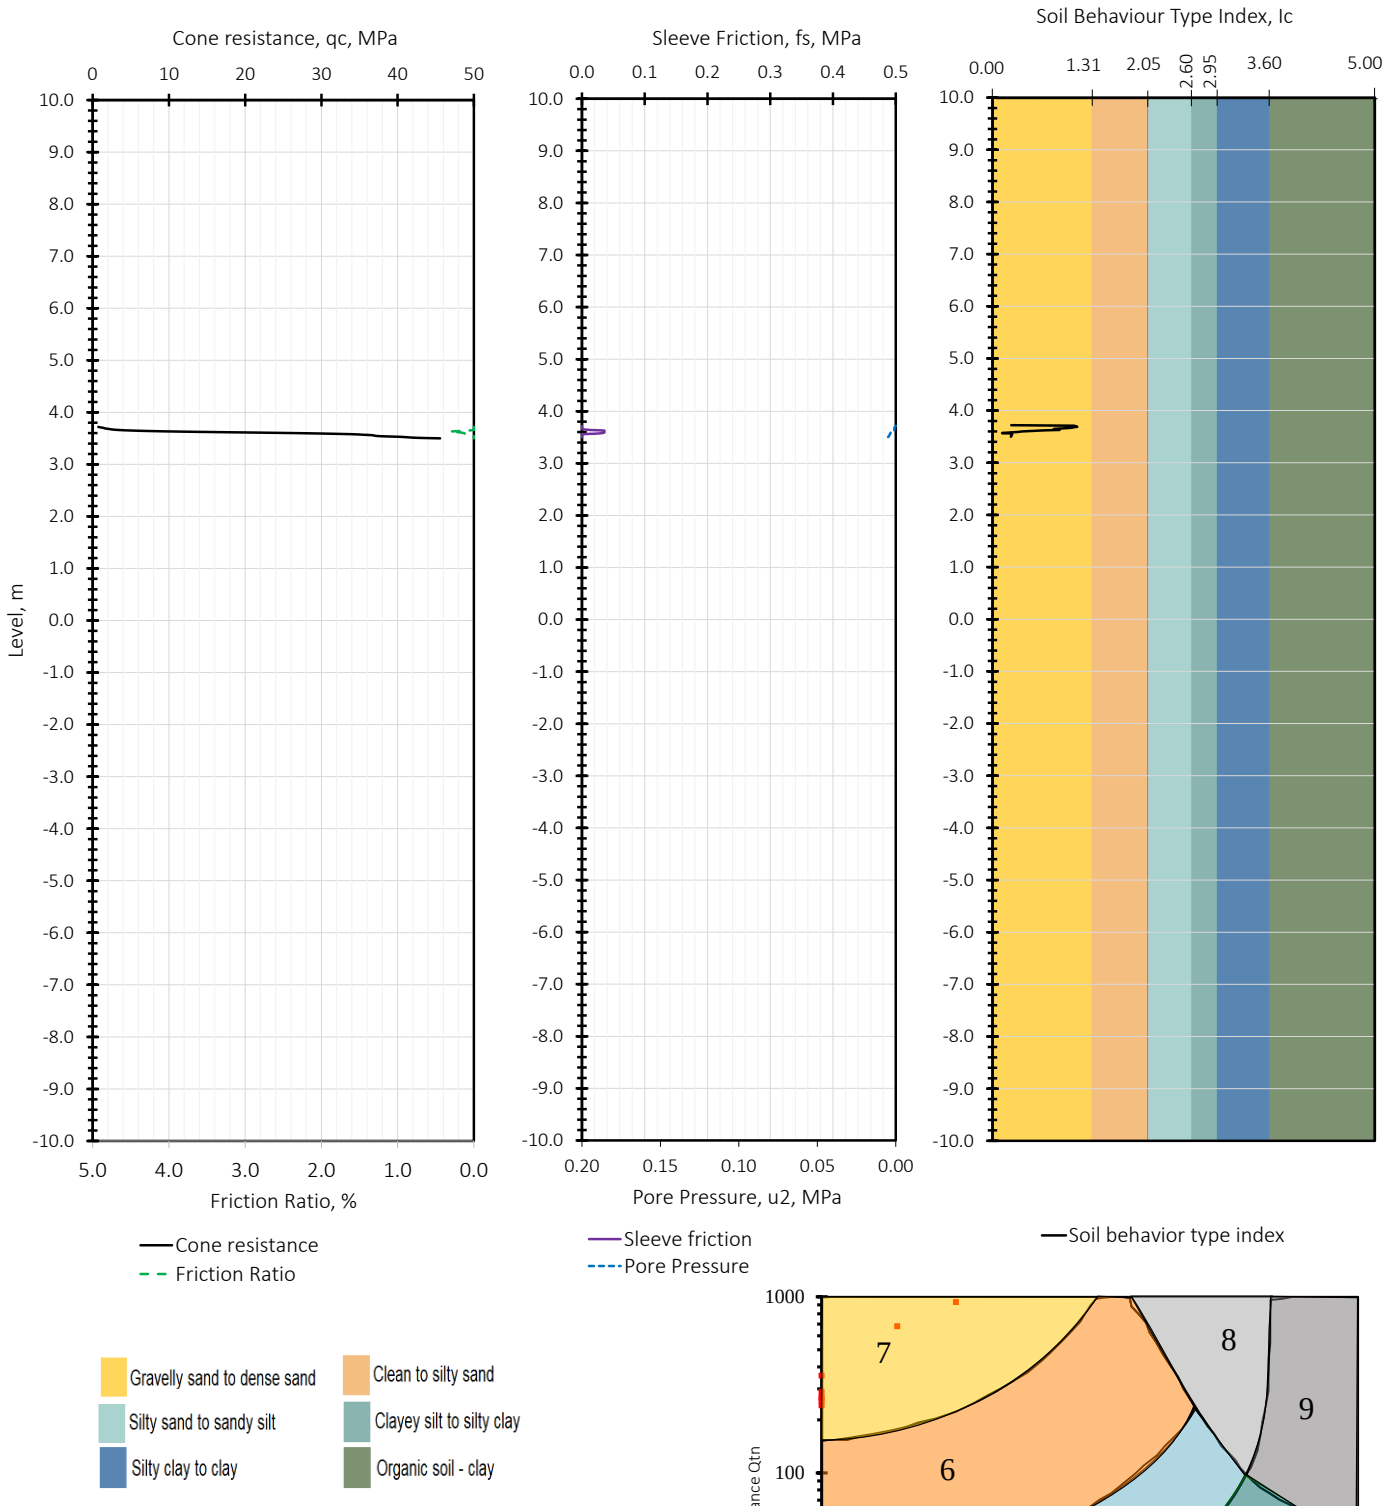

Main Contractor:	CTS GULF	
Test Location:	CPT-A1-B224.100	
Ground Elevation:	3.72	
	Easting	**Northing**
Coordinates:	420907.011	2927896.06
Cone ID:	DP15-CFPTxy.71431	
Test Date	5-Oct-2026	