

Client : SAUDI GLOBAL PORTS

Project : DAMMAM LOGISTICS ZONE

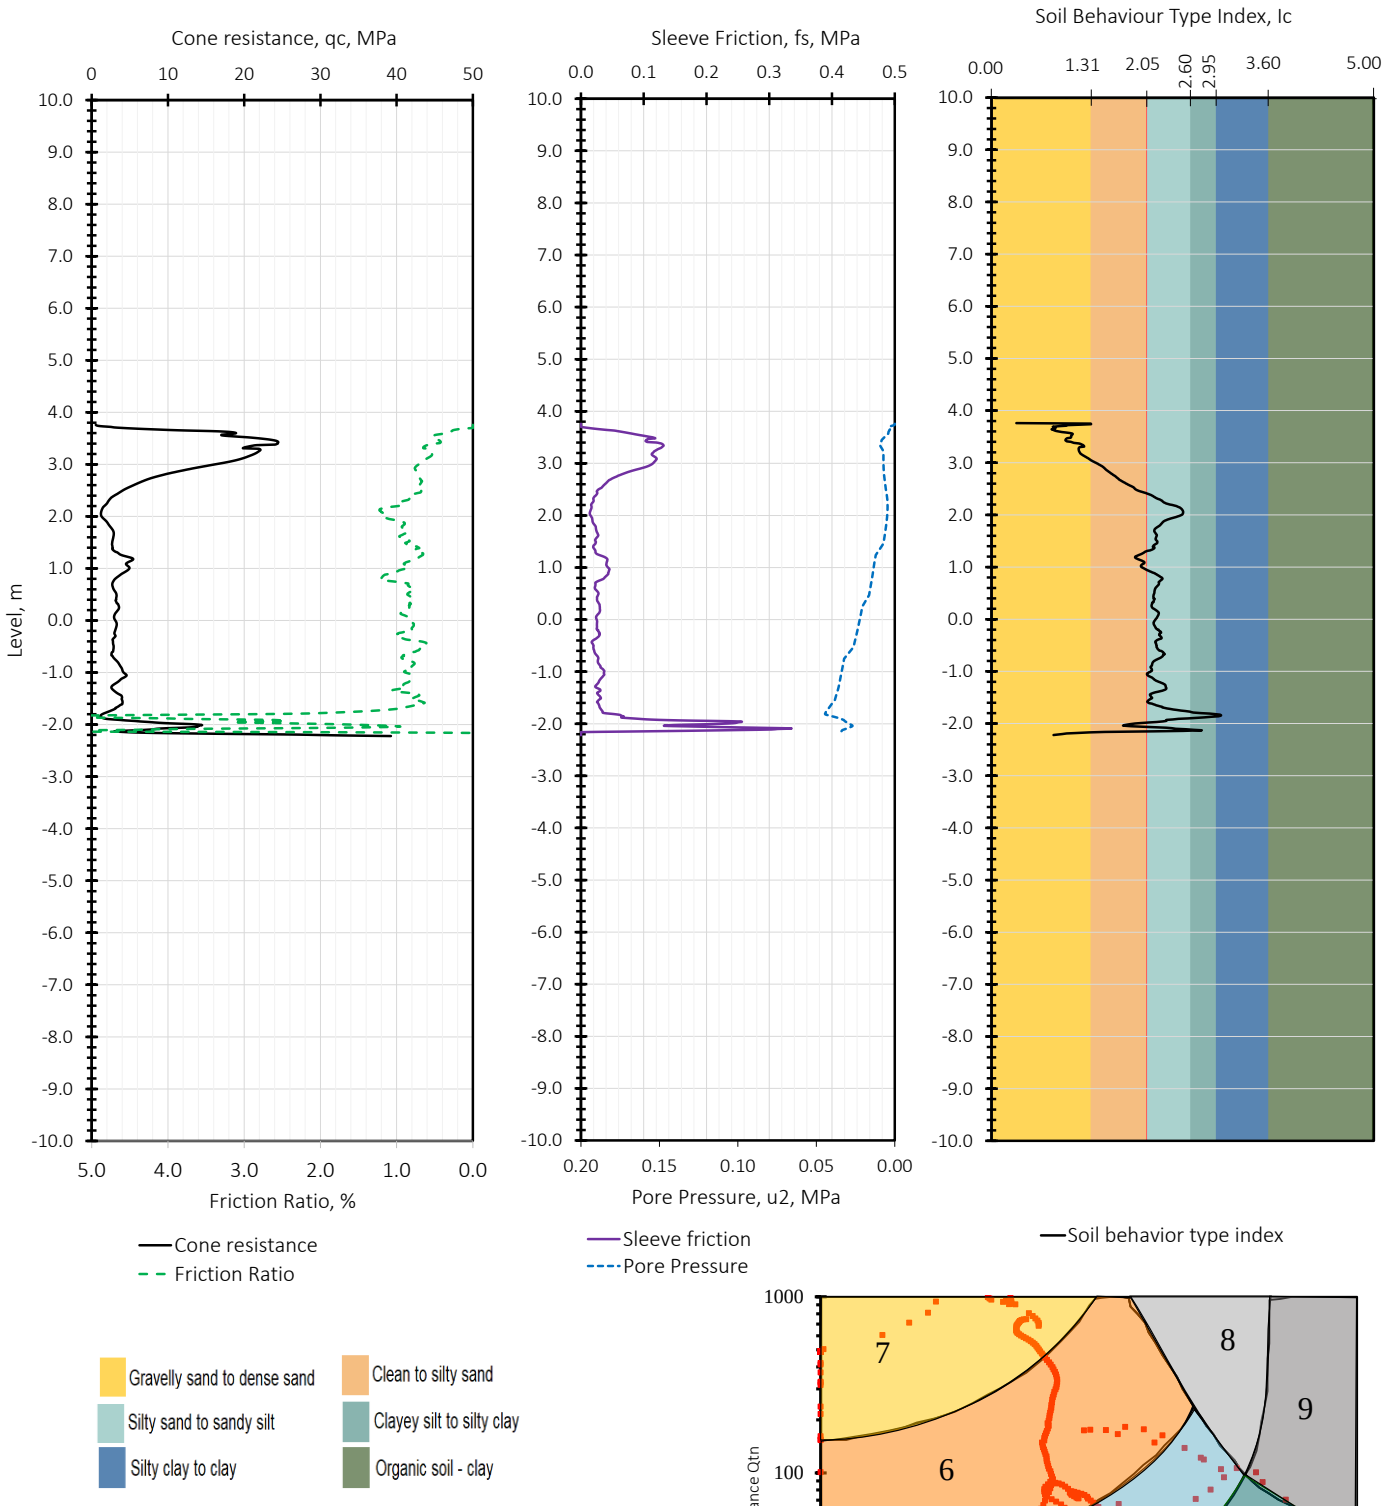

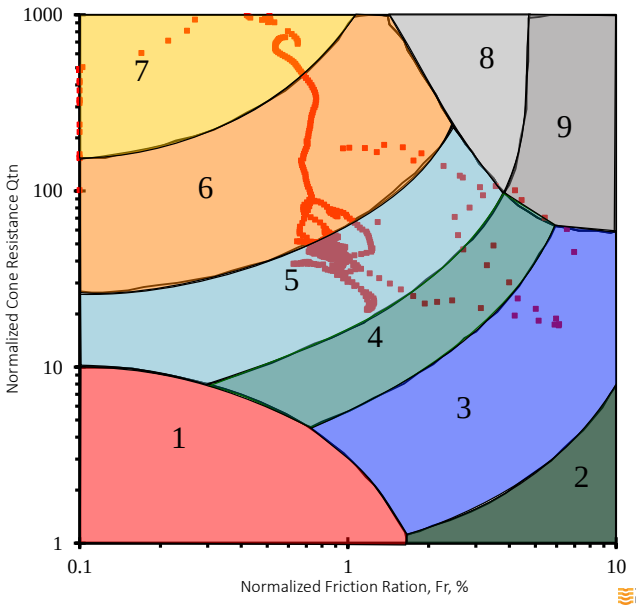

Main Contractor:	CTS GULF	
Test Location:	CPT-A1-B225-100	
Ground Elevation:	3.76	
	Easting	**Northing**
Coordinates:	420914.247	2927919.99
Cone ID:	DP15-CFPTxy.71431	
Test Date	5-Oct-2026	