

Client : SAUDI GLOBAL PORTS

Project : DAMMAM LOGISTICS ZONE

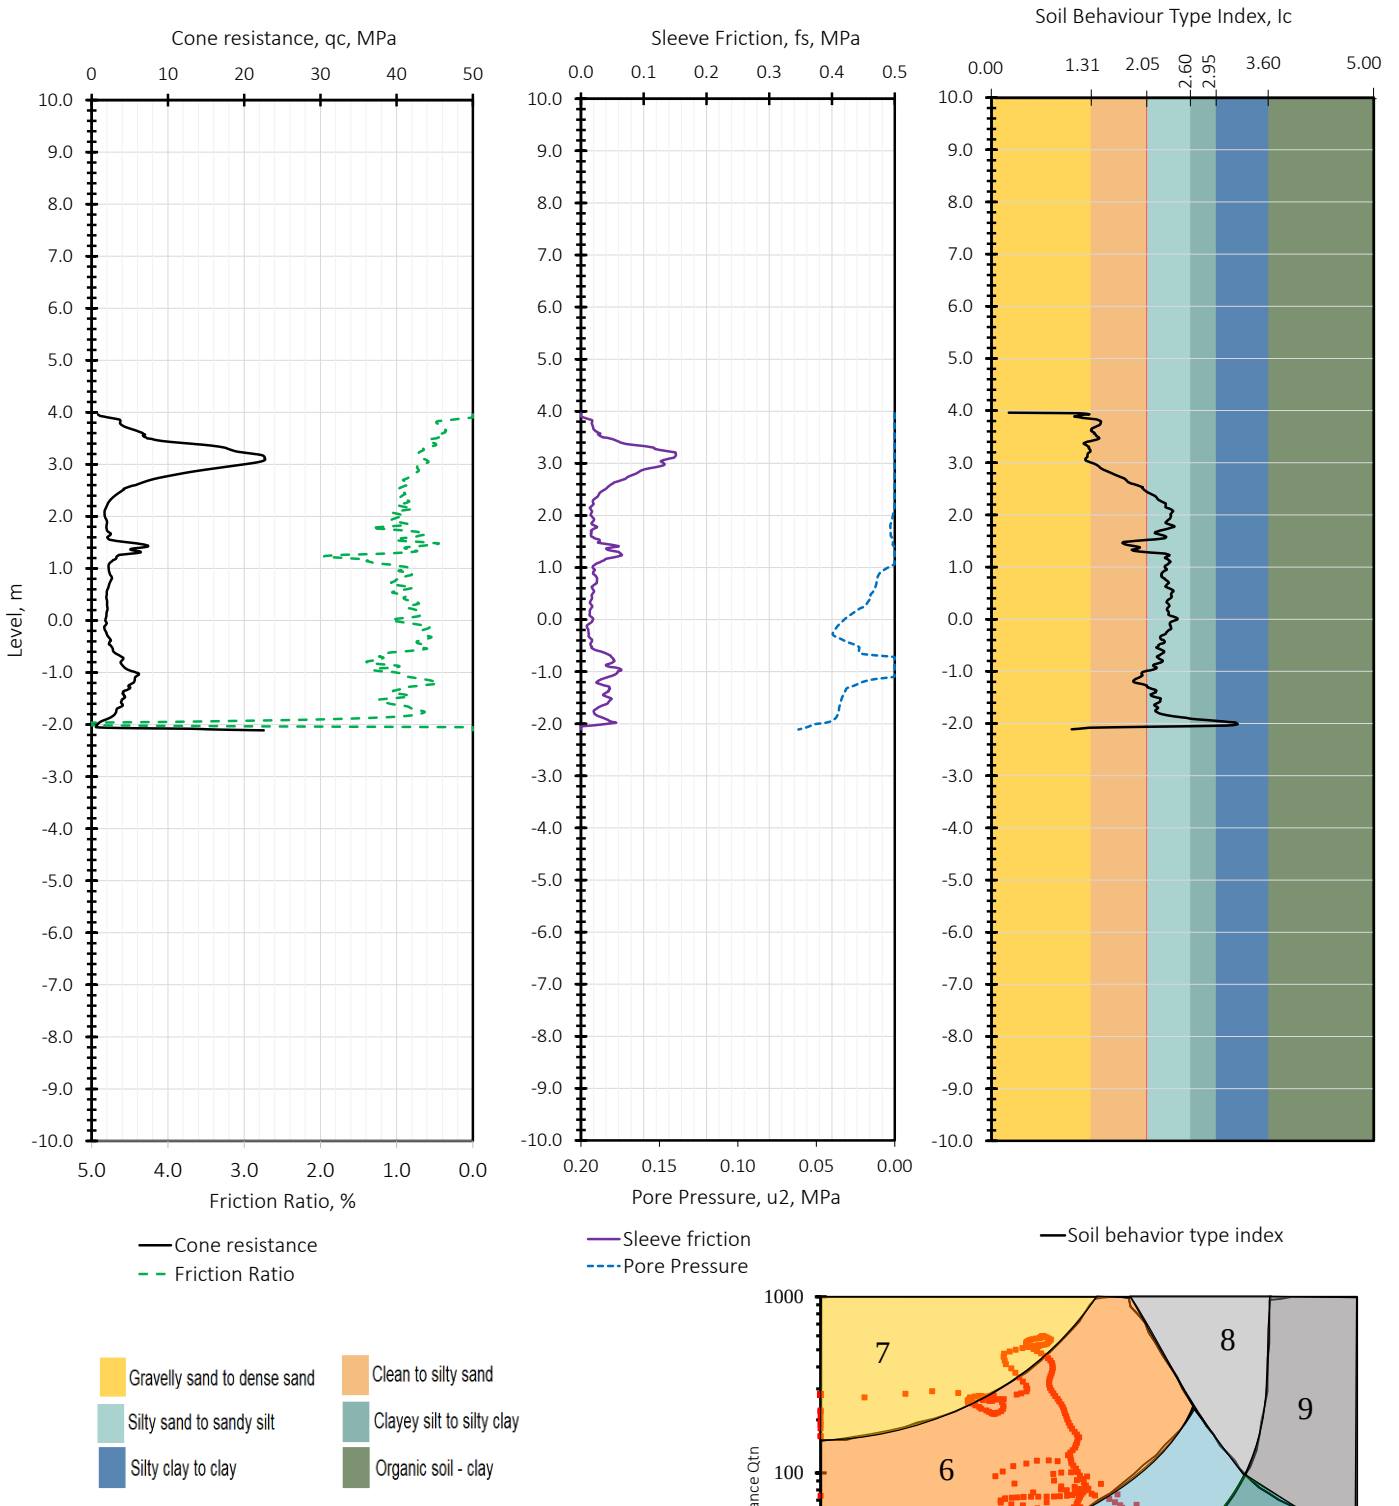

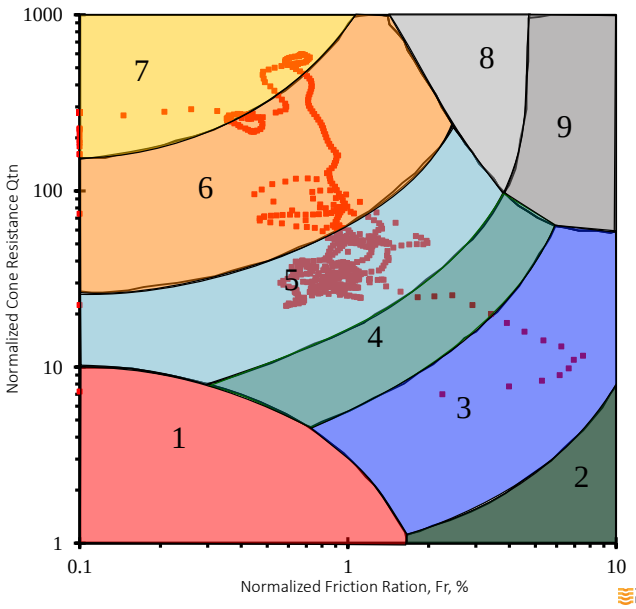

Main Contractor:	CTS GULF	
Test Location:	CPT-A1-B233-100	
Ground Elevation:	3.96	
	Easting	**Northing**
Coordinates:	420972.142	2928111.427
Cone ID:	DP15-CFPTxy.71431	
Test Date	5-Oct-2026	