
Client : SAUDI GLOBAL PORTS

Project : DAMMAM LOGISTICS ZONE

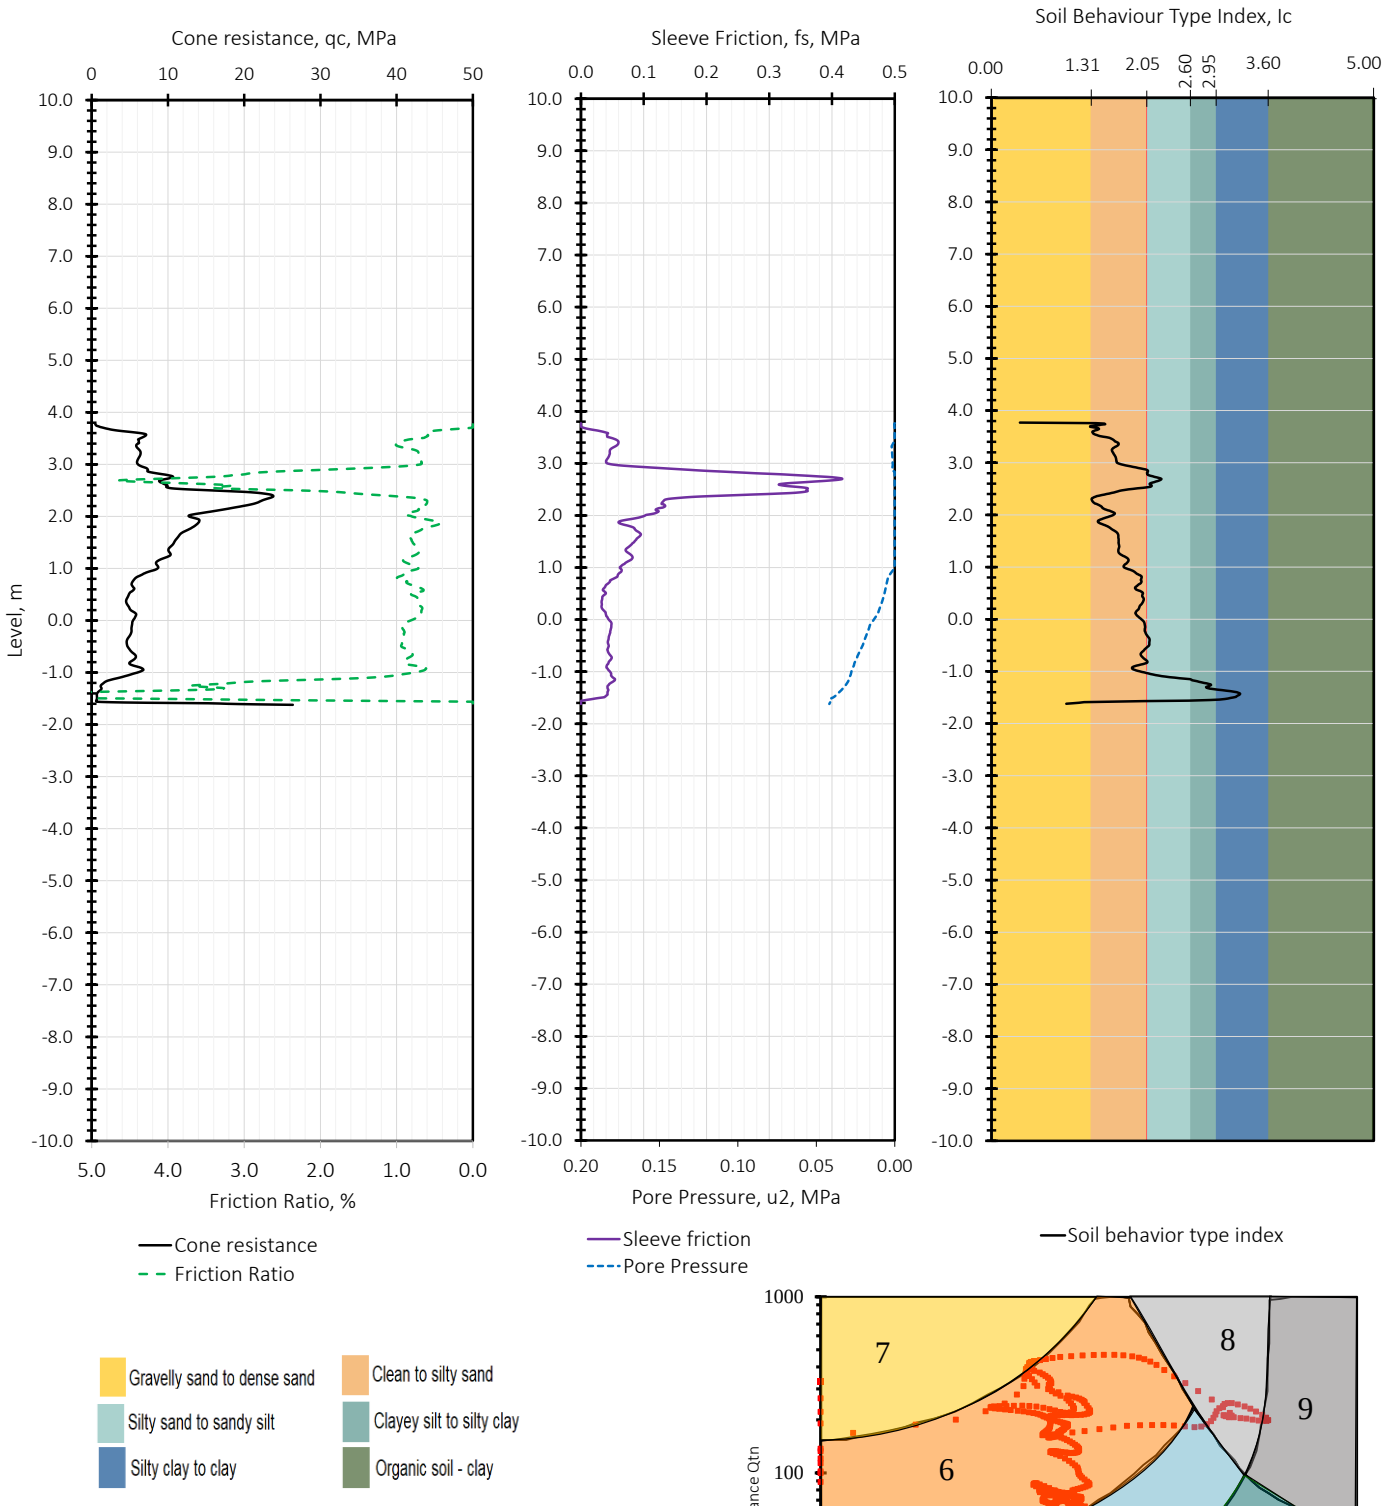

Main Contractor:	CTS GULF	
Test Location:	CPT-A1-B249-100	
Ground Elevation:	3.77	
	Easting	**Northing**
Coordinates:	420845.207	2927601.332
Cone ID:	DP15-CFPTxy.71424	
Test Date	13-Oct-2026	