
Client : SAUDI GLOBAL PORTS

Project : DAMMAM LOGISTICS ZONE

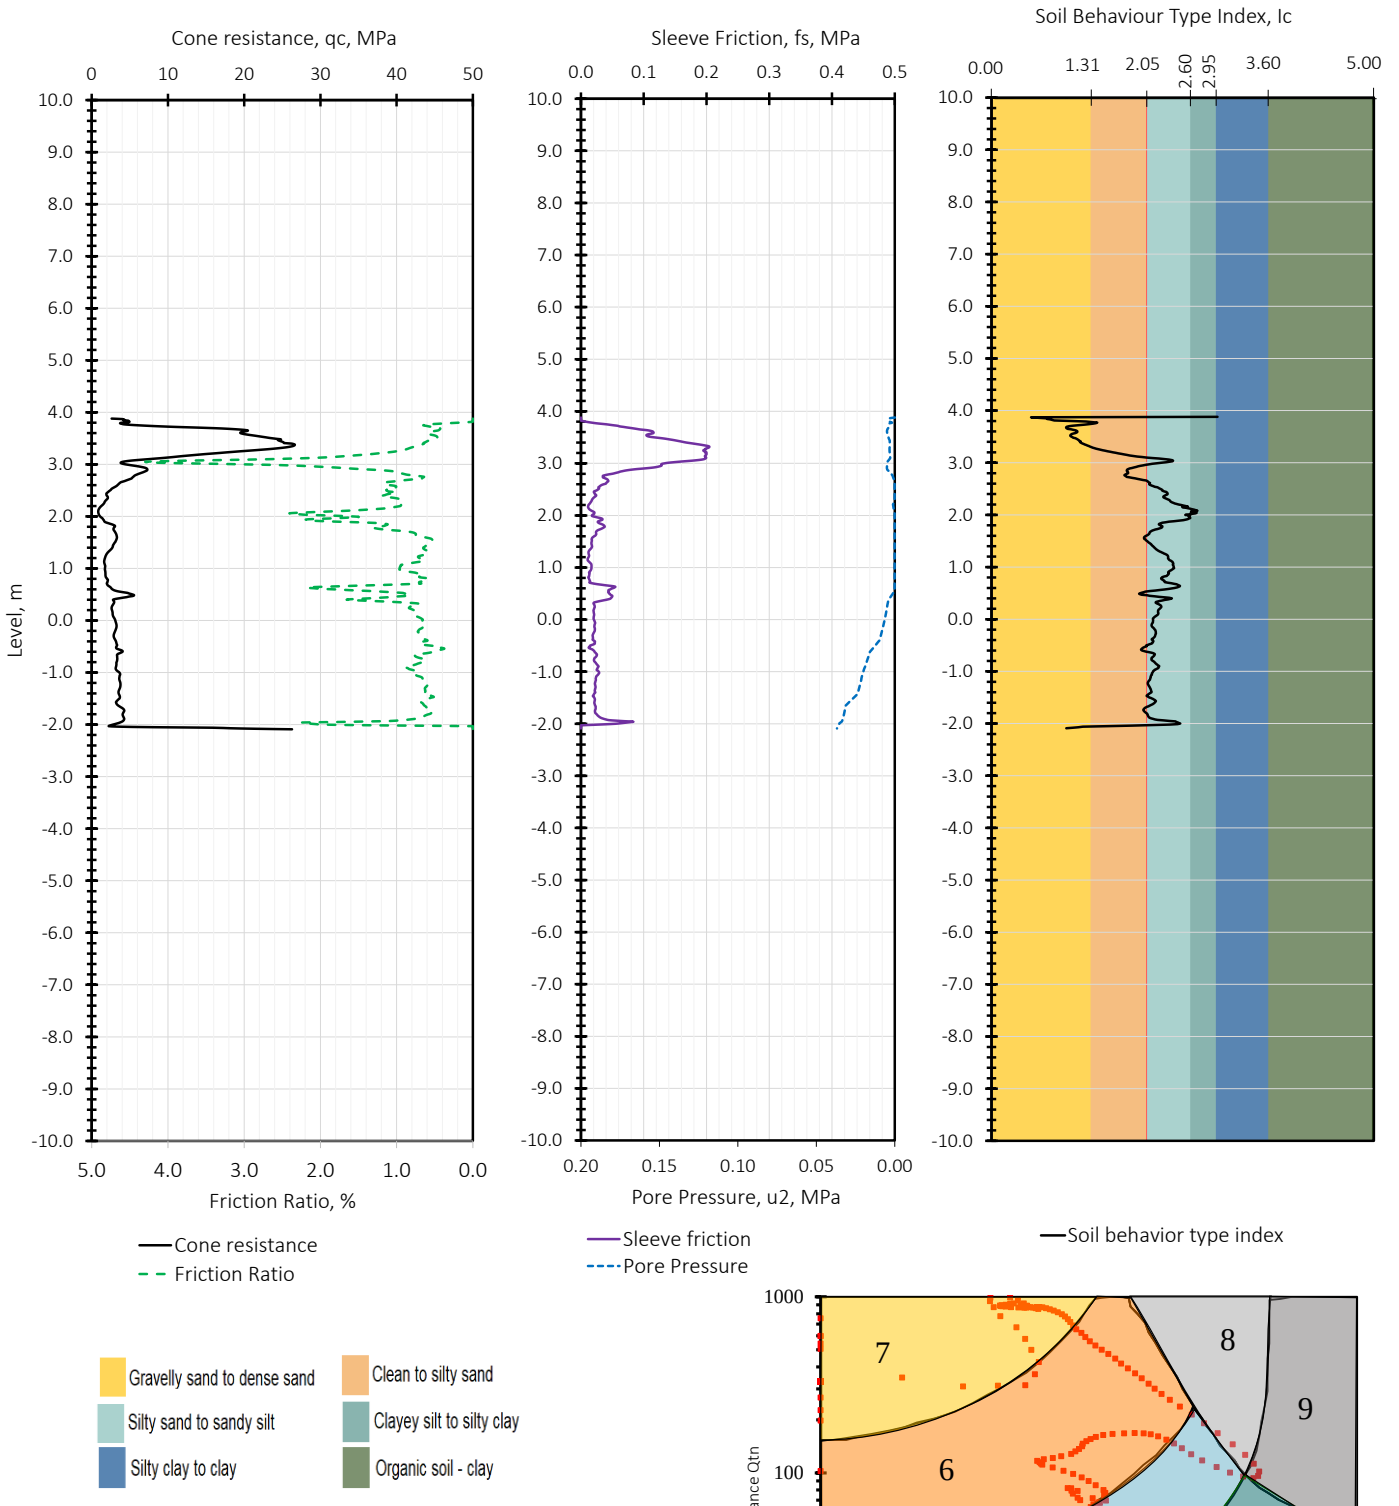

Main Contractor:	CTS GULF	
Test Location:	CPT-A1-B269-100	
Ground Elevation:	3.88	
	Easting	**Northing**
Coordinates:	420988.986	2928080.215
Cone ID:	DP15-CFPTxy.71431	
Test Date	6-Oct-2026	