

Client : SAUDI GLOBAL PORTS

Project : DAMMAM LOGISTICS ZONE

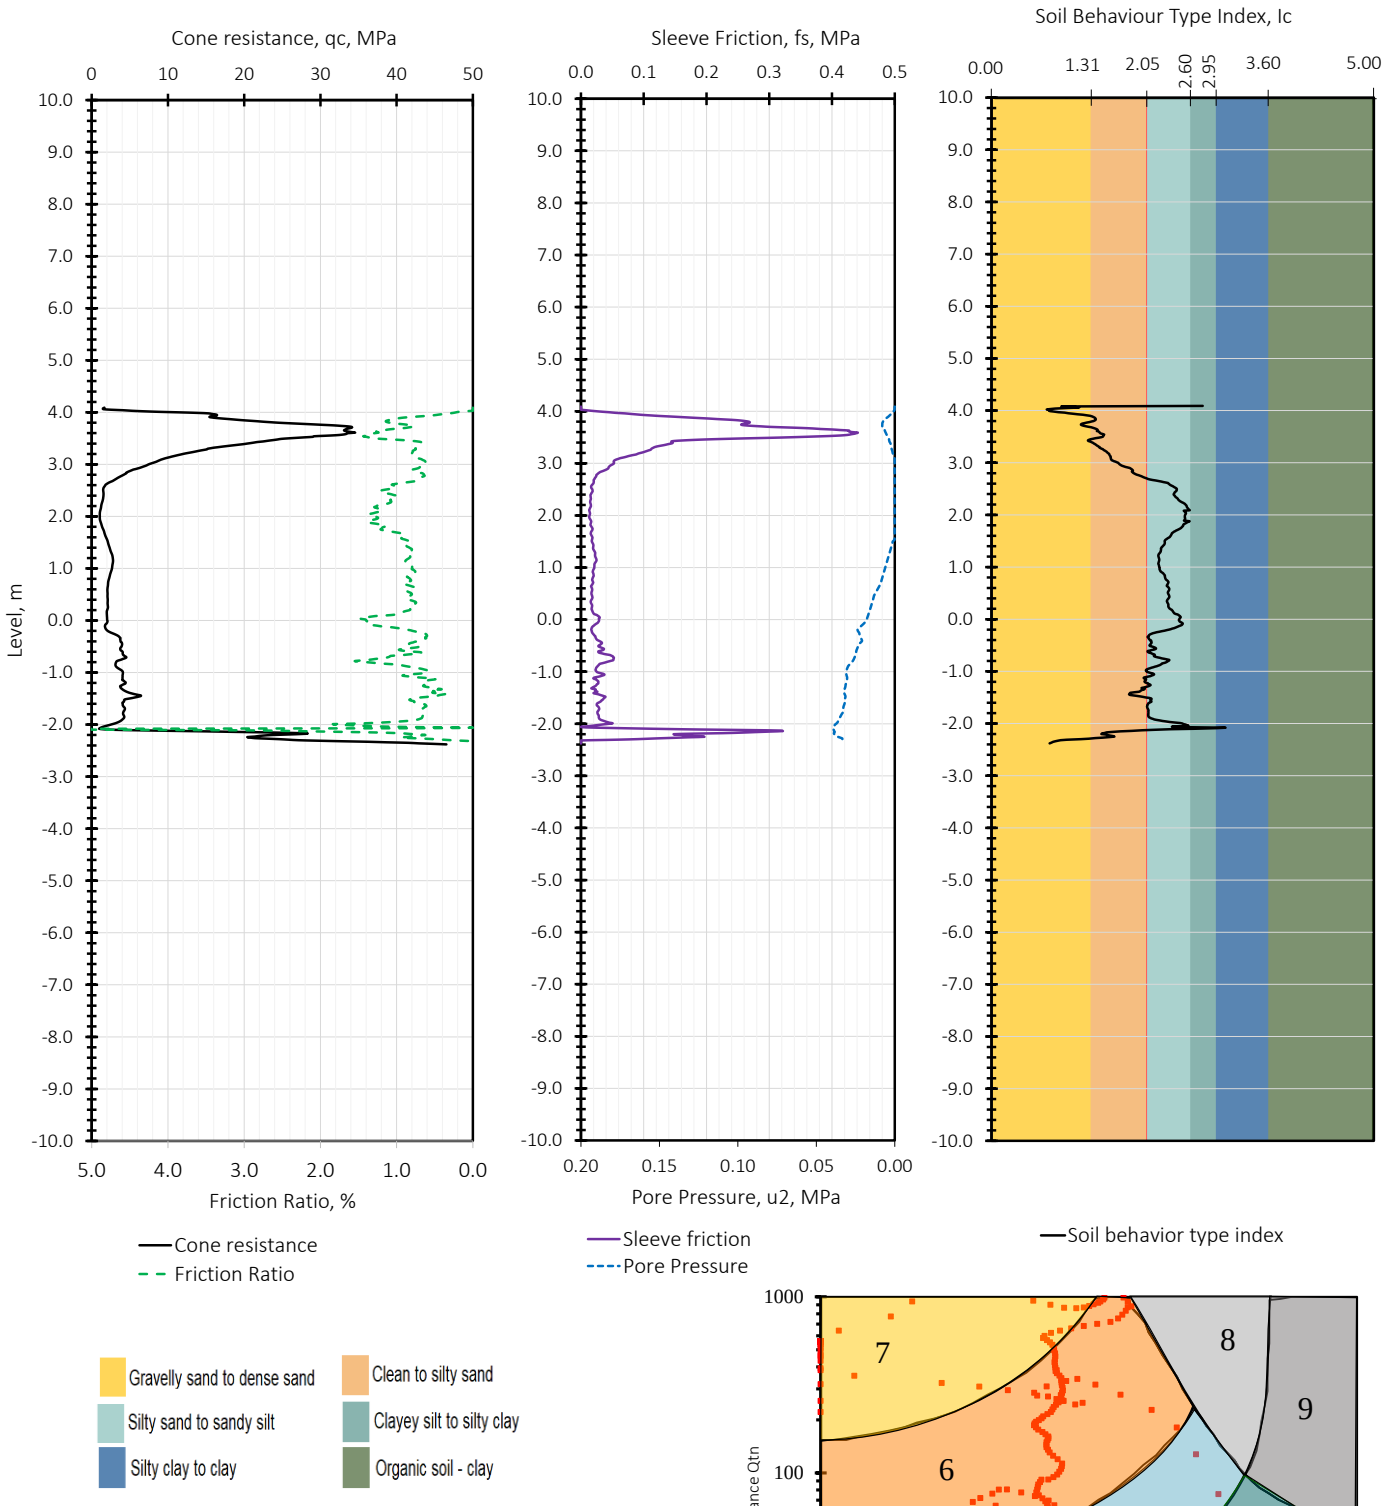

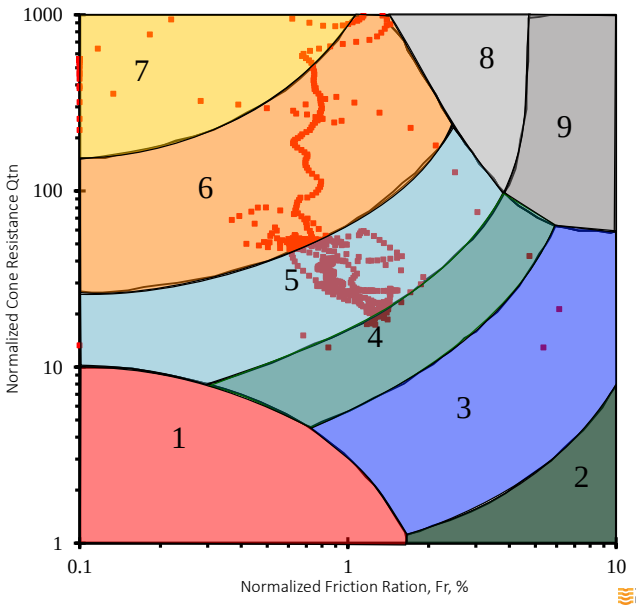

Main Contractor:	CTS GULF	
Test Location:	CPT-A1-B270-100	
Ground Elevation:	4.09	
	Easting	**Northing**
Coordinates:	420996.136	2928104.171
Cone ID:	DP15-CFPTxy.71431	
Test Date	6-Oct-2026	