

Client : SAUDI GLOBAL PORTS

Project : DAMMAM LOGISTICS ZONE

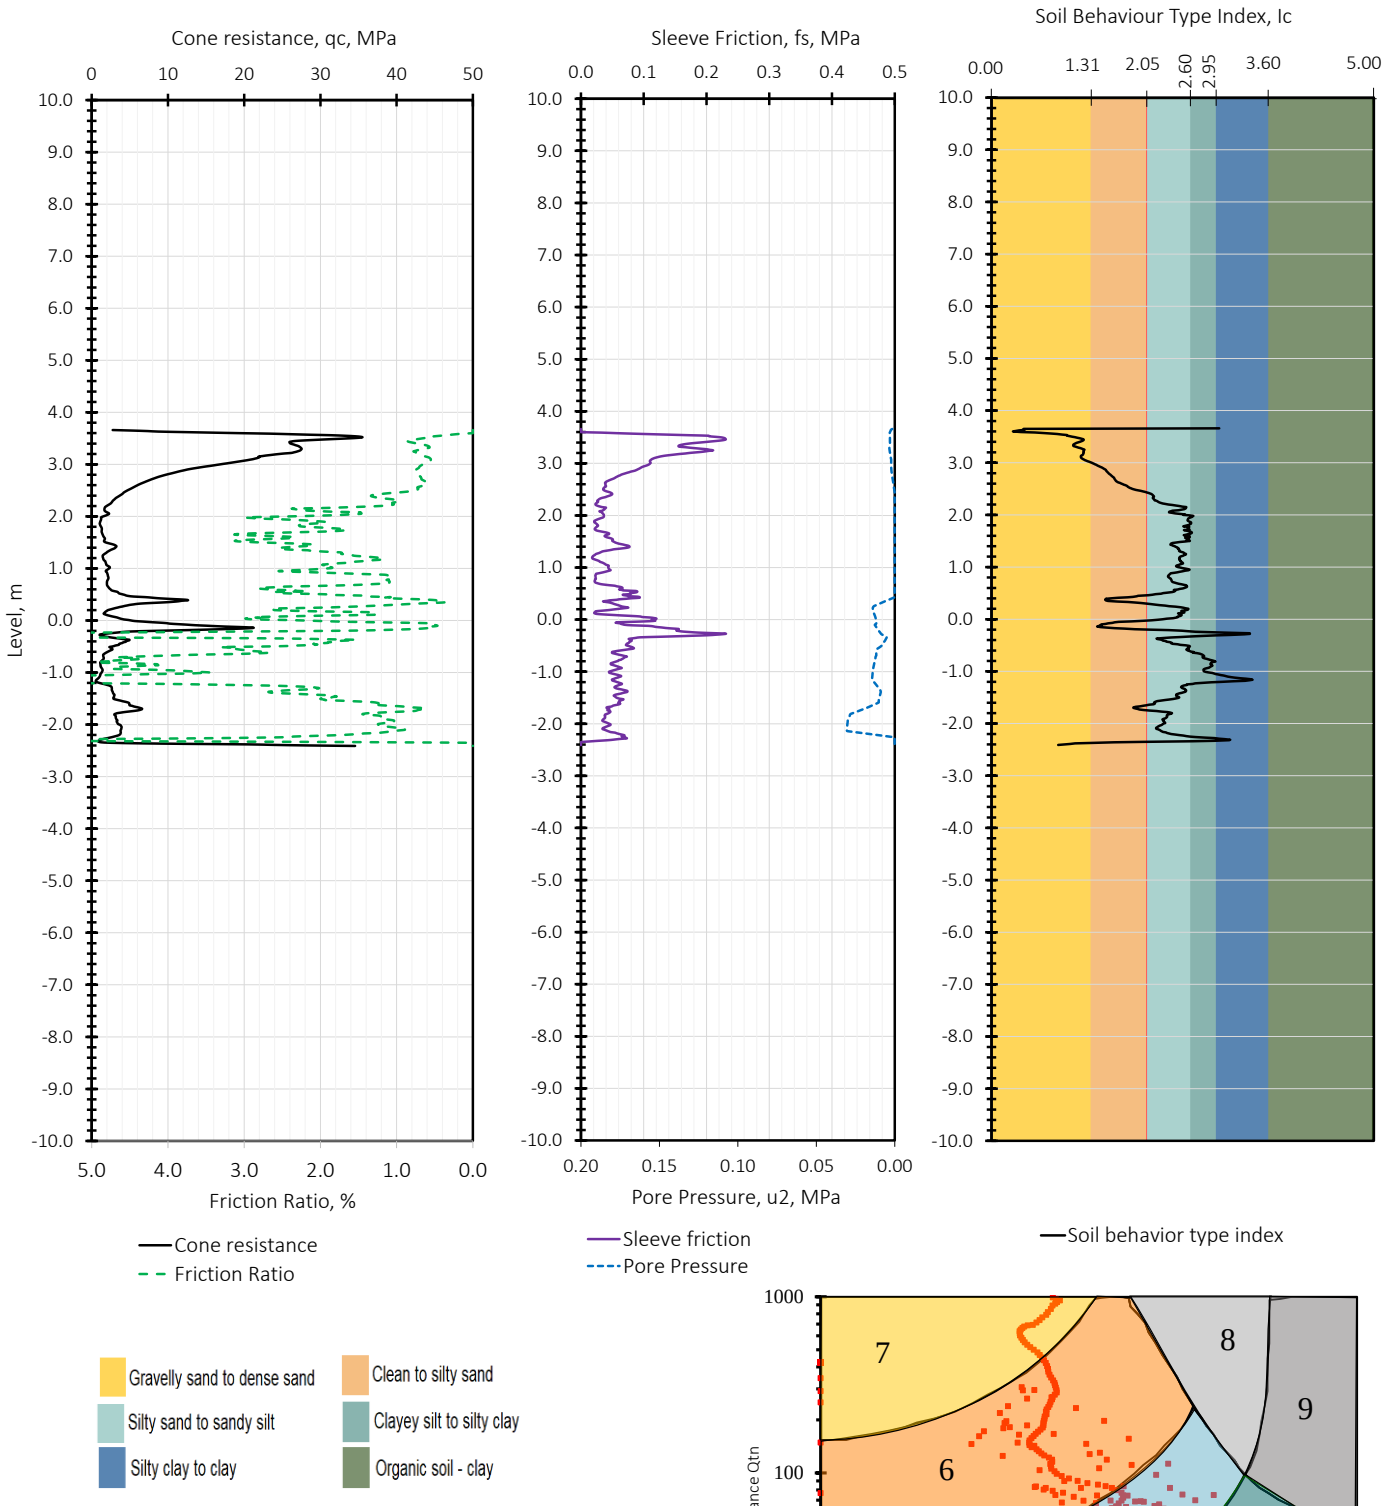

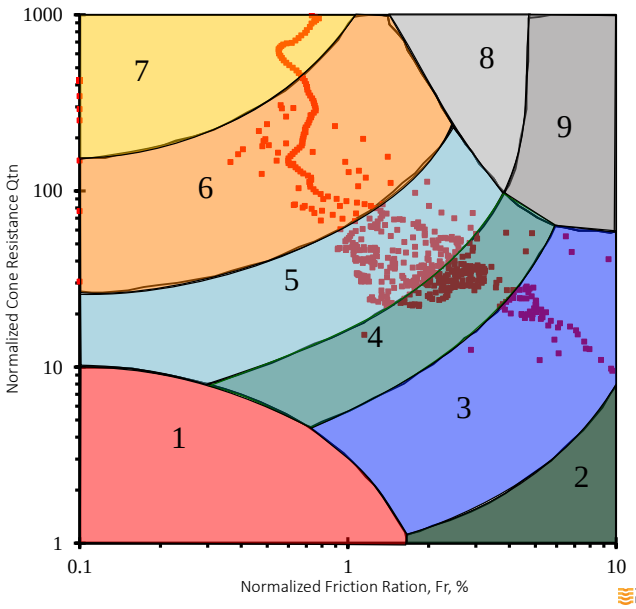

Main Contractor:	CTS GULF	
Test Location:	CPT-A1-B274-100	
Ground Elevation:	3.66	
	Easting	**Northing**
Coordinates:	421025.019	2928199.909
Cone ID:	DP15-CFPTxy.71431	
Test Date	1-Oct-2026	