
Client : SAUDI GLOBAL PORTS

Project : DAMMAM LOGISTICS ZONE

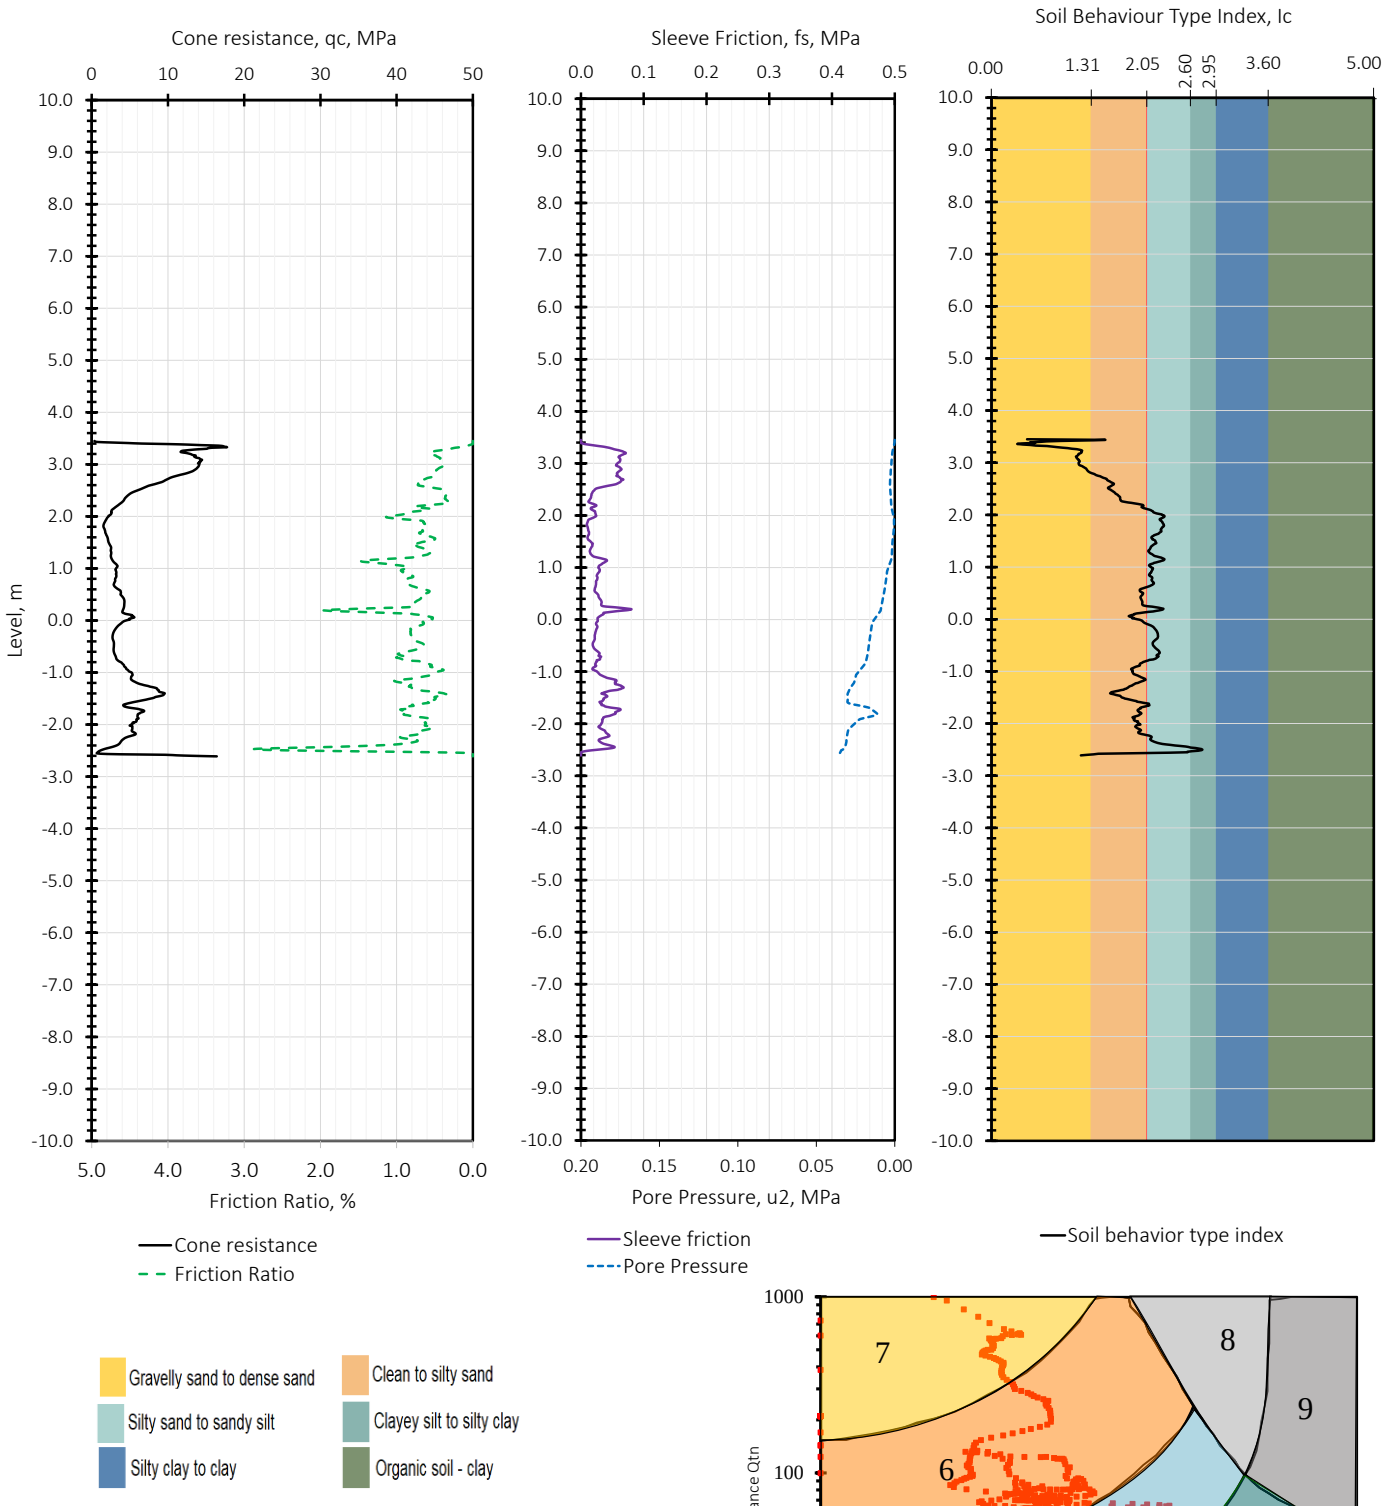

Main Contractor:	CTS GULF	
Test Location:	CPT-A1-B278-100-1	
Ground Elevation:	3.45	
	Easting	**Northing**
Coordinates:	421053.966	2928295.628
Cone ID:	DP15-CFPTxy.71432	
Test Date	27-Sep-2026	