

Client : SAUDI GLOBAL PORTS

Project : DAMMAM LOGISTICS ZONE

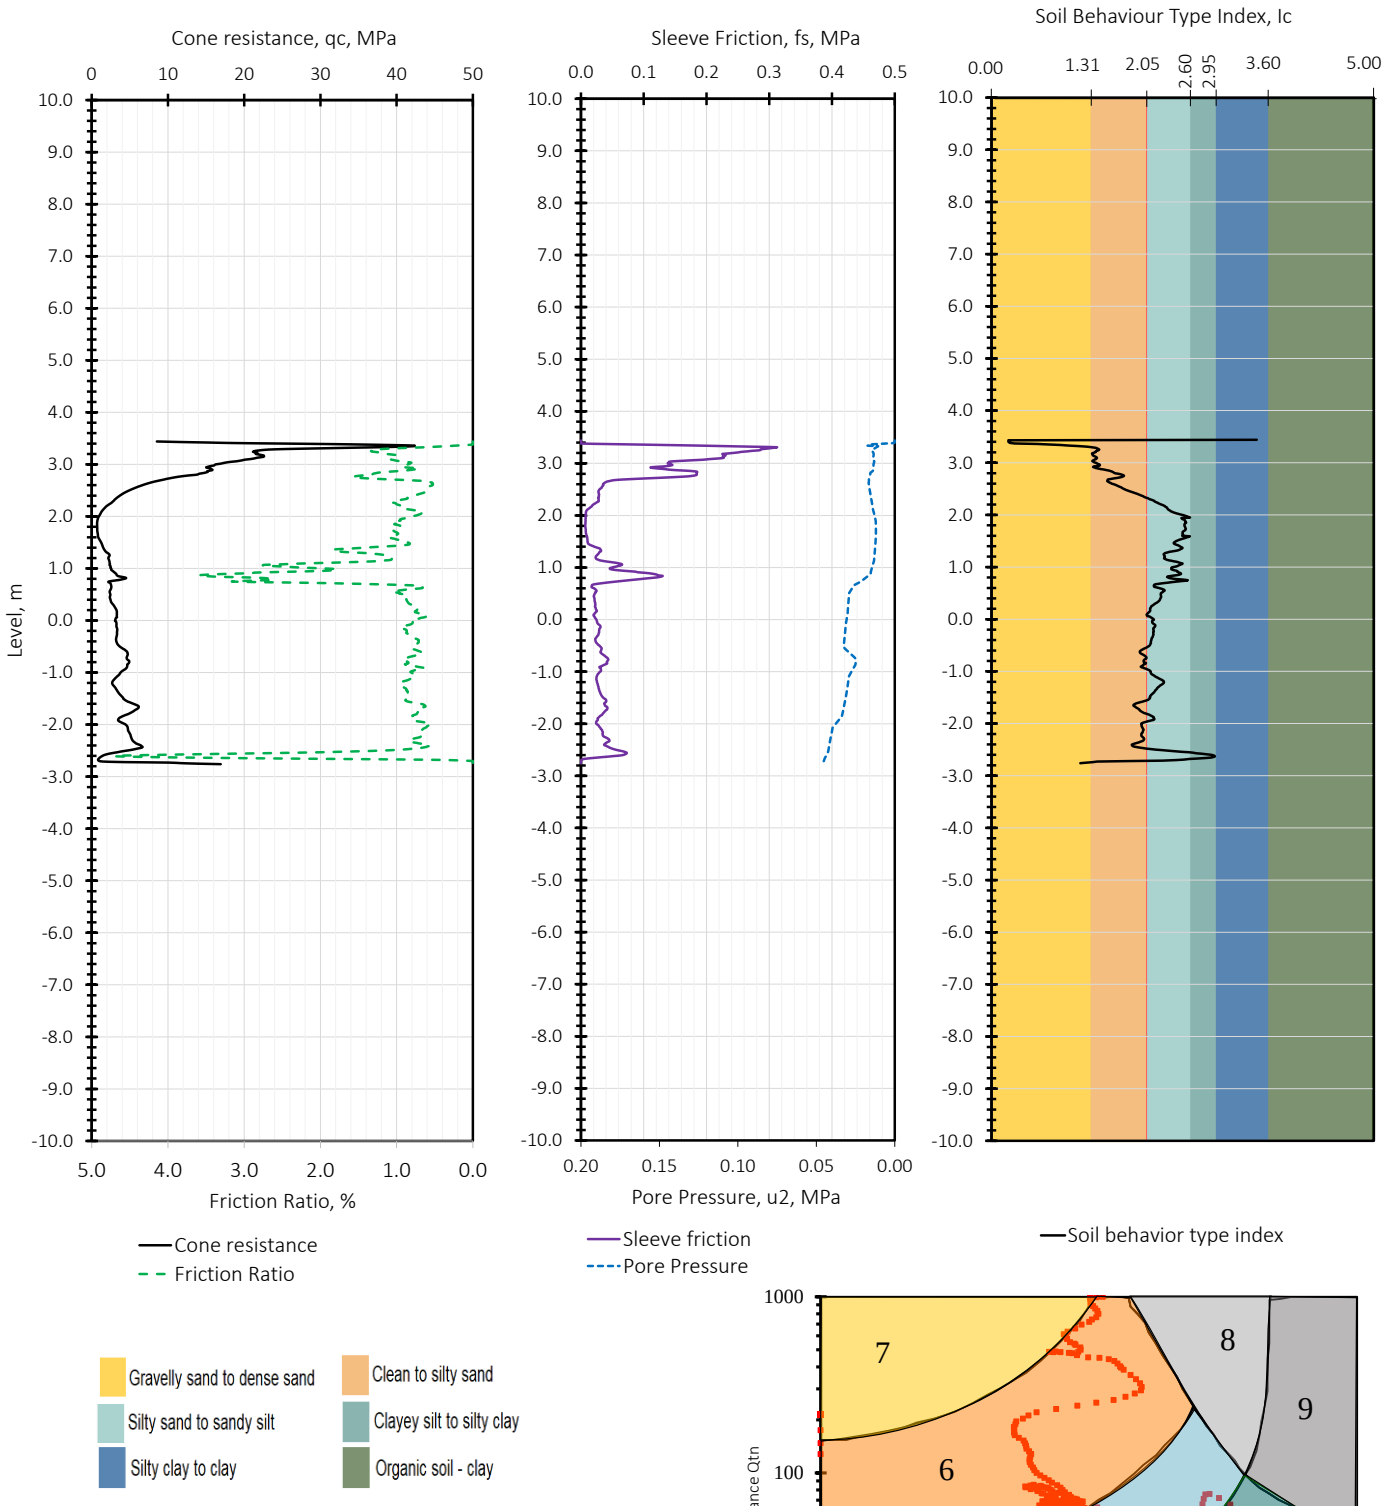

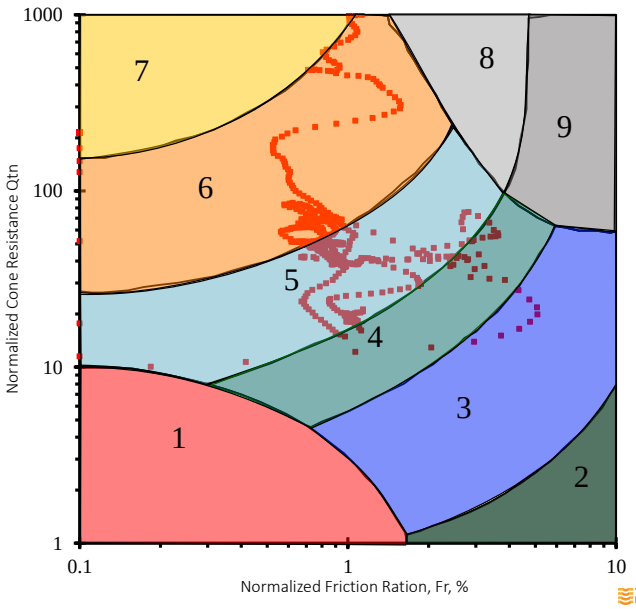

Main Contractor:	CTS GULF	
Test Location:	CPT-A1-B279-100	
Ground Elevation:	3.44	
	Easting	**Northing**
Coordinates:	421061.203	2928319.558
Cone ID:	DP15-CFPTxy.71432	
Test Date	26-Sep-2026	