
Client : SAUDI GLOBAL PORTS

Project : DAMMAM LOGISTICS ZONE

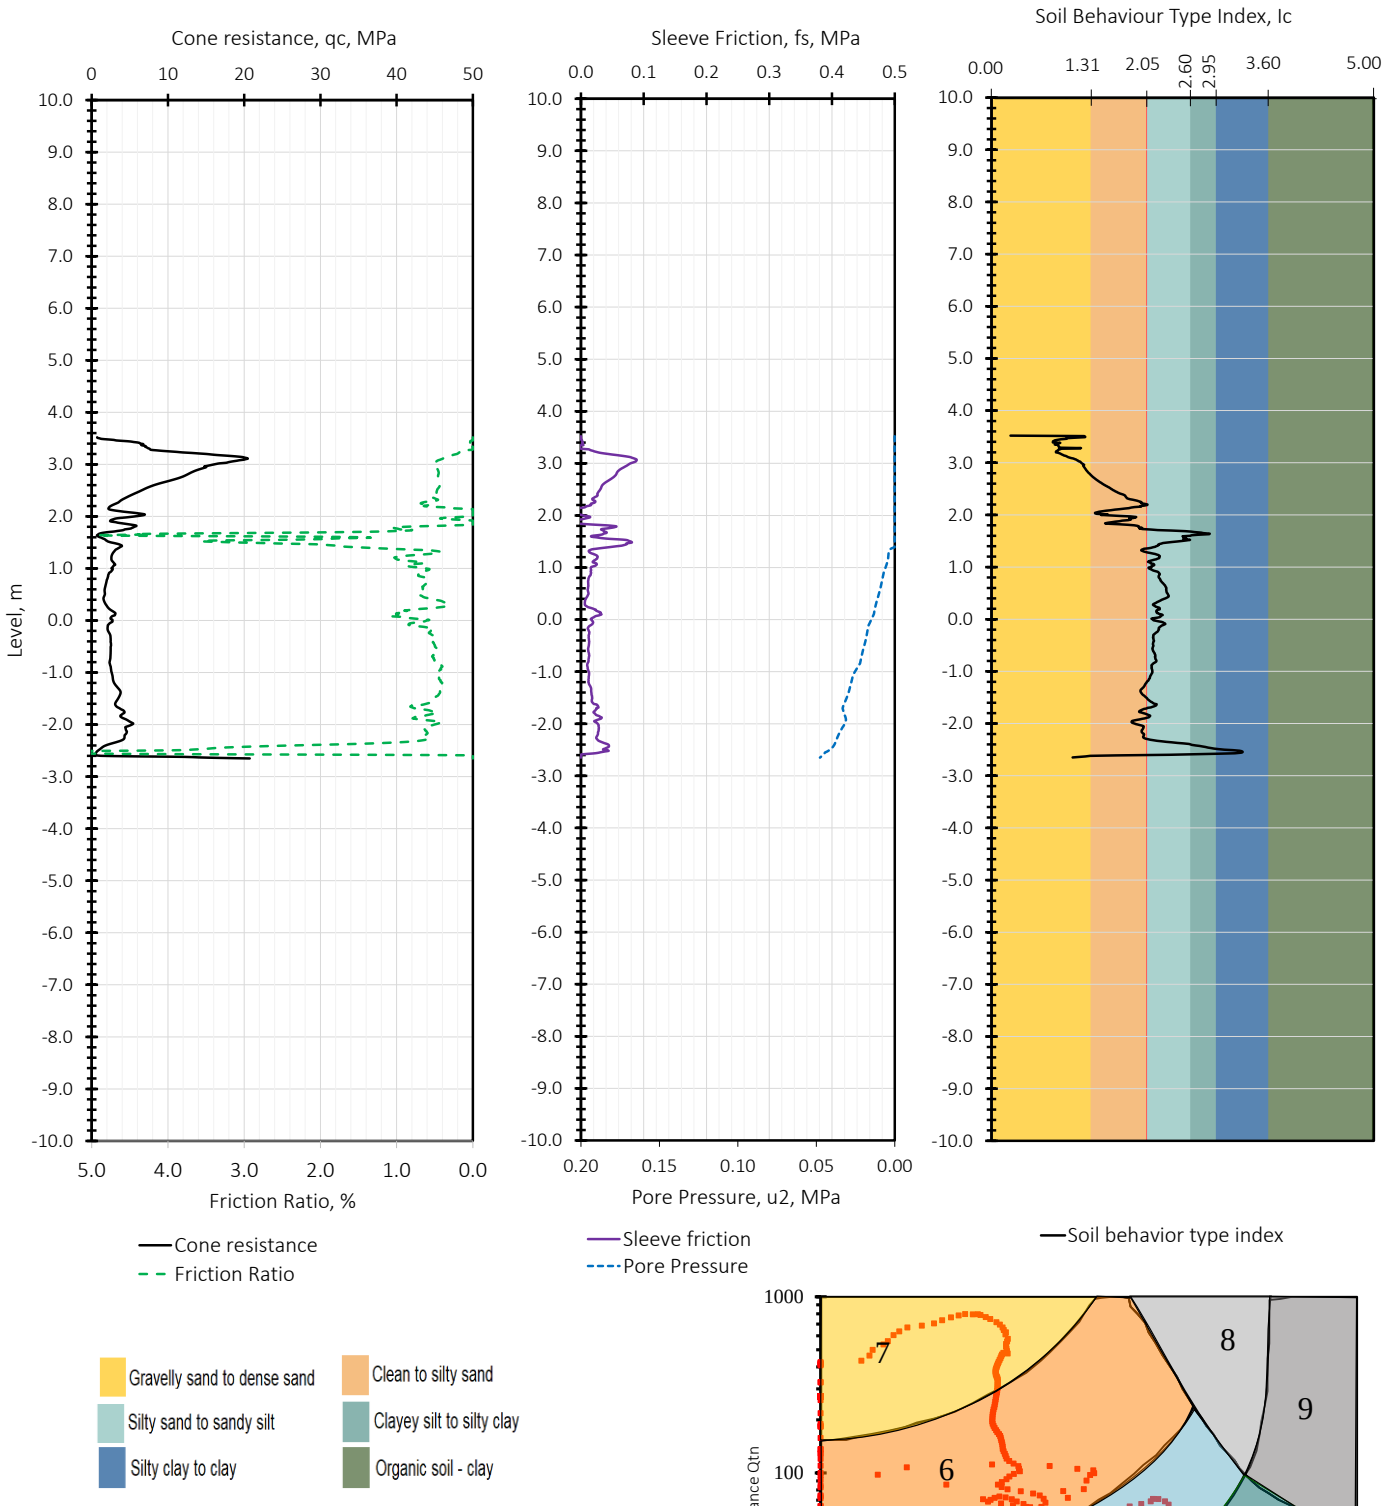

Main Contractor:	CTS GULF	
Test Location:	CPT-A1-B289-100	
Ground Elevation:	3.52	
	Easting	**Northing**
Coordinates:	421070.659	2928264.461
Cone ID:	DP15-CFPTxy.71432	
Test Date	26-Sep-2026	