
Client : SAUDI GLOBAL PORTS

Project : DAMMAM LOGISTICS ZONE

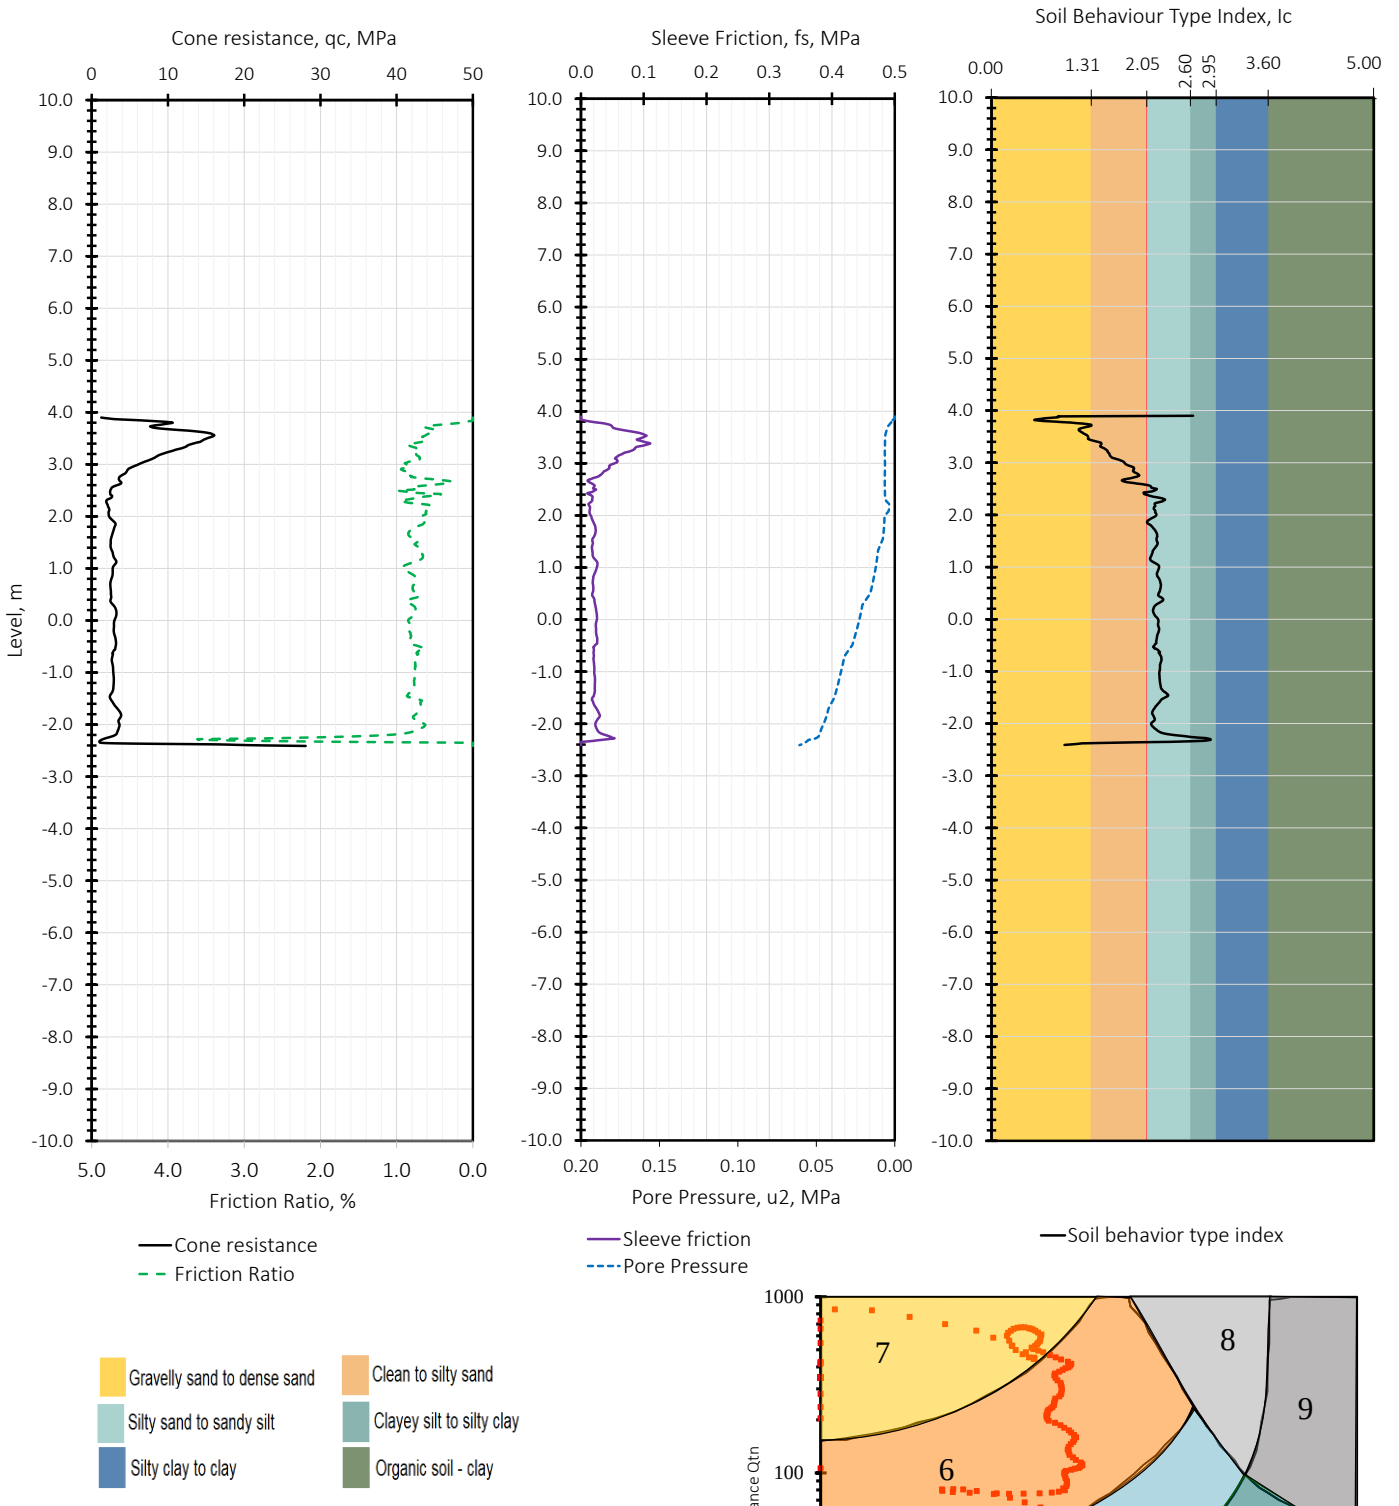

Main Contractor:	CTS GULF	
Test Location:	CPT-A1-B298-100-1	
Ground Elevation:	3.9	
	Easting	**Northing**
Coordinates:	421058.405	2928137.576
Cone ID:	DP15-CFPTxy.71432	
Test Date	30-Sep-2026	