
Client : SAUDI GLOBAL PORTS

Project : DAMMAM LOGISTICS ZONE

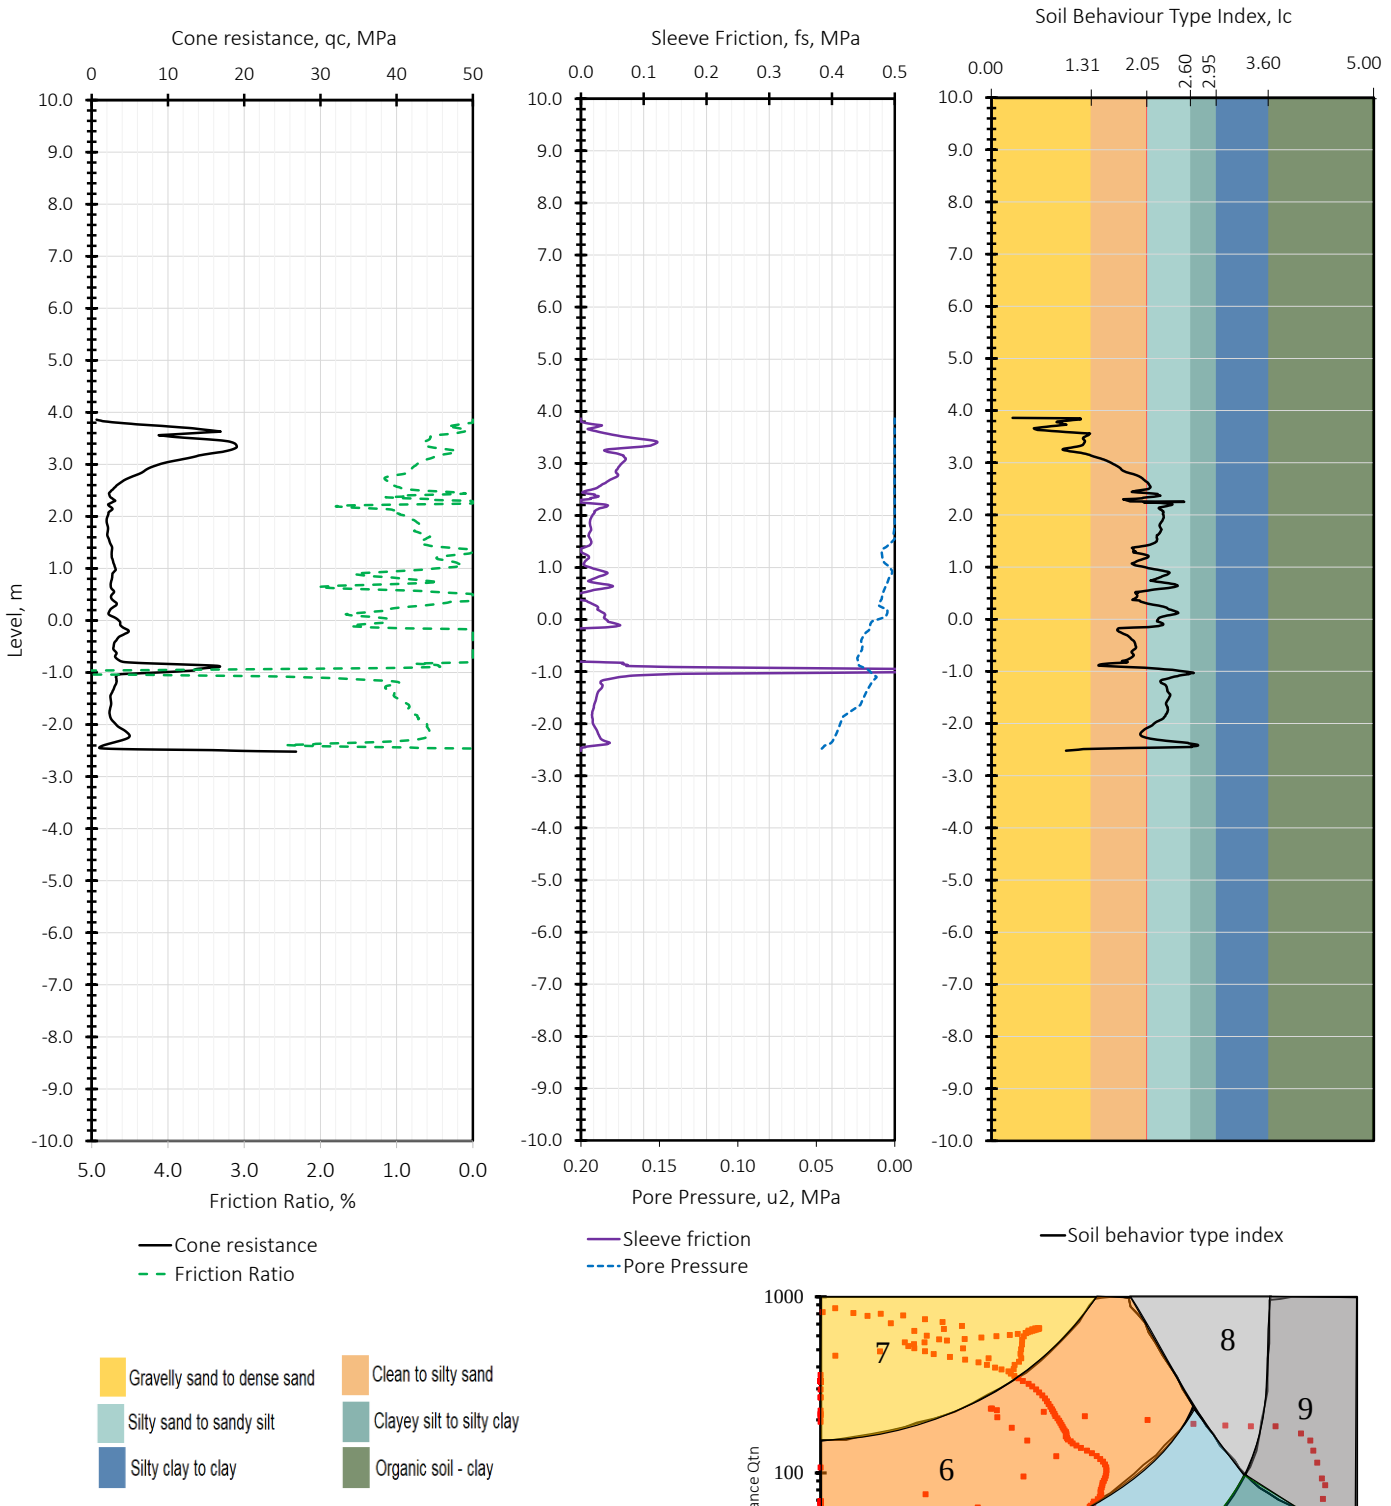

Main Contractor:	CTS GULF	
Test Location:	CPT-A1-B299-100	
Ground Elevation:	3.86	
	Easting	**Northing**
Coordinates:	421065.641	9228161.506
Cone ID:	DP15-CFPTxy.71432	
Test Date	30-Sep-2026	