
Client : SAUDI GLOBAL PORTS

Project : DAMMAM LOGISTICS ZONE

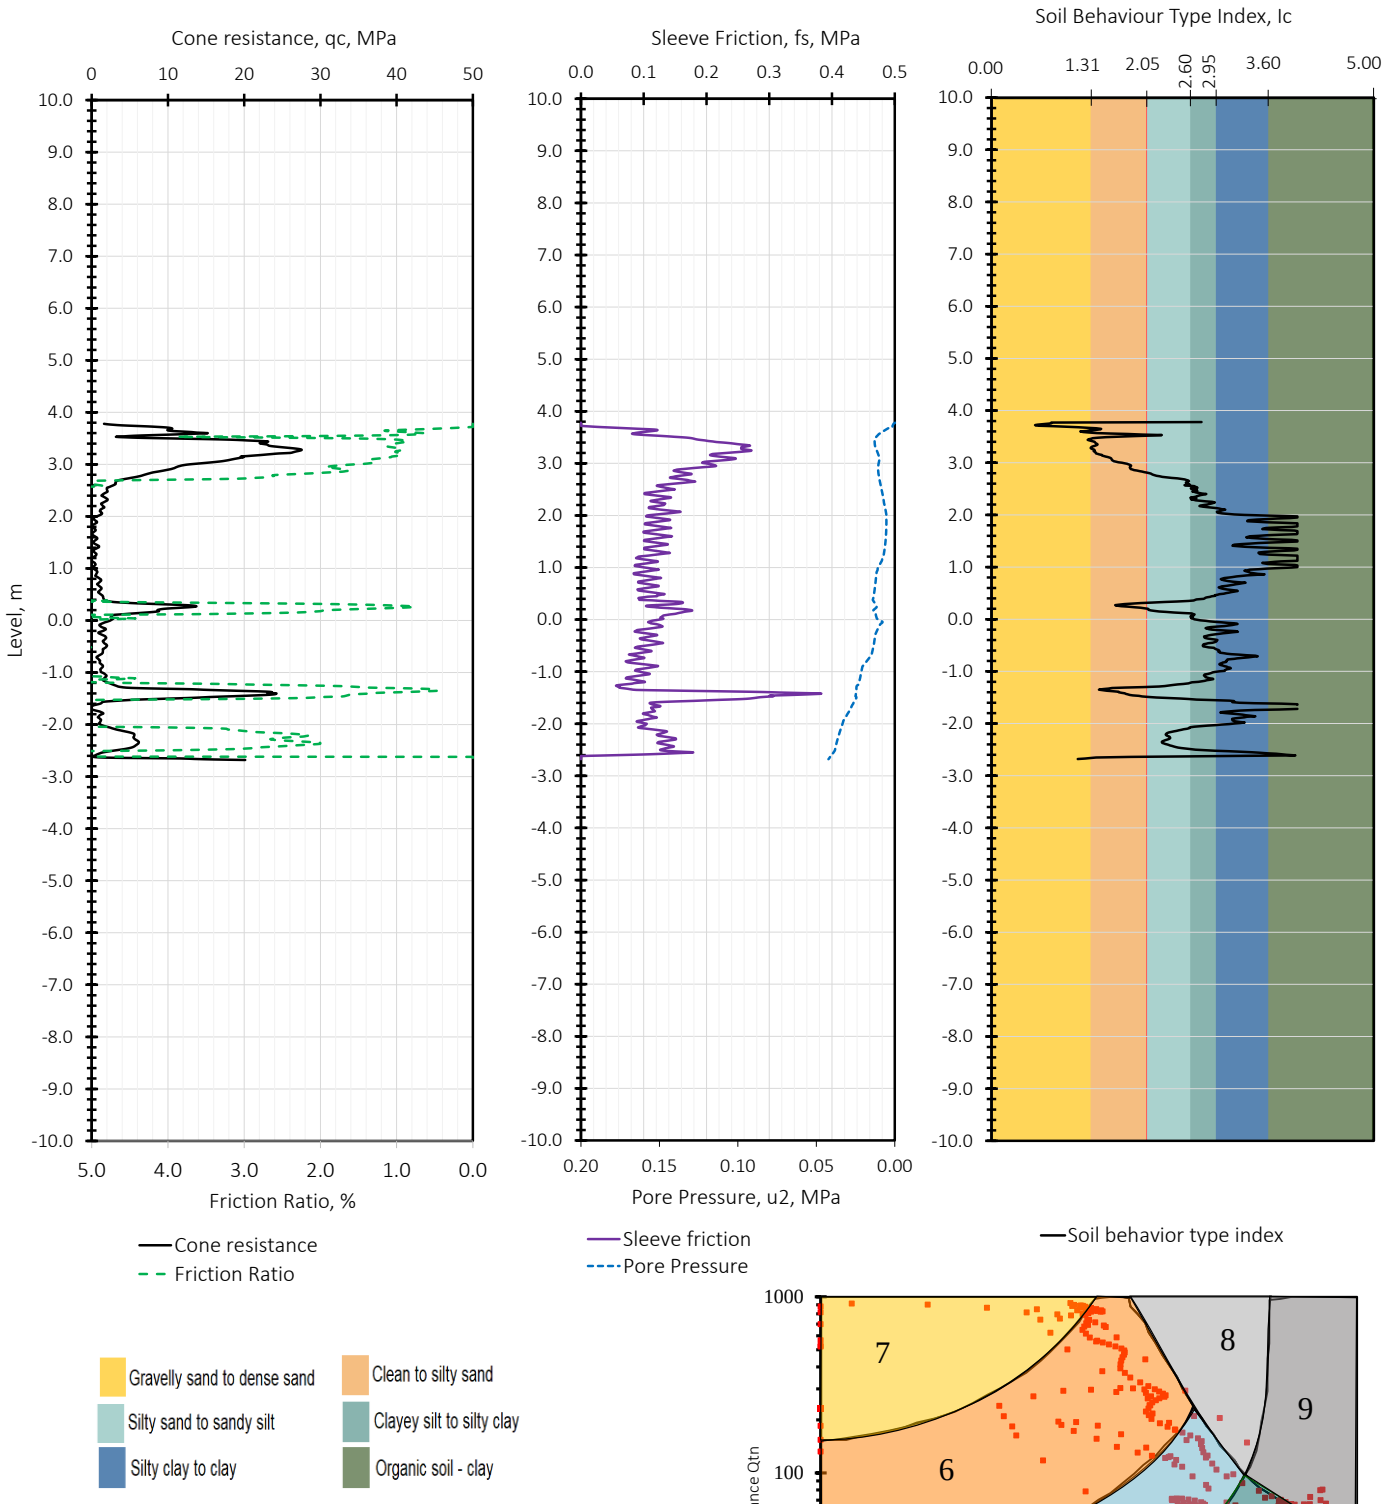

Main Contractor:	CTS GULF	
Test Location:	CPT-A1-B300-100	
Ground Elevation:	3.78	
	Easting	**Northing**
Coordinates:	421072.878	2928185.435
Cone ID:	DP15-CFPTxy.71431	
Test Date	1-Oct-2026	