
Client : SAUDI GLOBAL PORTS

Project : DAMMAM LOGISTICS ZONE

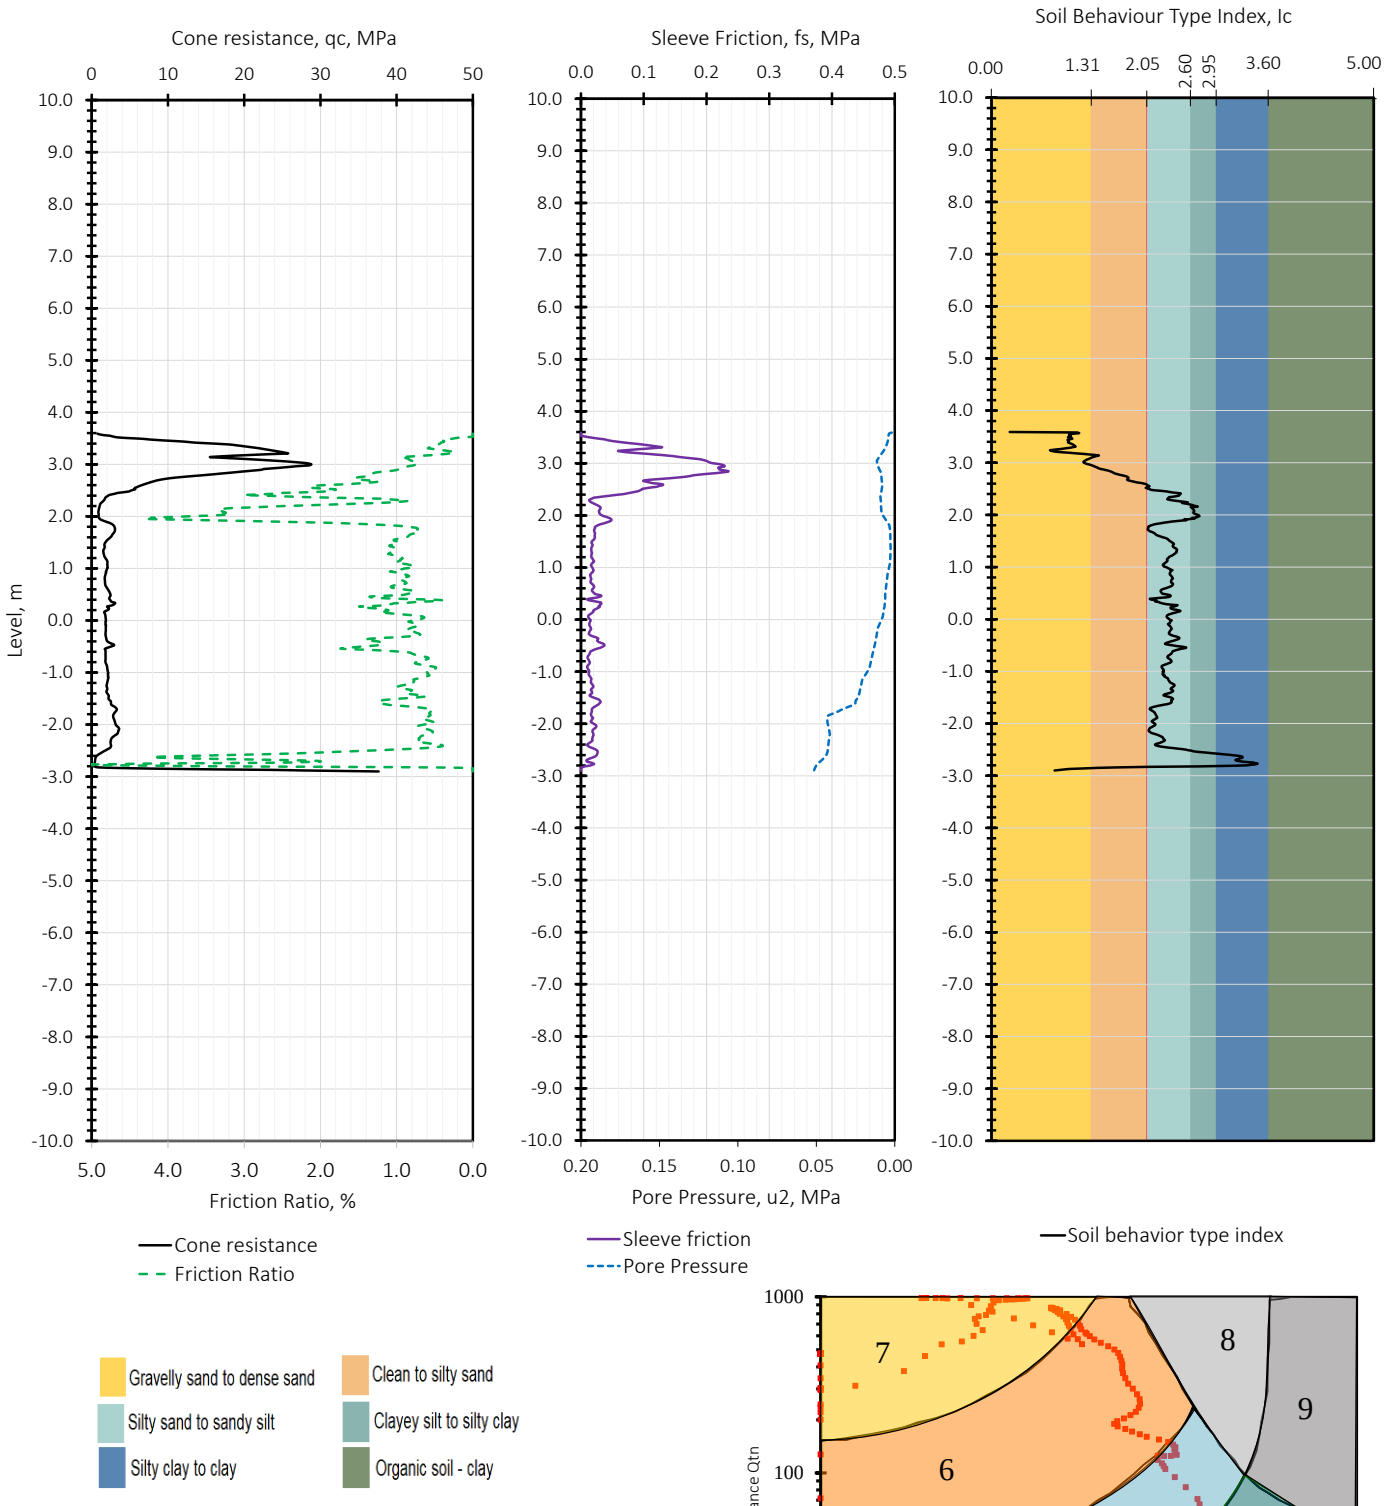

Main Contractor:	CTS GULF	
Test Location:	CPT-A1-B302-100	
Ground Elevation:	3.59	
	Easting	**Northing**
Coordinates:	421087.352	2928233.295
Cone ID:	DP15-CFPTxy.71431	
Test Date	1-Oct-2026	