
Client : SAUDI GLOBAL PORTS

Project : DAMMAM LOGISTICS ZONE

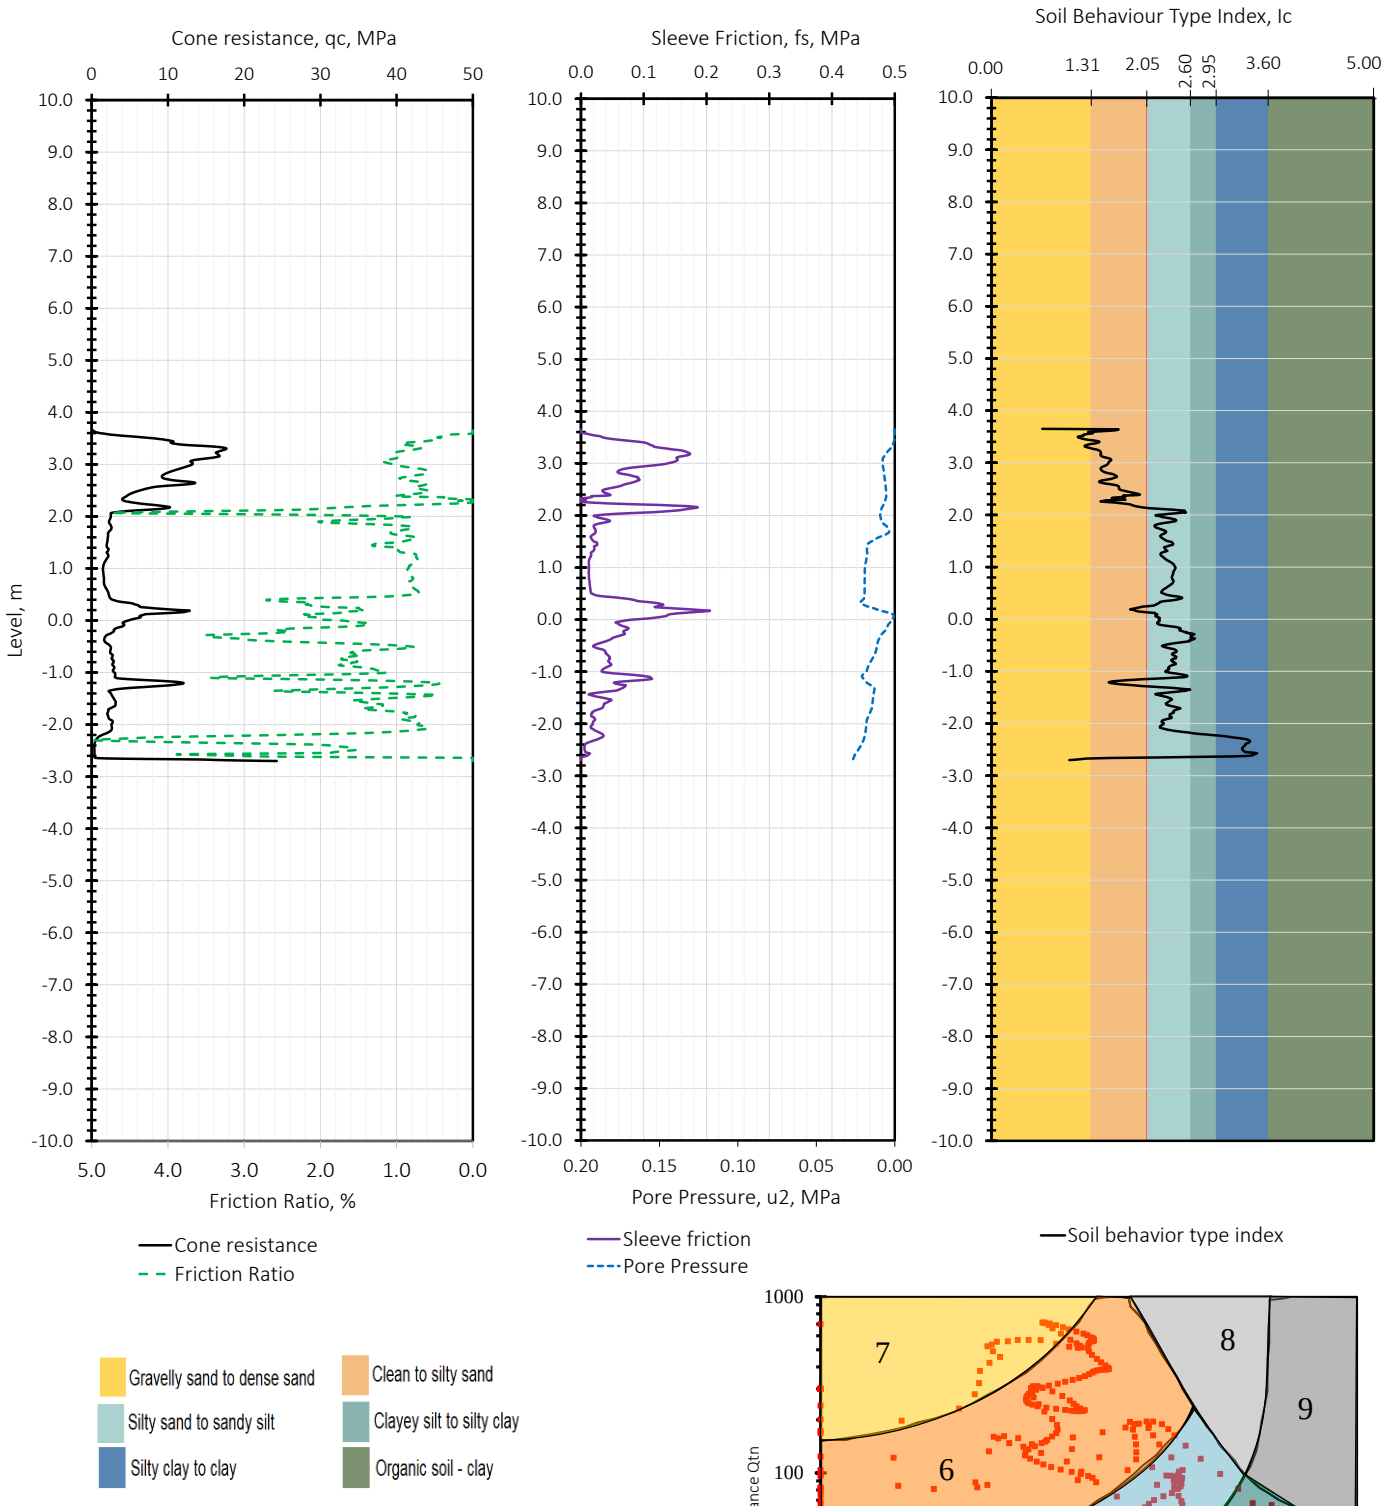

Main Contractor:	CTS GULF	
Test Location:	CPT-A1-B313-100	
Ground Elevation:	3.65	
	Easting	**Northing**
Coordinates:	421104.045	2928202.128
Cone ID:	DP15-CFPTxy.71432	
Test Date	29-Sep-2026	