
Client : SAUDI GLOBAL PORTS

Project : DAMMAM LOGISTICS ZONE

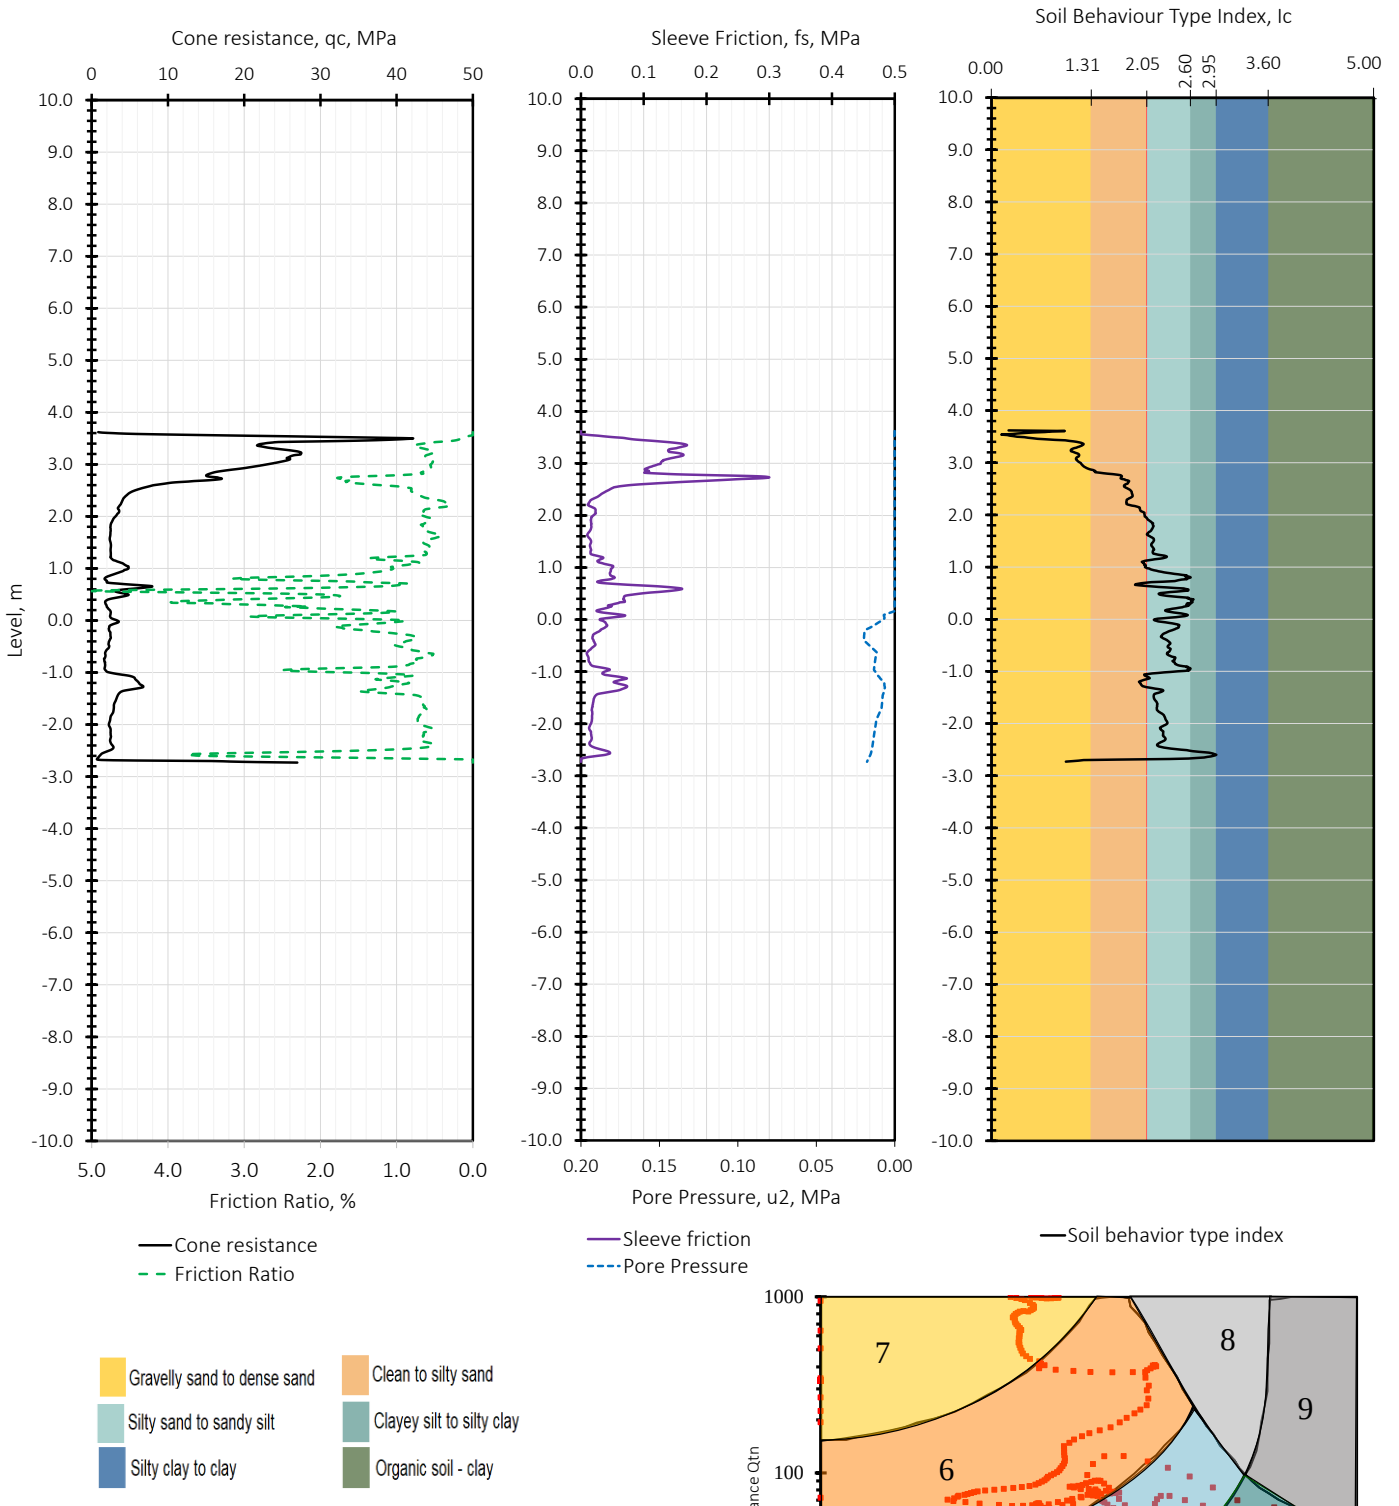

Main Contractor:	CTS GULF	
Test Location:	CPT-A1-B314-100	
Ground Elevation:	3.62	
	Easting	**Northing**
Coordinates:	421111.282	2928226.058
Cone ID:	DP15-CFPTxy.71432	
Test Date	29-Sep-2026	