
Client : SAUDI GLOBAL PORTS

Project : DAMMAM LOGISTICS ZONE

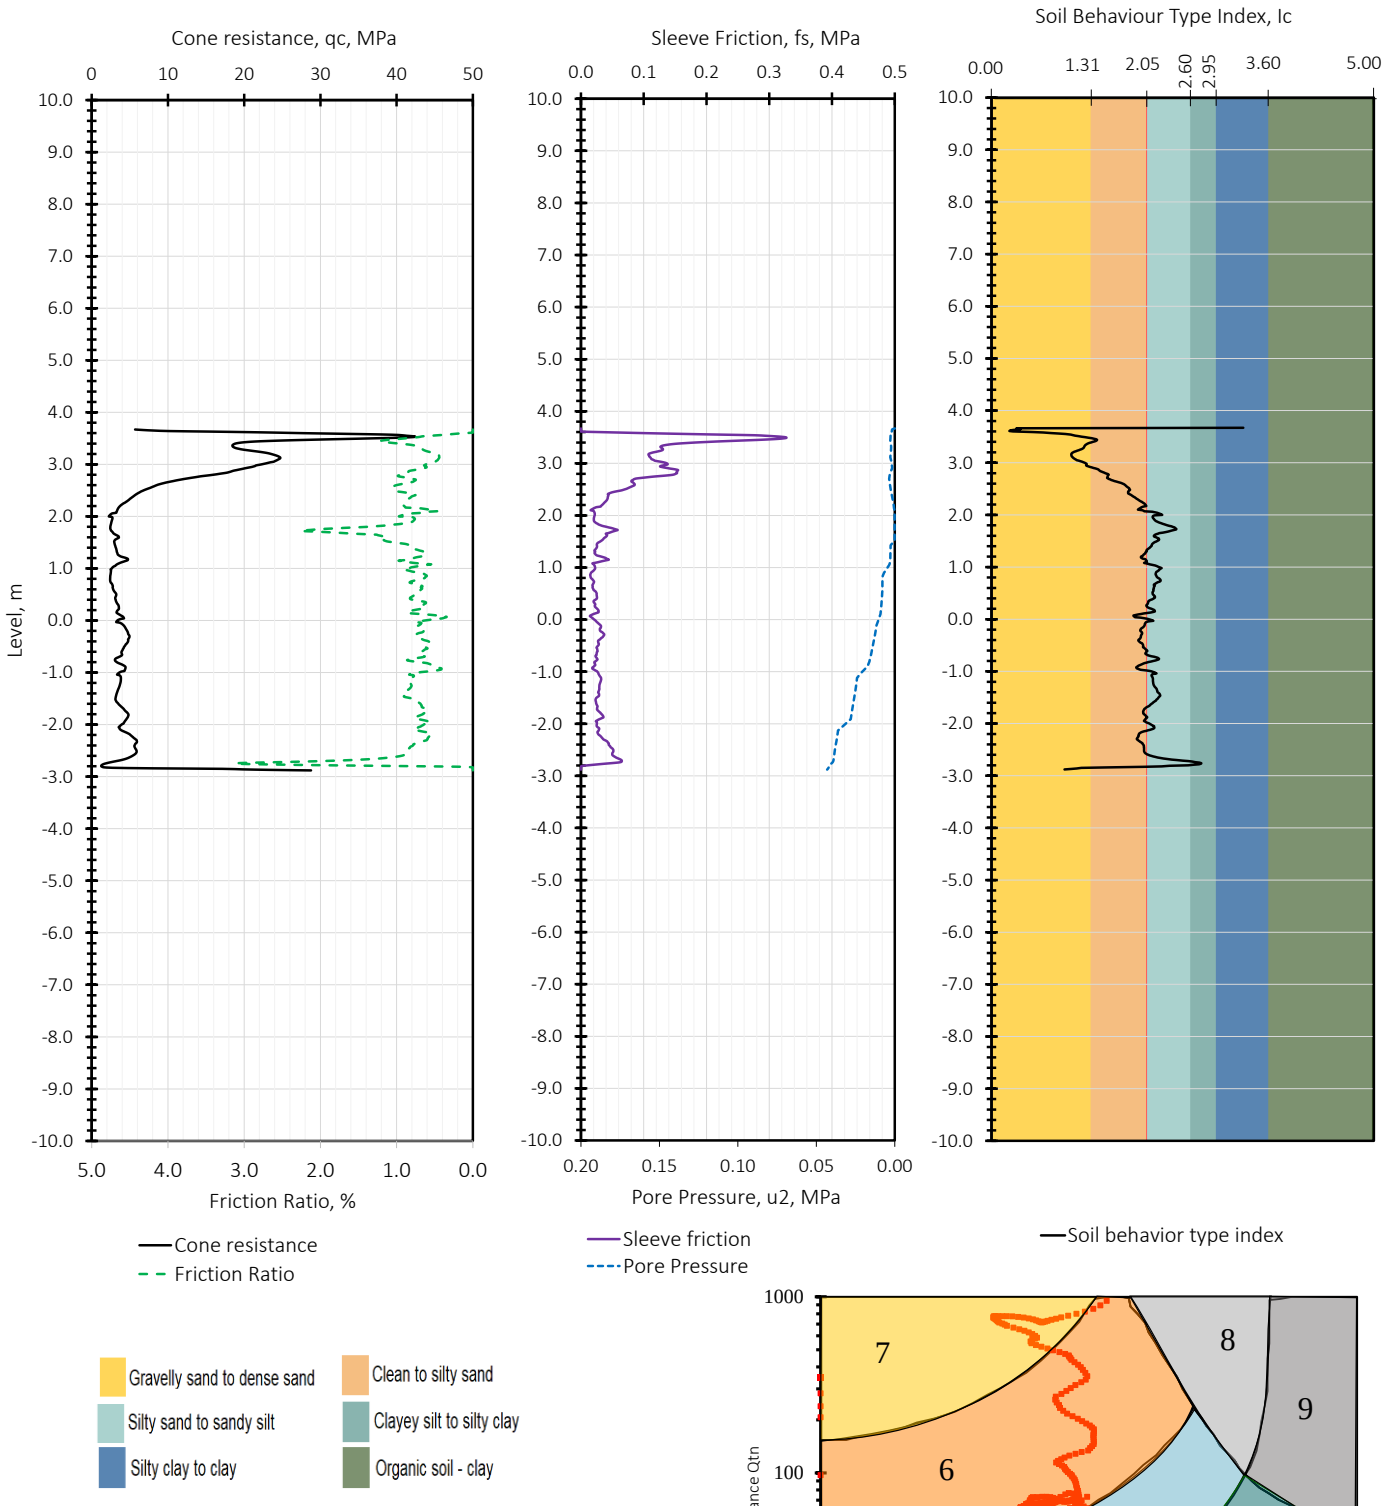

Main Contractor:	CTS GULF	
Test Location:	CPT-A1-B319-100	
Ground Elevation:	3.67	
	Easting	**Northing**
Coordinates:	421147.466	2928345.706
Cone ID:	DP15-CFPTxy.71431	
Test Date	22-Sep-2026	