
Client : SAUDI GLOBAL PORTS

Project : DAMMAM LOGISTICS ZONE

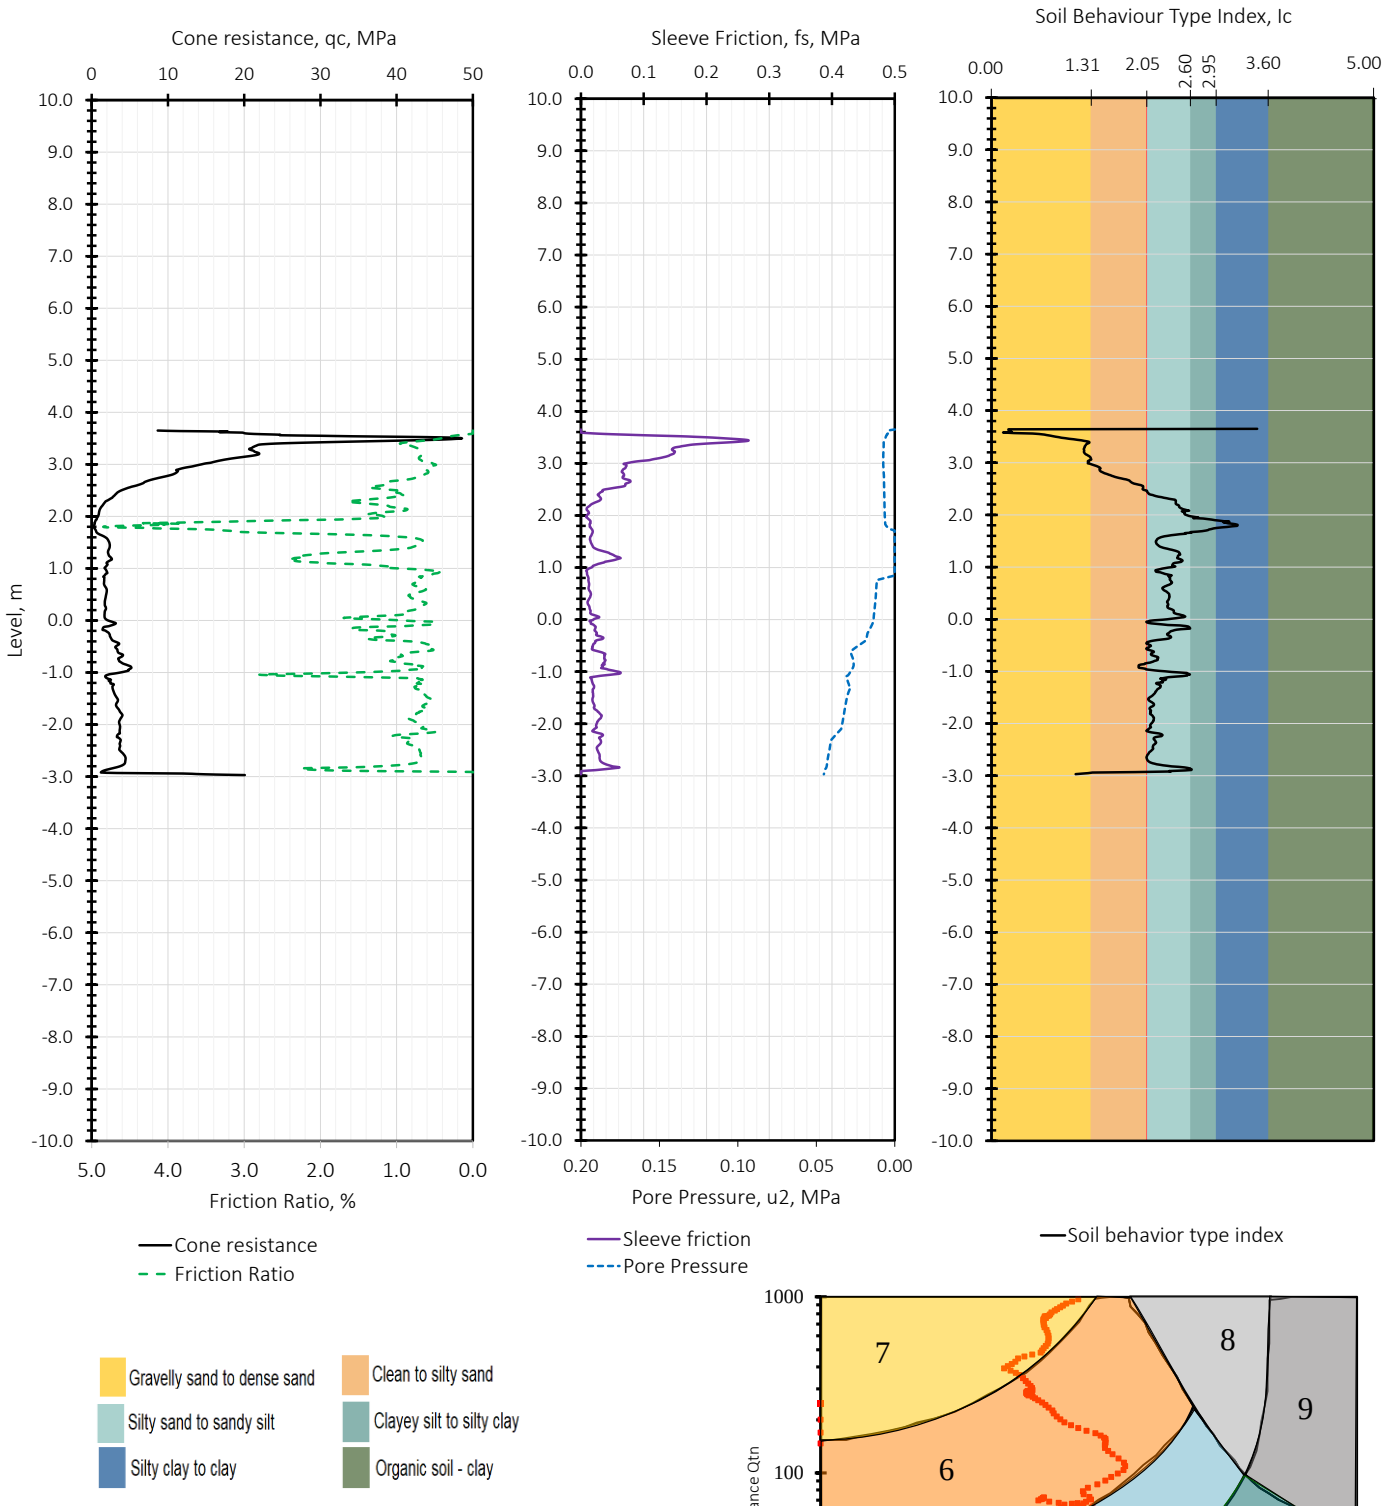

Main Contractor:	CTS GULF	
Test Location:	CPT-A1-B321-100	
Ground Elevation:	3.65	
	Easting	**Northing**
Coordinates:	421174.073	2928392.277
Cone ID:	DP15-CFPTxy.71431	
Test Date	22-Sep-2026	