
Client : SAUDI GLOBAL PORTS

Project : DAMMAM LOGISTICS ZONE

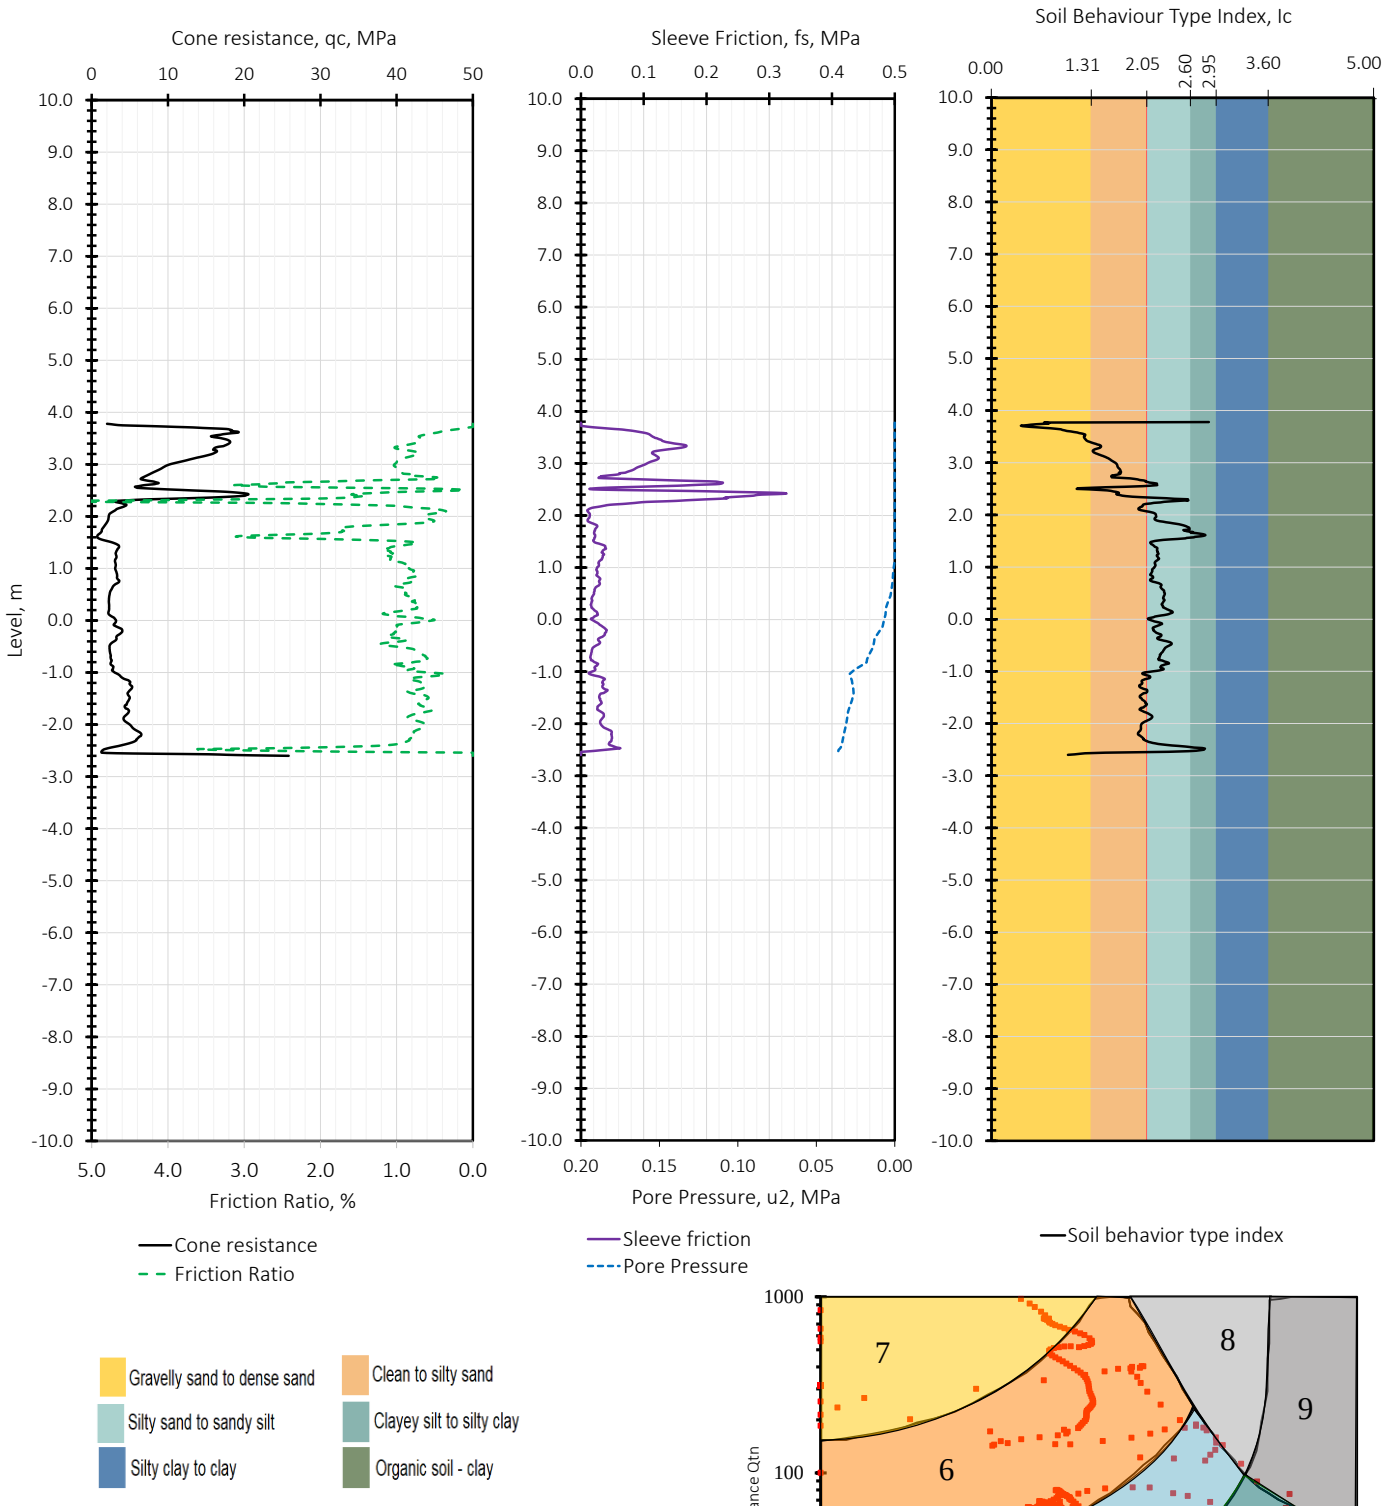

Main Contractor:	CTS GULF	
Test Location:	CPT-A1-B323-100	
Ground Elevation:	3.78	
	Easting	**Northing**
Coordinates:	421106.264	2928123.102
Cone ID:	DP15-CFPTxy.71432	
Test Date	28-Sep-2026	