
Client : SAUDI GLOBAL PORTS

Project : DAMMAM LOGISTICS ZONE

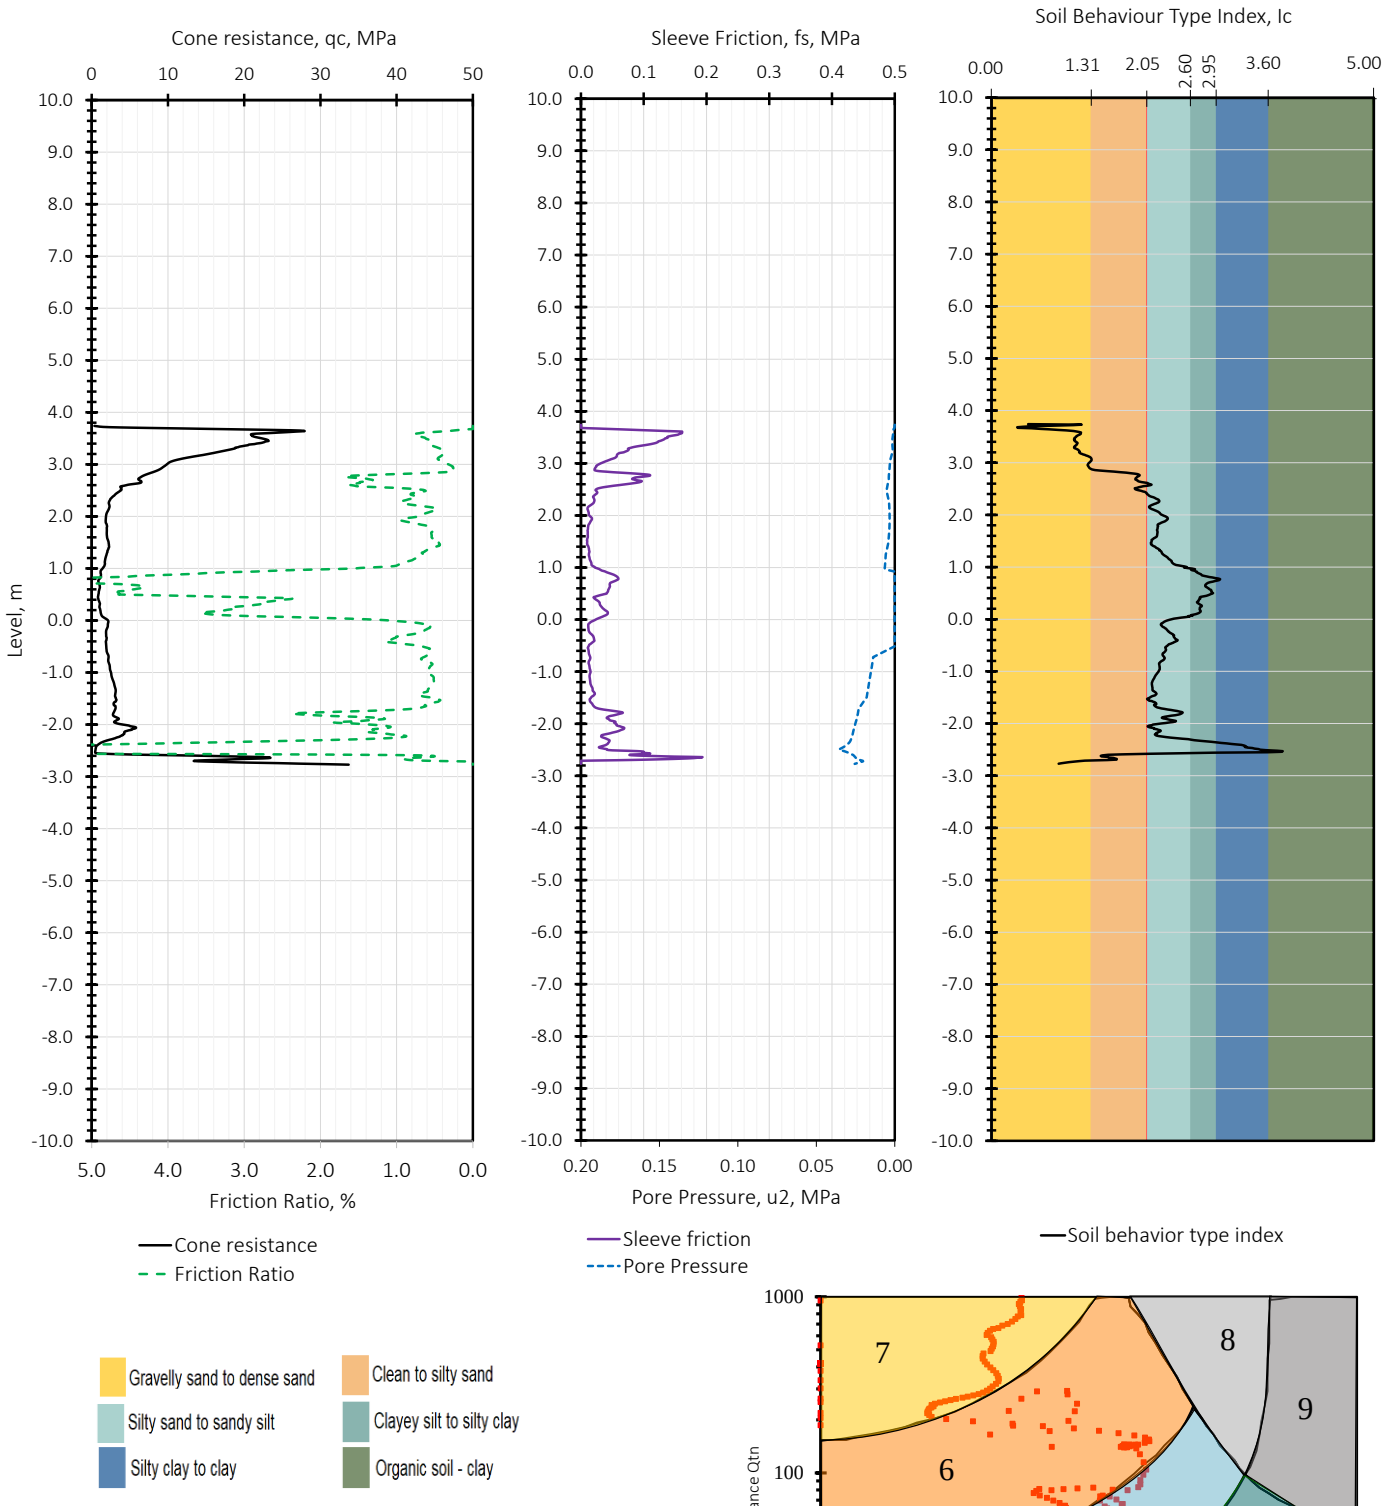

Main Contractor:	CTS GULF	
Test Location:	CPT-A1-B327-100-1	
Ground Elevation:	3.74	
	Easting	**Northing**
Coordinates:	421135.211	2928218.821
Cone ID:	DP15-CFPTxy.71432	
Test Date	28-Sep-2026	