
Client : SAUDI GLOBAL PORTS

Project : DAMMAM LOGISTICS ZONE

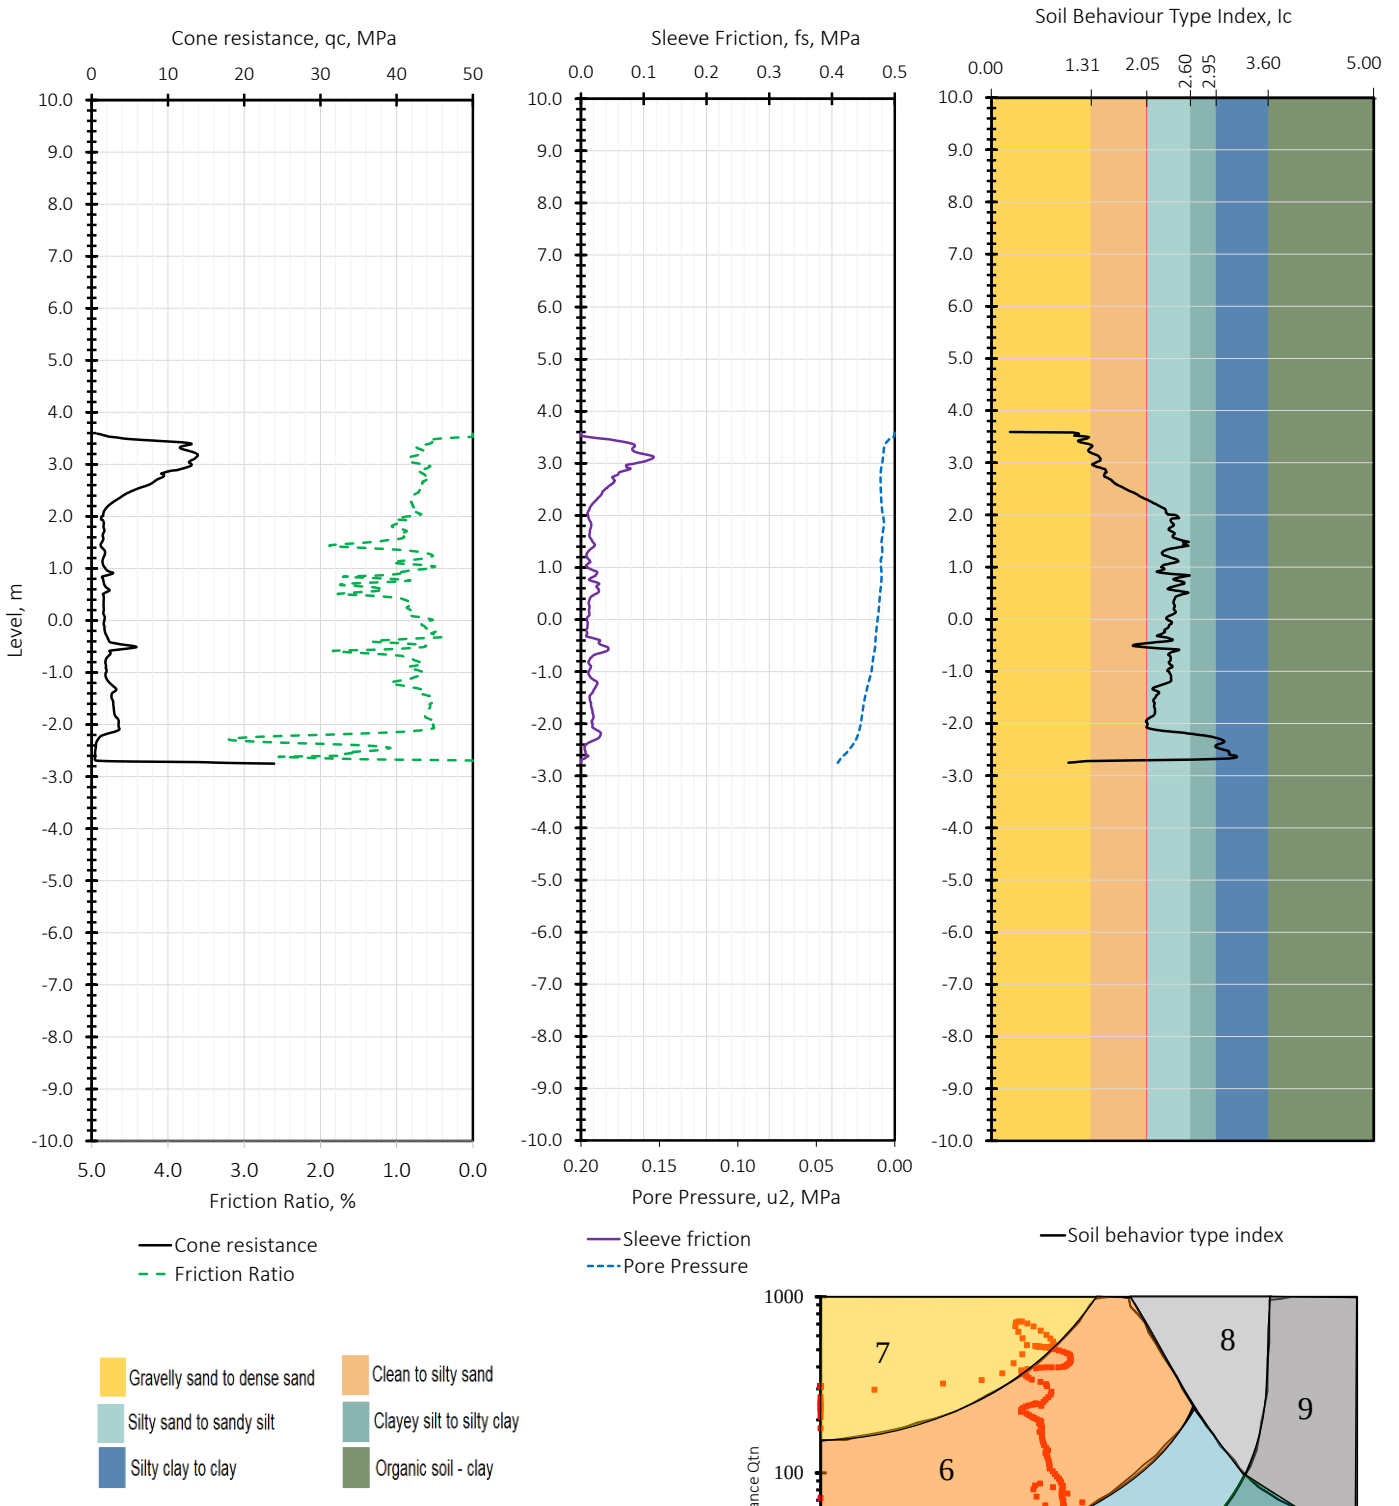

Main Contractor:	CTS GULF	
Test Location:	CPT-A1-B328-100	
Ground Elevation:	3.59	
	Easting	**Northing**
Coordinates:	421142.448	2928242.751
Cone ID:	DP15-CFPTxy.71431	
Test Date	21-Sep-2026	