
Client : SAUDI GLOBAL PORTS

Project : DAMMAM LOGISTICS ZONE

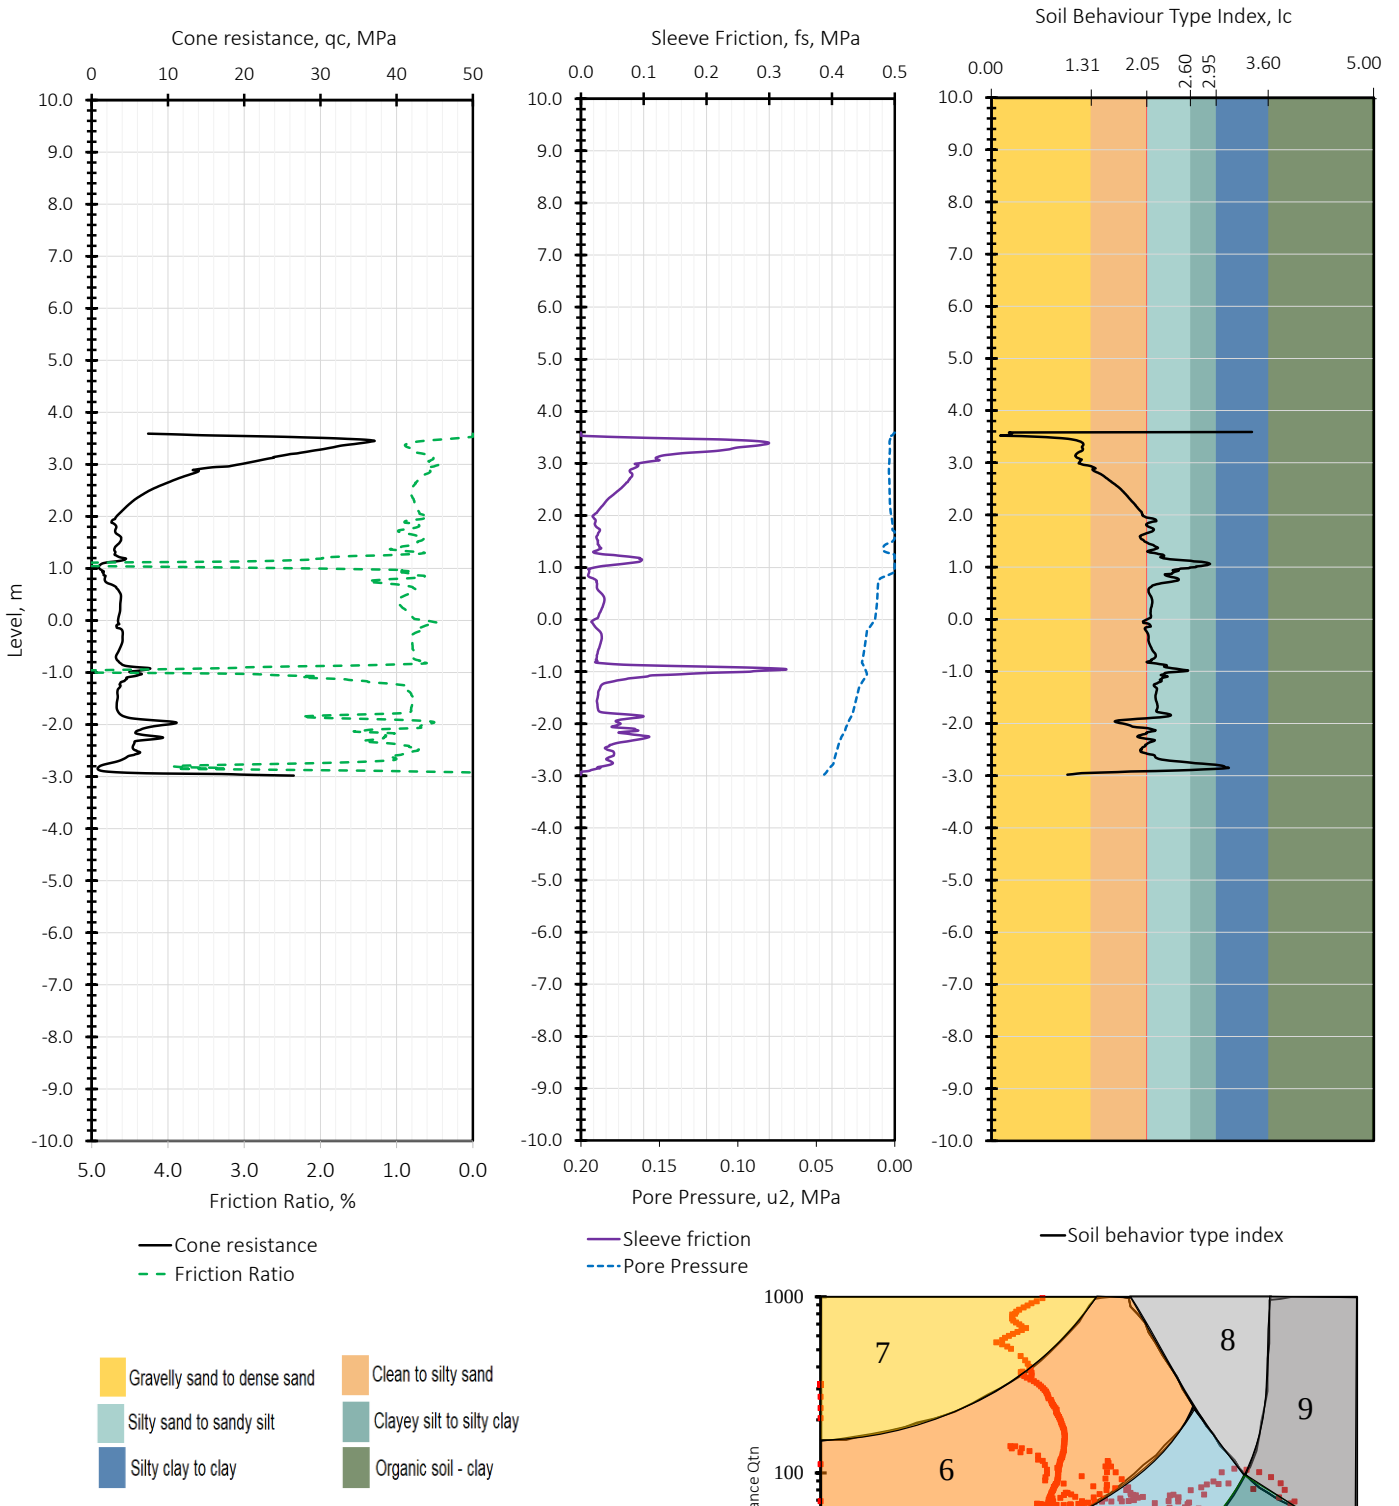

Main Contractor:	CTS GULF	
Test Location:	CPT-A1-B333-100	
Ground Elevation:	3.59	
	Easting	**Northing**
Coordinates:	421178.632	2928362.399
Cone ID:	DP15-CFPTxy.71431	
Test Date	22-Sep-2026	