

Client : SAUDI GLOBAL PORTS

Project : DAMMAM LOGISTICS ZONE

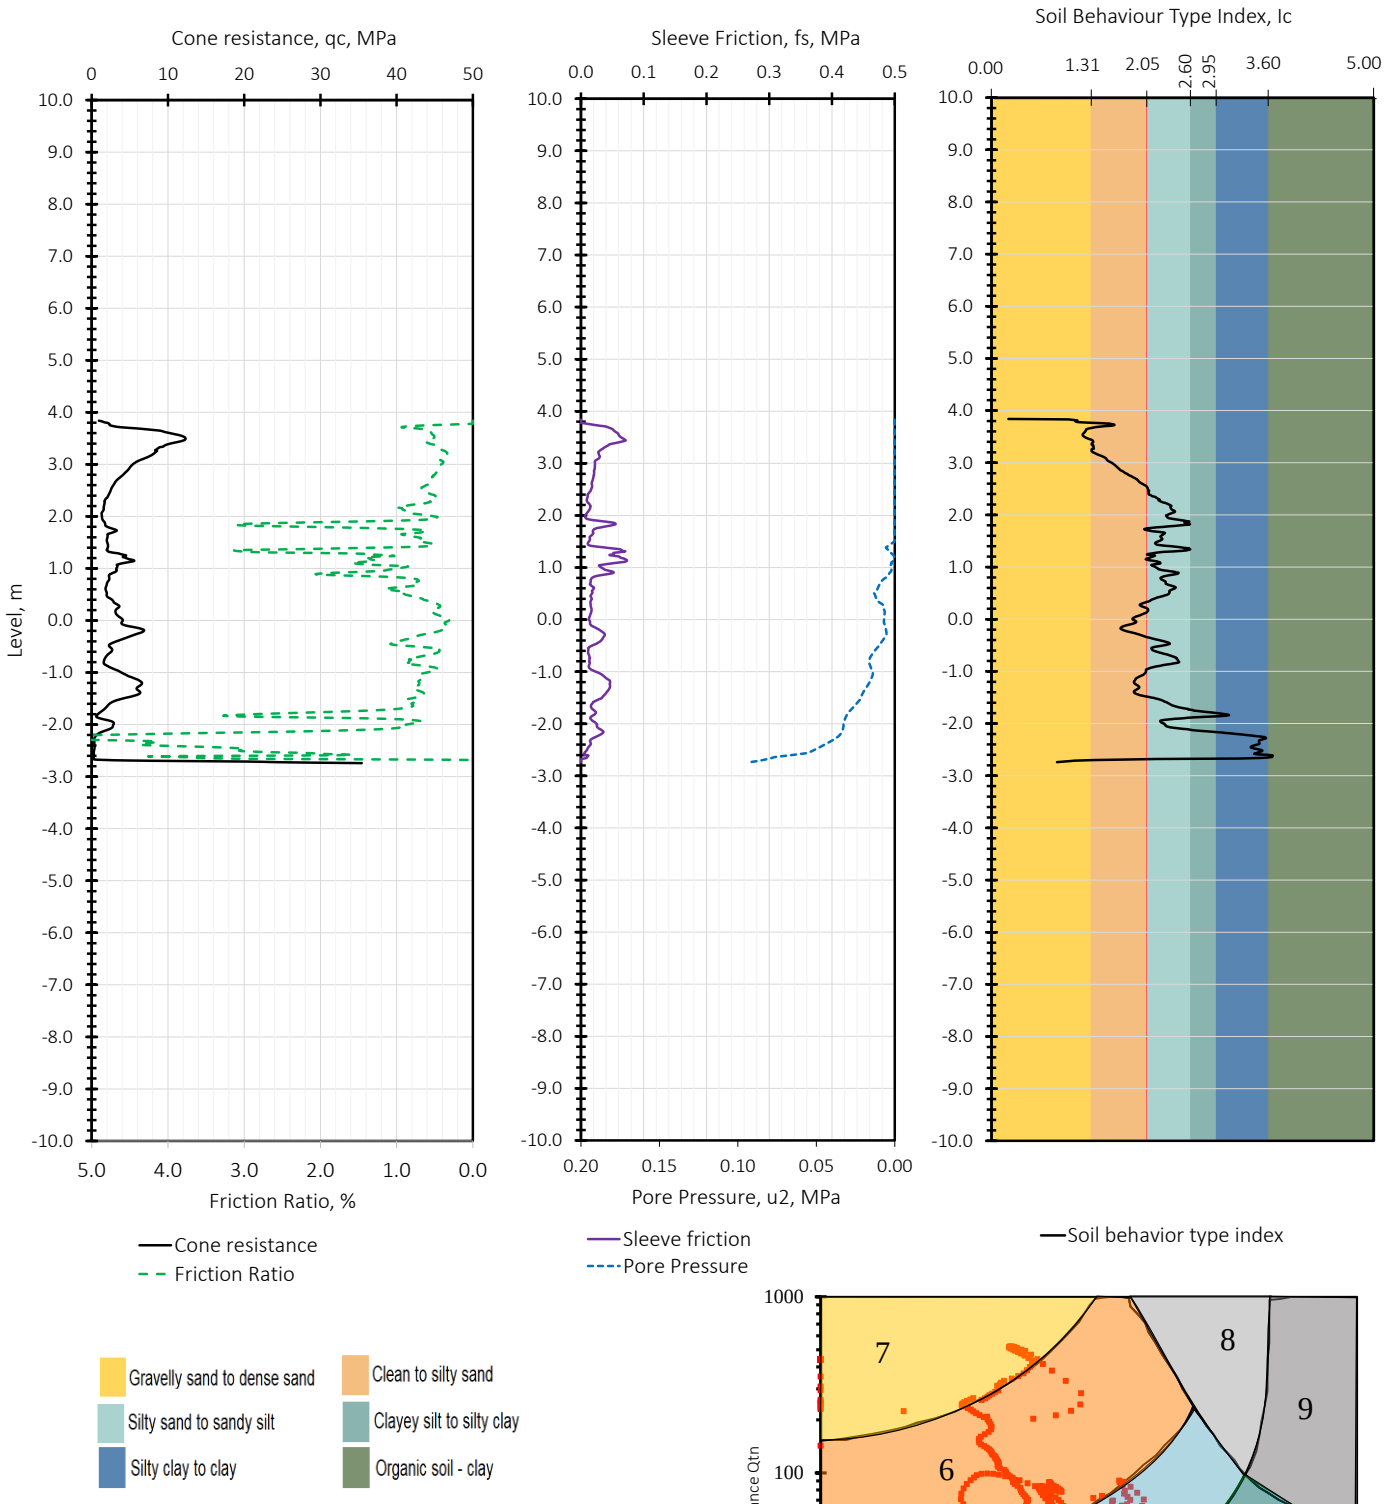

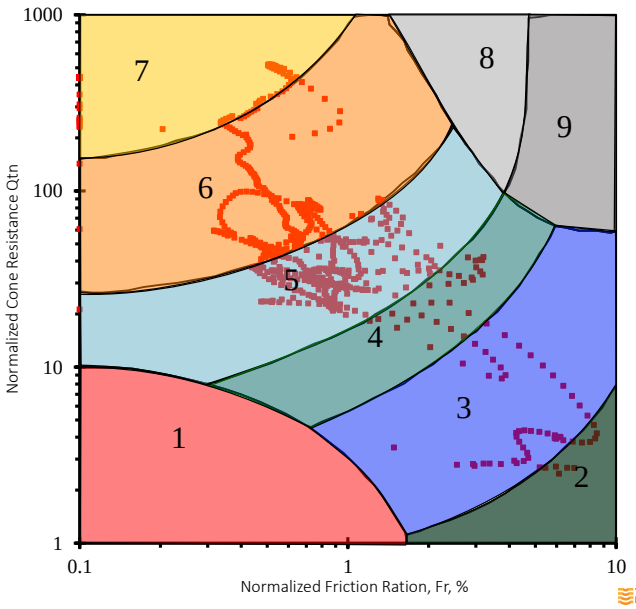

Main Contractor:	CTS GULF	
Test Location:	CPT-A1-B337-100	
Ground Elevation:	3.84	
	Easting	**Northing**
Coordinates:	421144.667	2928163.725
Cone ID:	DP15-CFPTxy.71432	
Test Date	29-Sep-2026	