
Client : SAUDI GLOBAL PORTS

Project : DAMMAM LOGISTICS ZONE

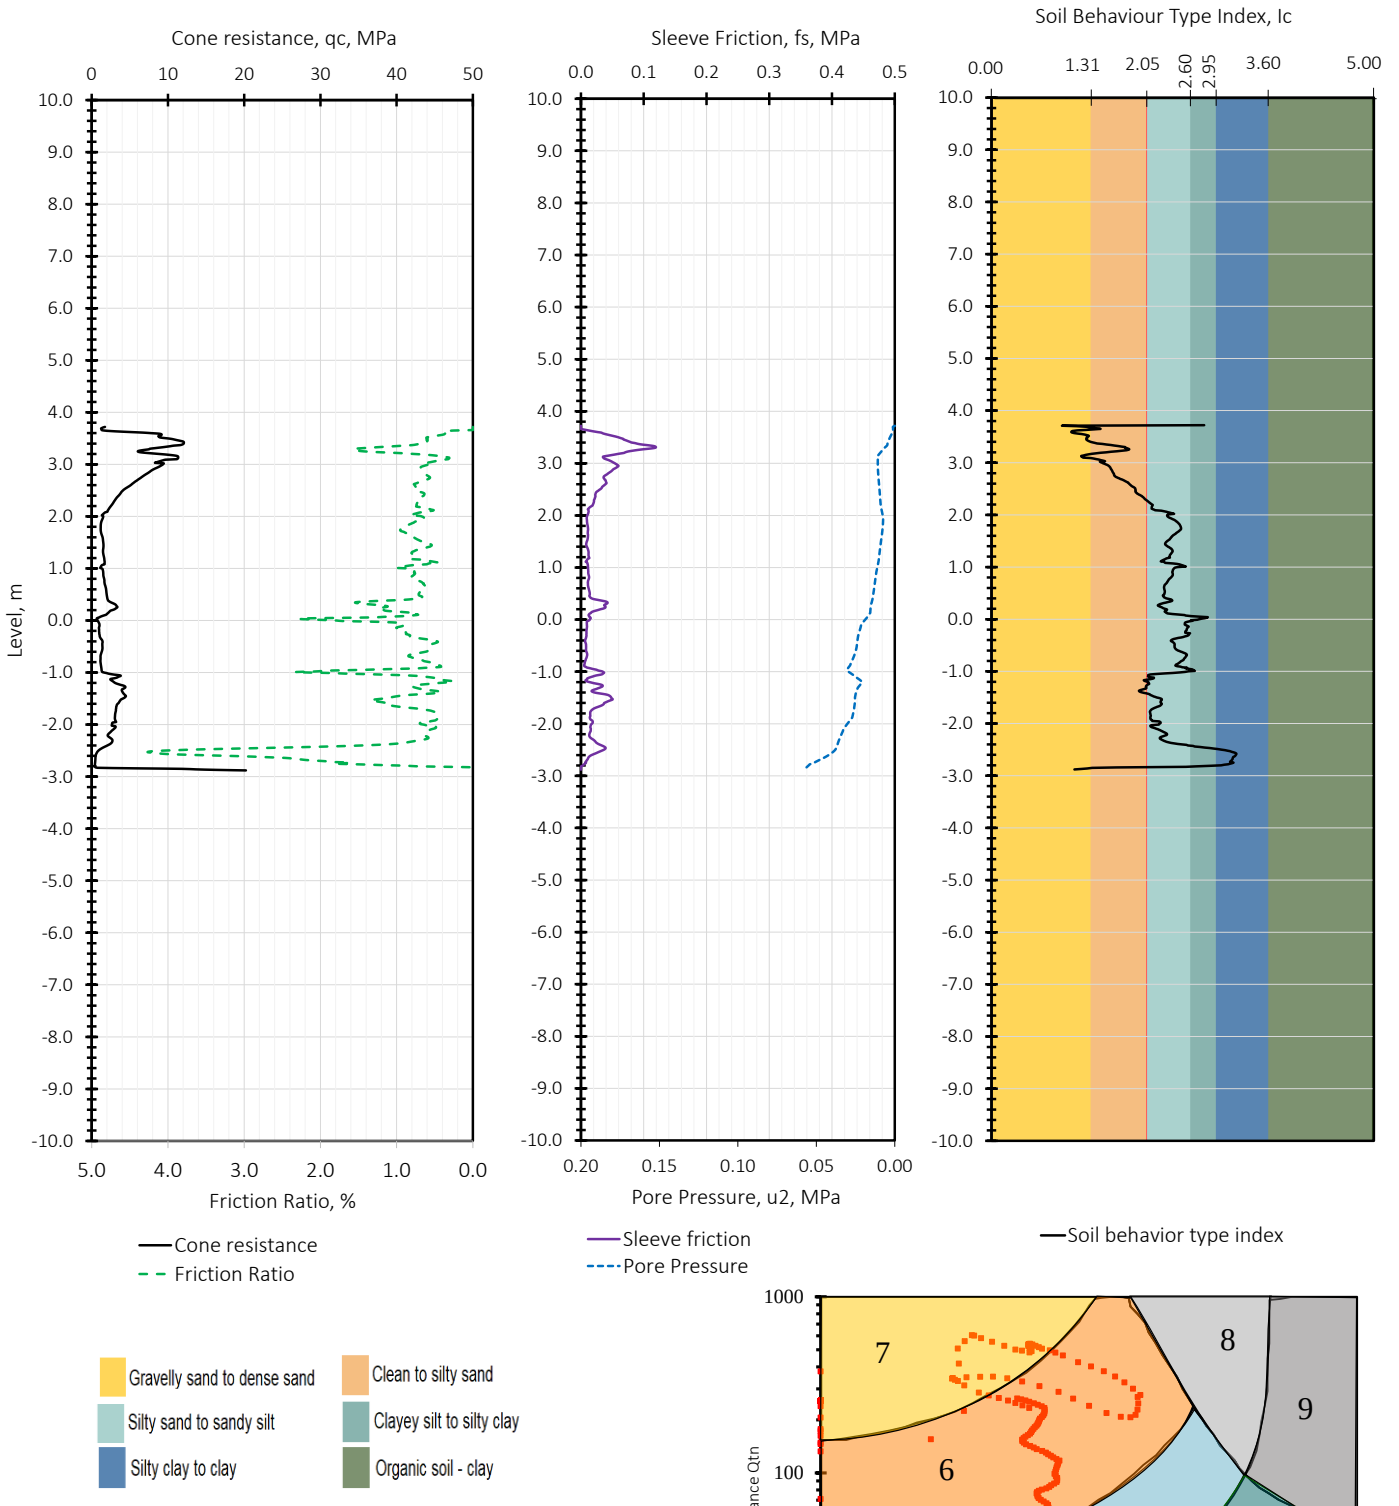

Main Contractor:	CTS GULF	
Test Location:	CPT-A1-B342-100	
Ground Elevation:	3.72	
	Easting	**Northing**
Coordinates:	421180.851	2928283.373
Cone ID:	DP15-CFPTxy.71431	
Test Date	21-Sep-2026	