
Client : SAUDI GLOBAL PORTS

Project : DAMMAM LOGISTICS ZONE

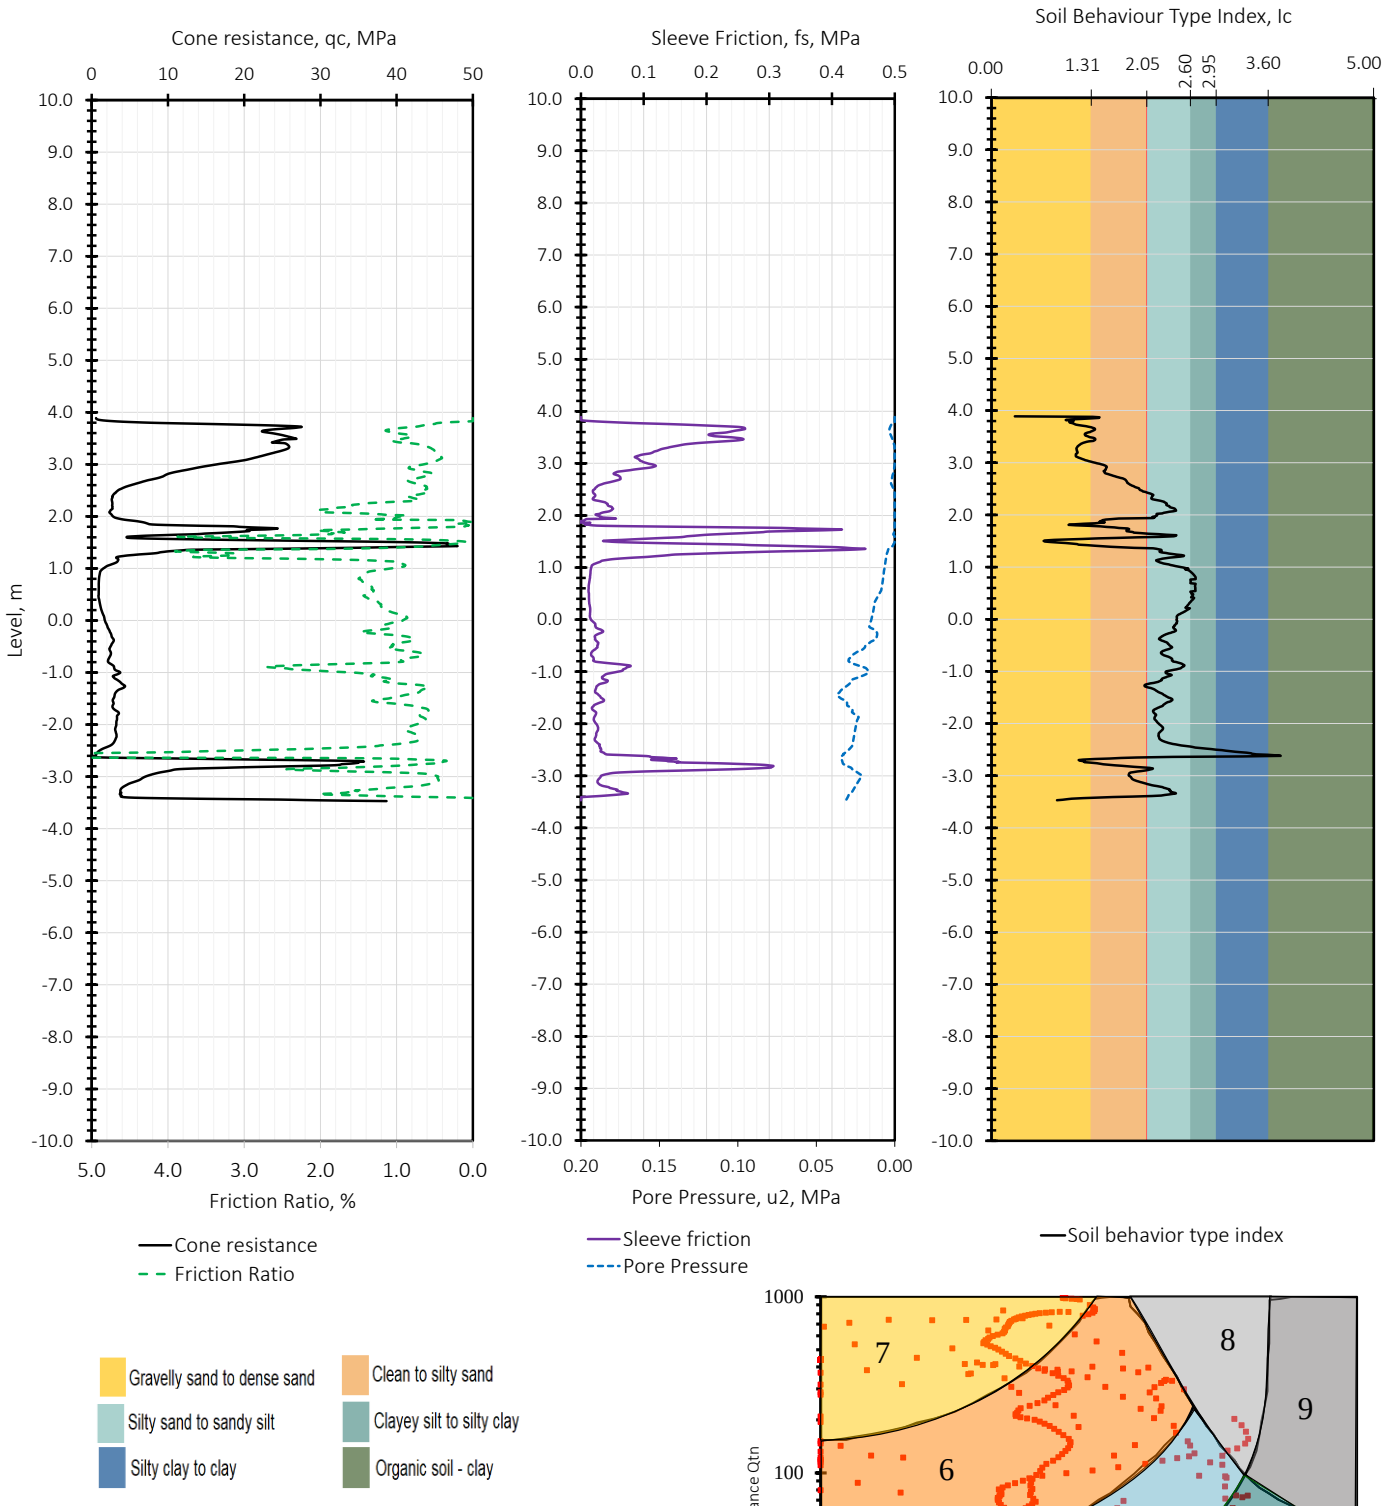

Main Contractor:	CTS GULF	
Test Location:	CPT-A1-B348-100	
Ground Elevation:	3.89	
	Easting	**Northing**
Coordinates:	421154.123	2928108.629
Cone ID:	DP15-CFPTxy.71432	
Test Date	29-Sep-2026	