

Client : SAUDI GLOBAL PORTS

Project : DAMMAM LOGISTICS ZONE

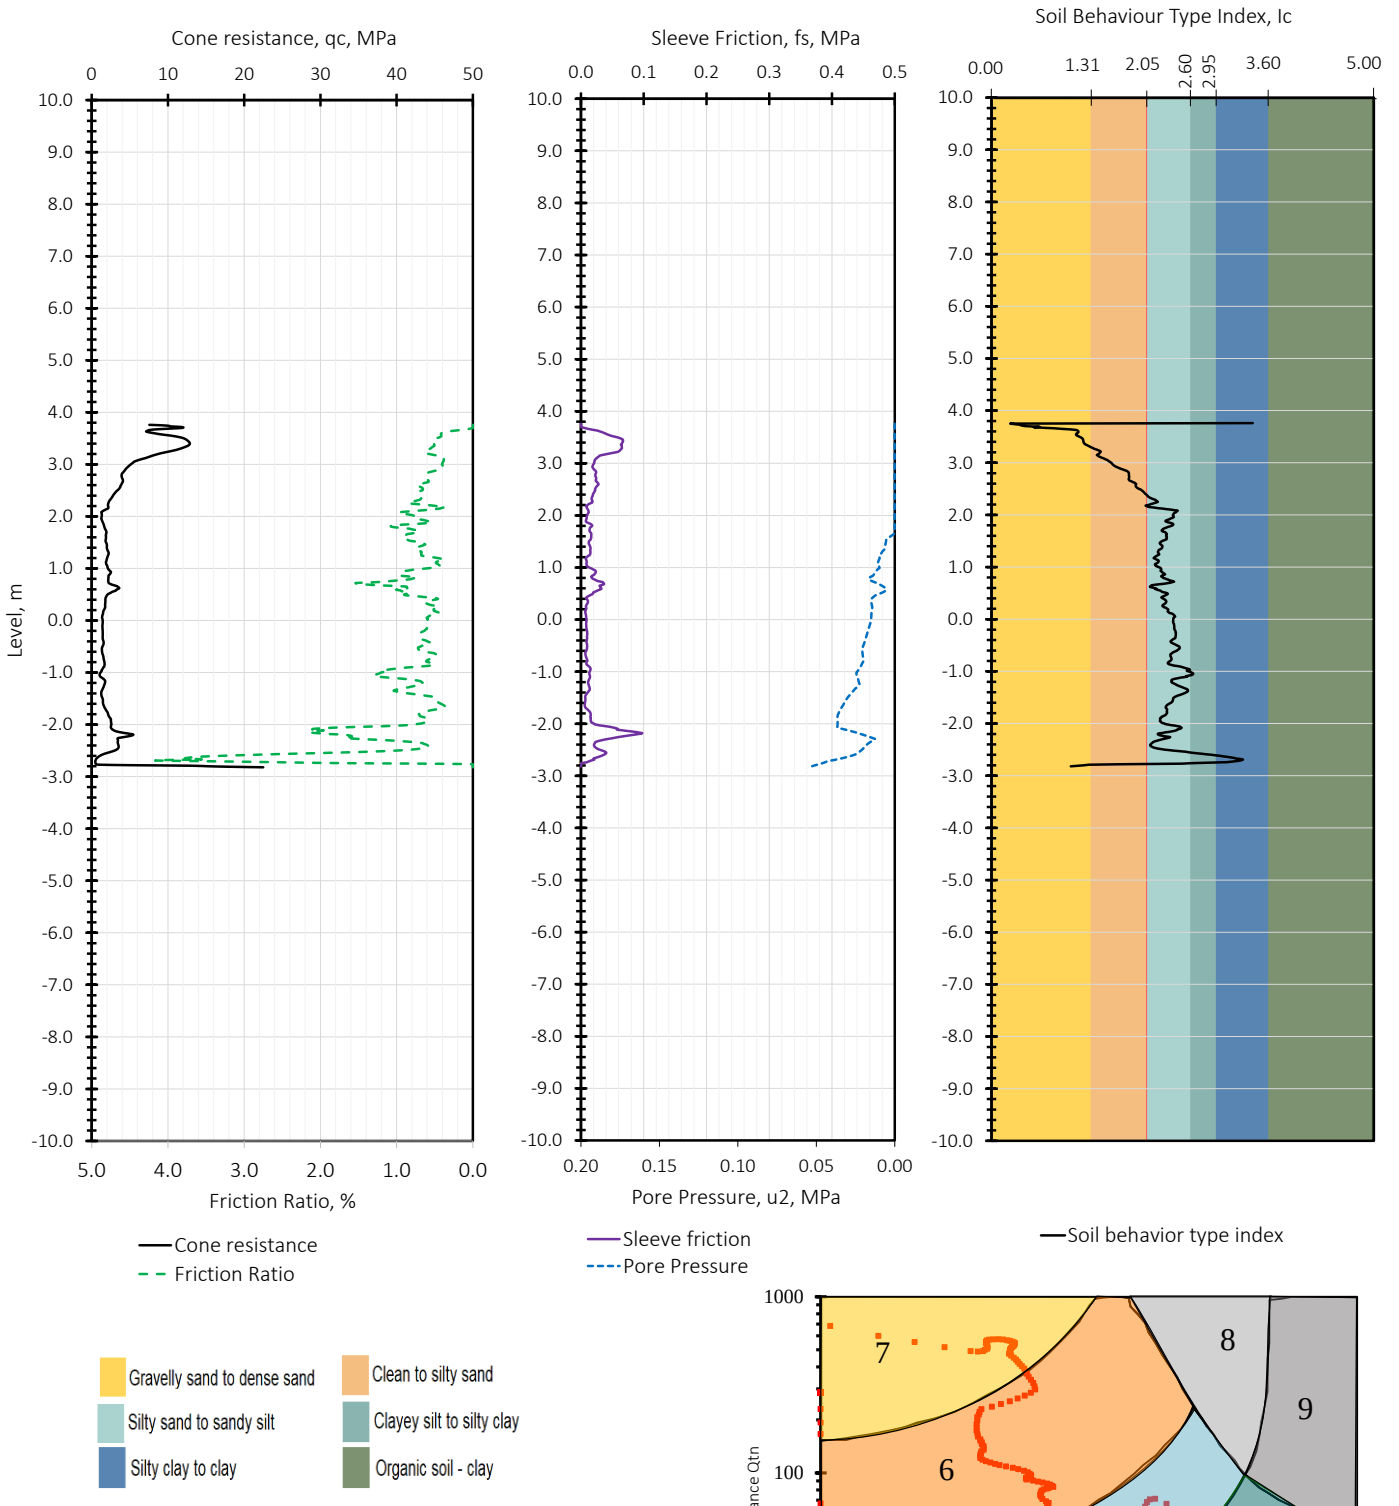

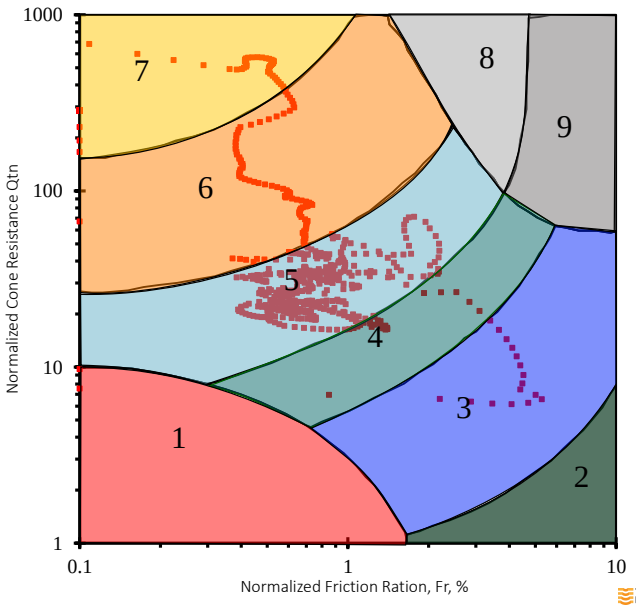

Main Contractor:	CTS GULF	
Test Location:	CPT-A1-B355-100	
Ground Elevation:	3.76	
	Easting	**Northing**
Coordinates:	421204.781	2928276.136
Cone ID:	DP15-CFPTxy.71431	
Test Date	21-Sep-2026	