
Client : SAUDI GLOBAL PORTS

Project : DAMMAM LOGISTICS ZONE

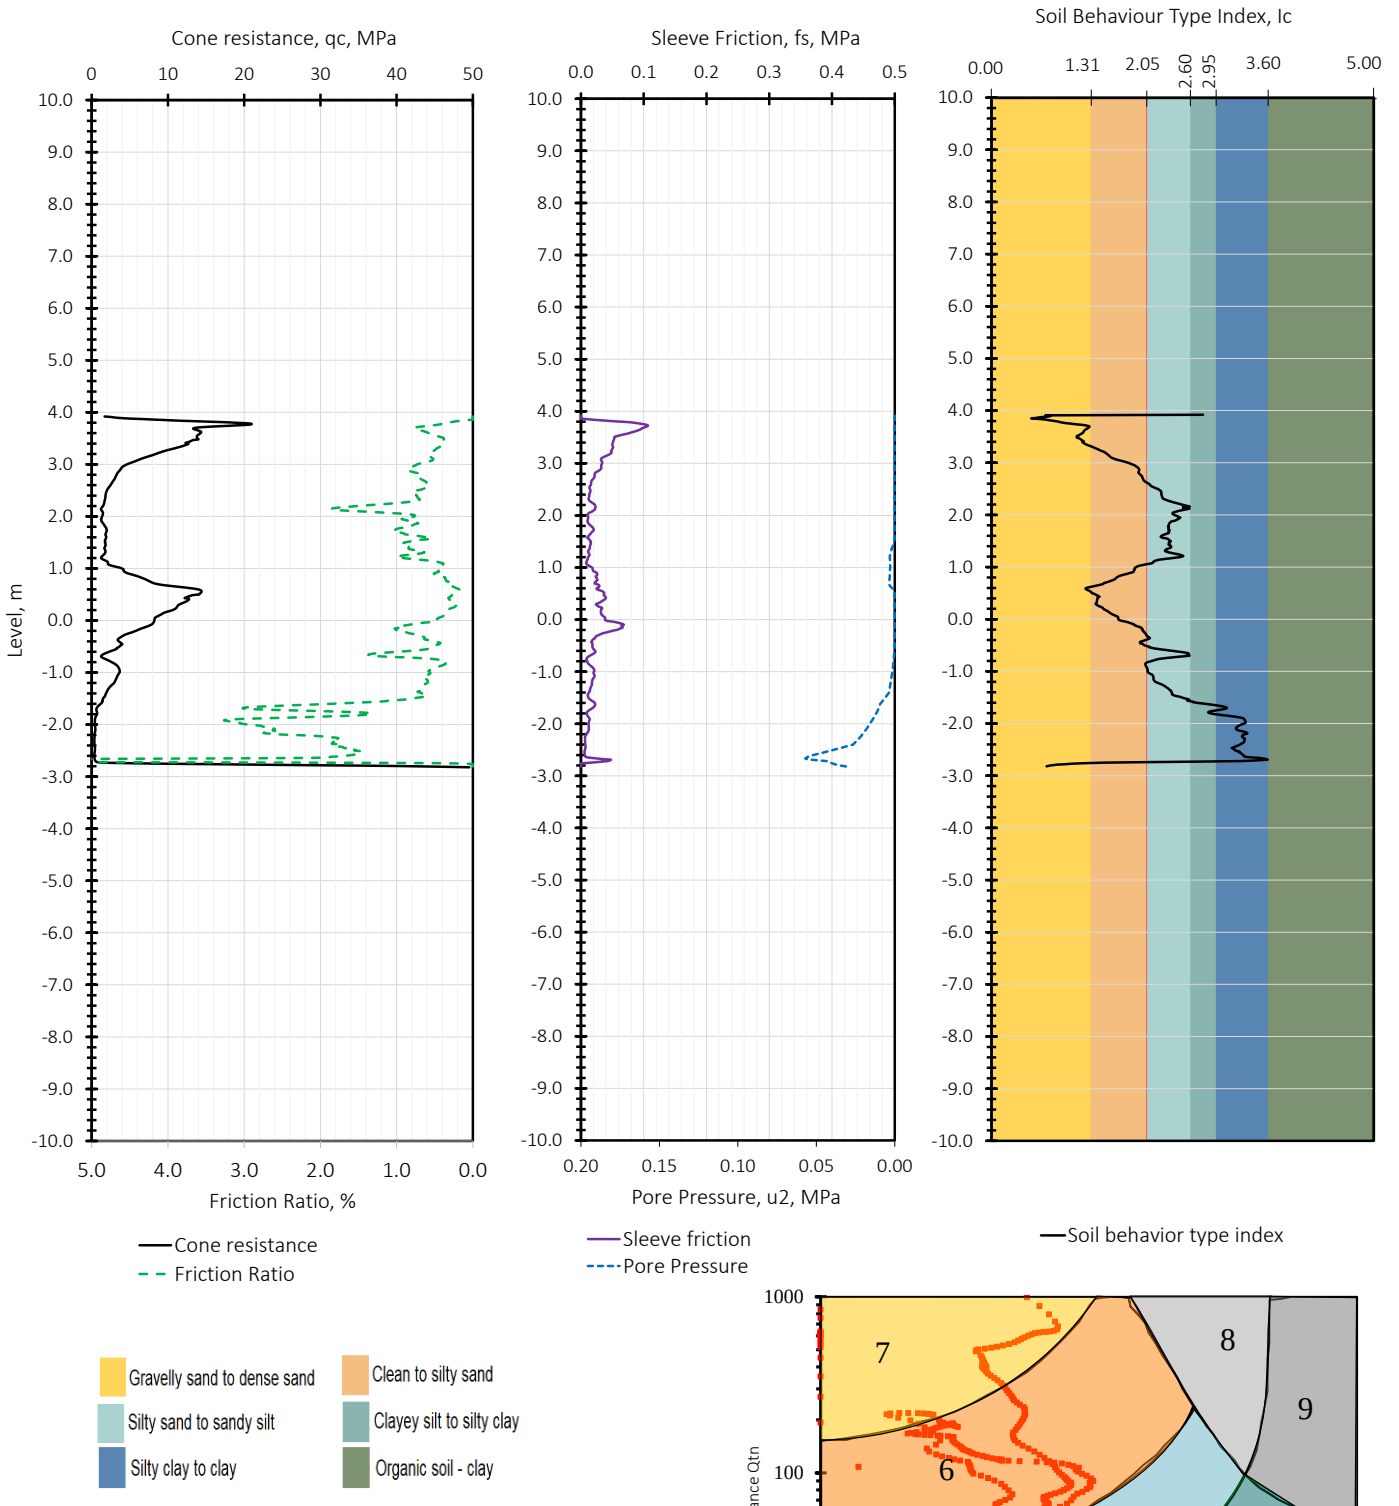

Main Contractor:	CTS GULF	
Test Location:	CPT-A1-B361-100	
Ground Elevation:	3.92	
	Easting	**Northing**
Coordinates:	421192.526	2928149.251
Cone ID:	DP15-CFPTxy.71432	
Test Date	29-Sep-2026	